
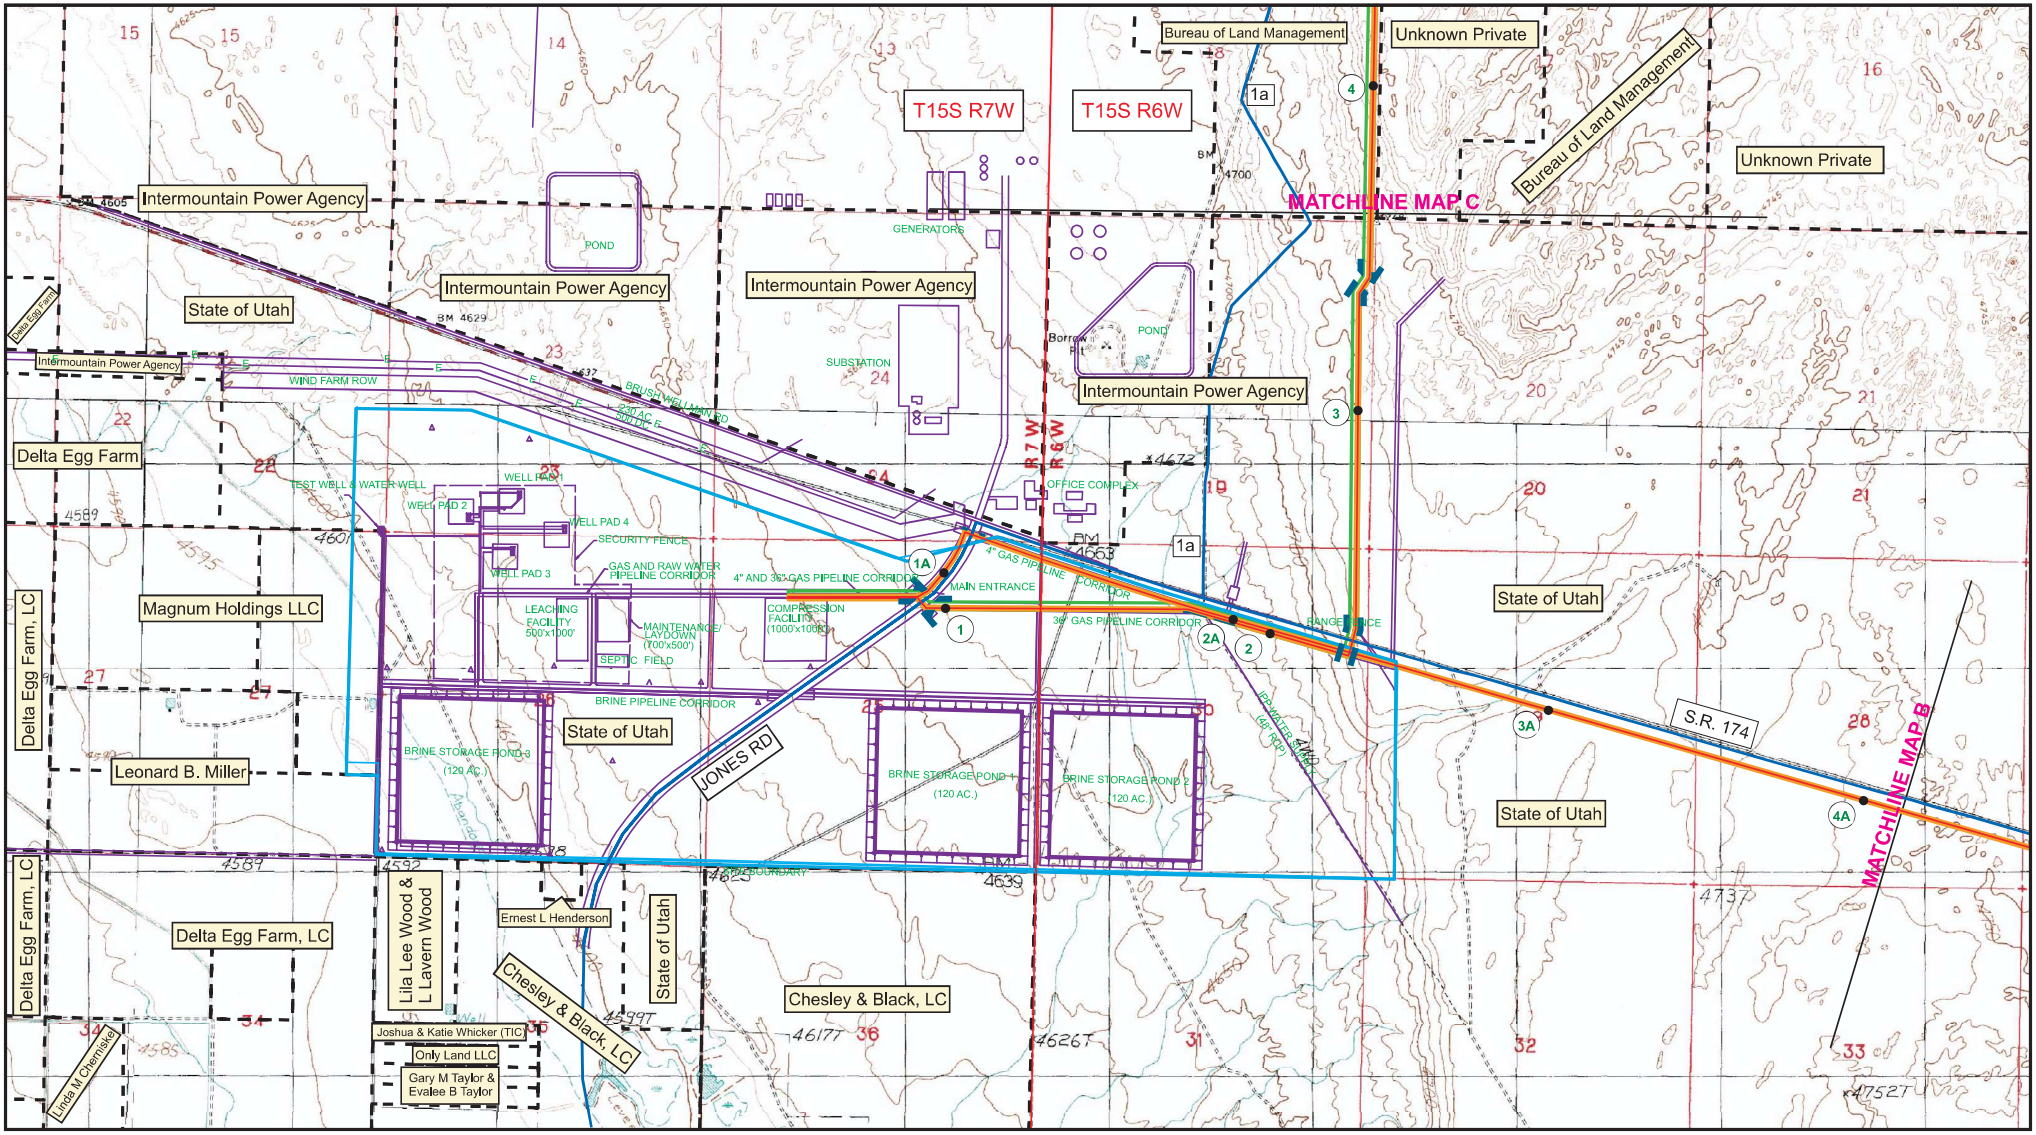


Storage Area
Permanent Right-of-way
Temporary Right-of-way
Additional Temporary Work Space
Land Ownership

Proposed Pipeline Centerline
Access Road
Storage Site Facilities Plan
Milepost

USGS 7.5' Quadrangles

Map A

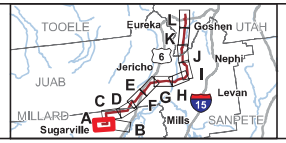

MAGNUM GAS STORAGE PROJECT

Proposed Storage Area, Pipeline Route, and Access Roads

ENTRIX
807 East South Temple, Suite 350
Salt Lake City, UT 84102
ph (801) 363-0116
fx (801) 363-0135
www.entrix.com


Coordinate System:
NAD 1983 UTM Zone 12N meter

N

0 1,000 2,000 4,000 Feet

1 inch = 2,000 feet 1:24,000

File: Entrix\Tetratech Magnum Pipeline Maps\Temp Work Space.mxd

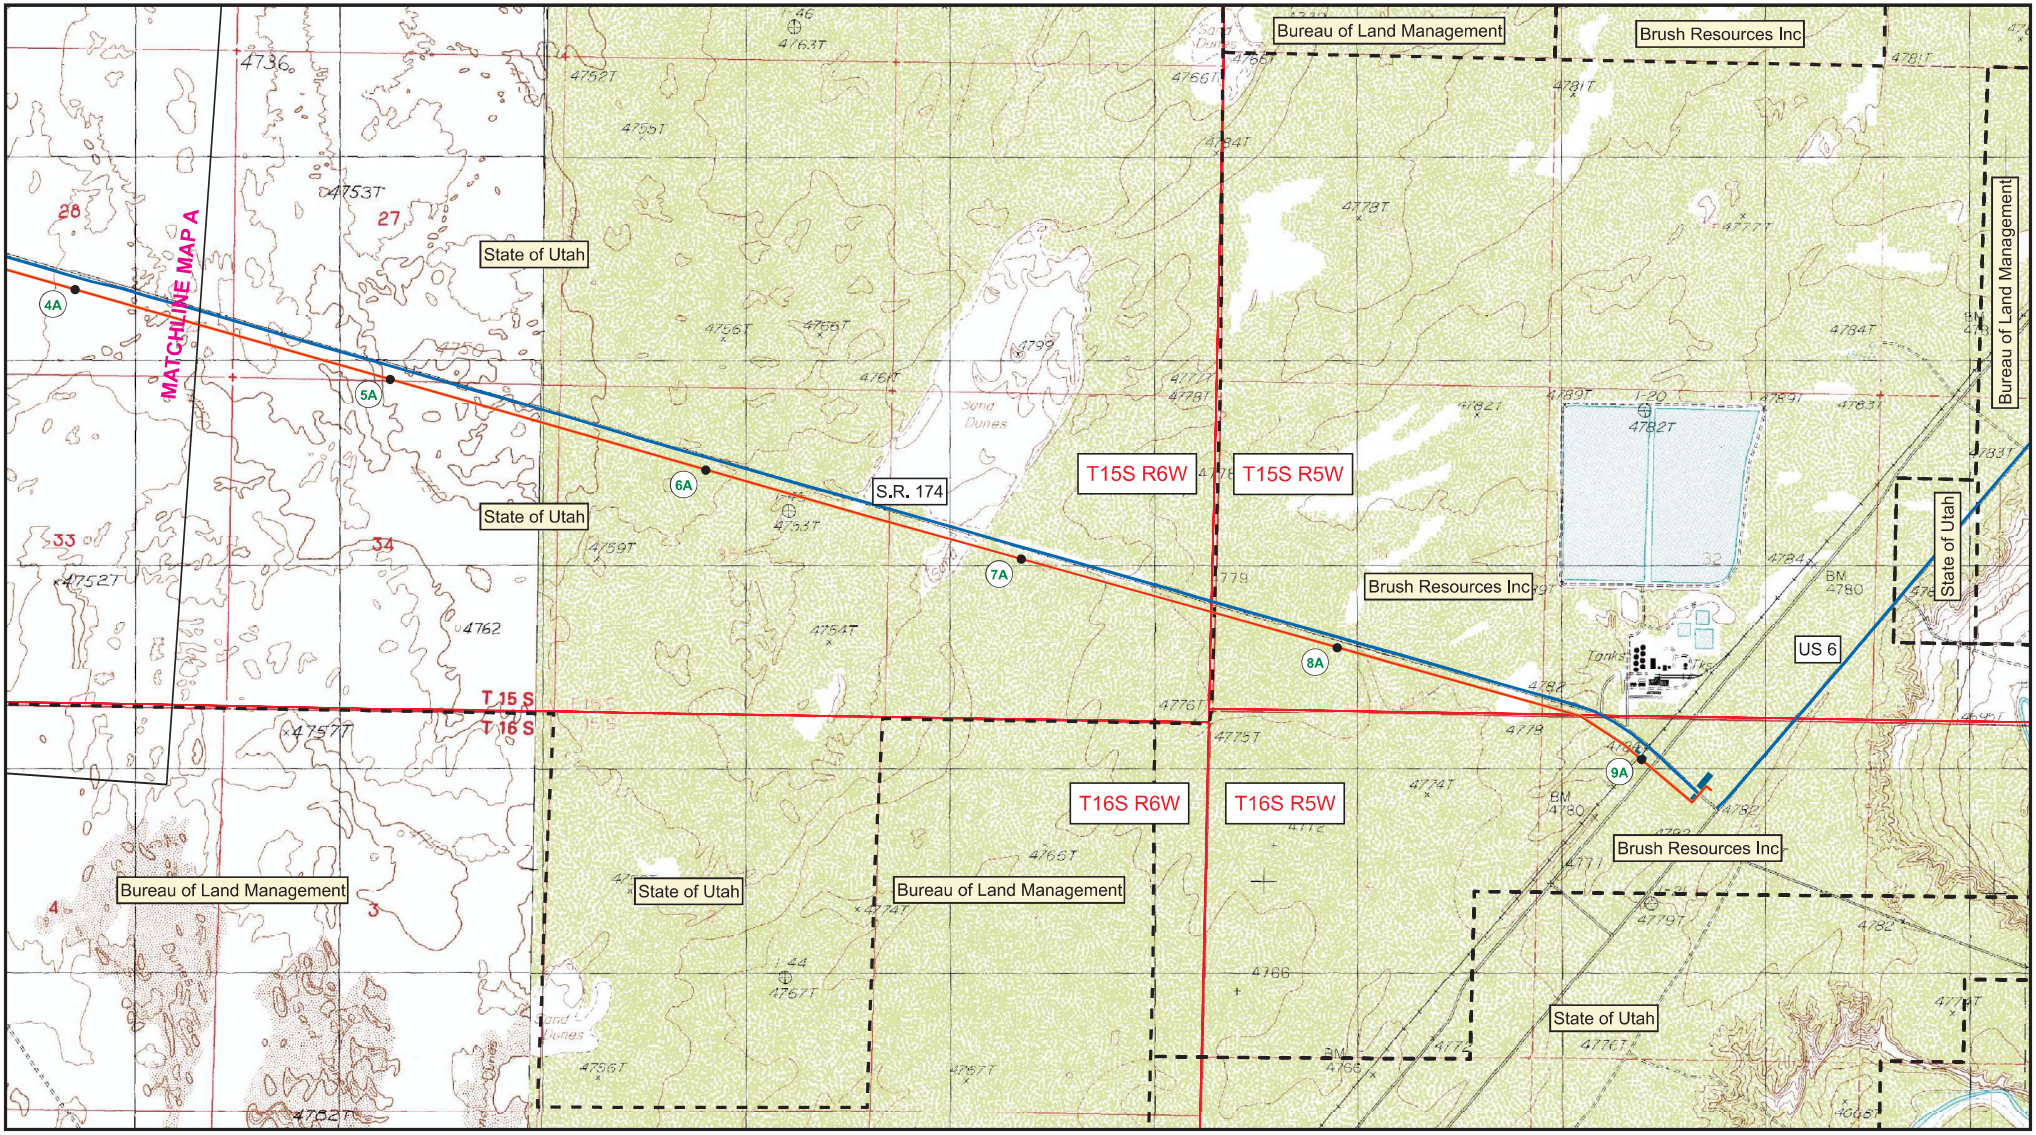


Storage Area
Permanent Right-of-way
Temporary Right-of-way
Additional Temporary Work Space
Land Ownership

Proposed Pipeline Centerline
Access Road
Storage Site Facilities Plan
Milepost

USGS 7.5' Quadrangles

Map B

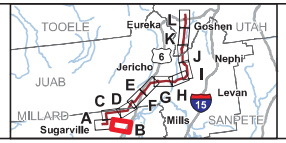

MAGNUM GAS STORAGE PROJECT

Proposed Storage Area, Pipeline Route, and Access Roads

ENTRIX
807 East South Temple, Suite 350
Salt Lake City, UT 84102
ph (801) 363-0116
fx (801) 363-0135
www.entrix.com


Coordinate System:
NAD 1983 UTM Zone 12N meter

N

0 1,000 2,000 4,000 Feet

1 inch = 2,000 feet 1:24,000


File: Entrix\Tetratech Magnum Pipeline Maps\Temp Work Space.mxd

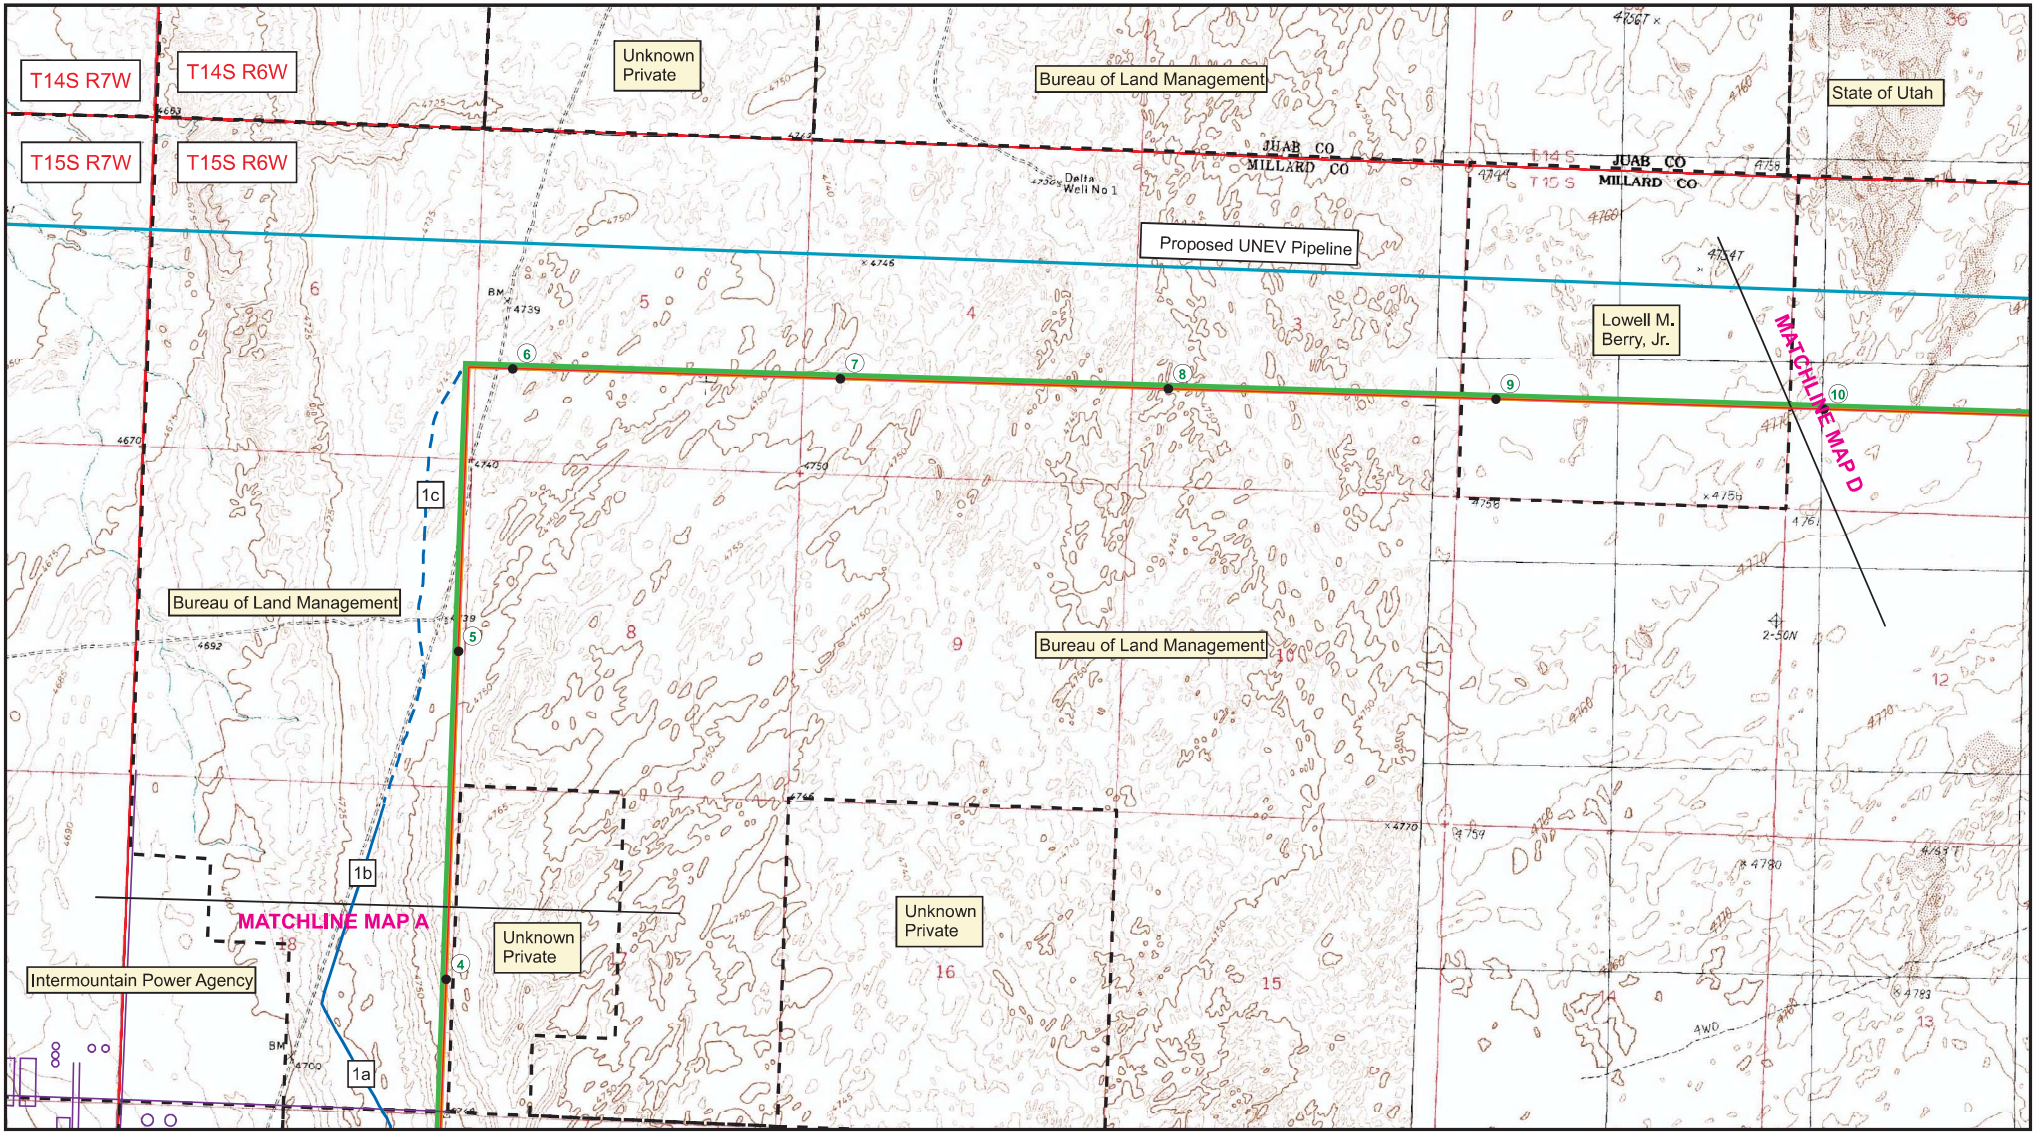

Storage Area
Permanent Right-of-way
Temporary Right-of-way
Additional Temporary Work Space
Land Ownership
Proposed Pipeline Centerline
Access Road
Access Road To Be Improved
Storage Site Facilities Plan
Milepost

USGS 7.5' Quadrangles

Map C

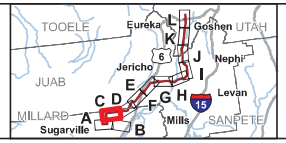

MAGNUM GAS STORAGE PROJECT

Proposed Storage Area, Pipeline Route, and Access Roads

ENTRIX
807 East South Temple, Suite 350
Salt Lake City, UT 84102
ph (801) 363-0116
fx (801) 363-0135
www.entrix.com


Coordinate System:
NAD 1983 UTM Zone 12N meter

N

0 1,000 2,000 4,000 Feet

1 inch = 2,000 feet 1:24,000

File: Entrix\Tetratech Magnum Pipeline Maps\Temp Work Space.mxd

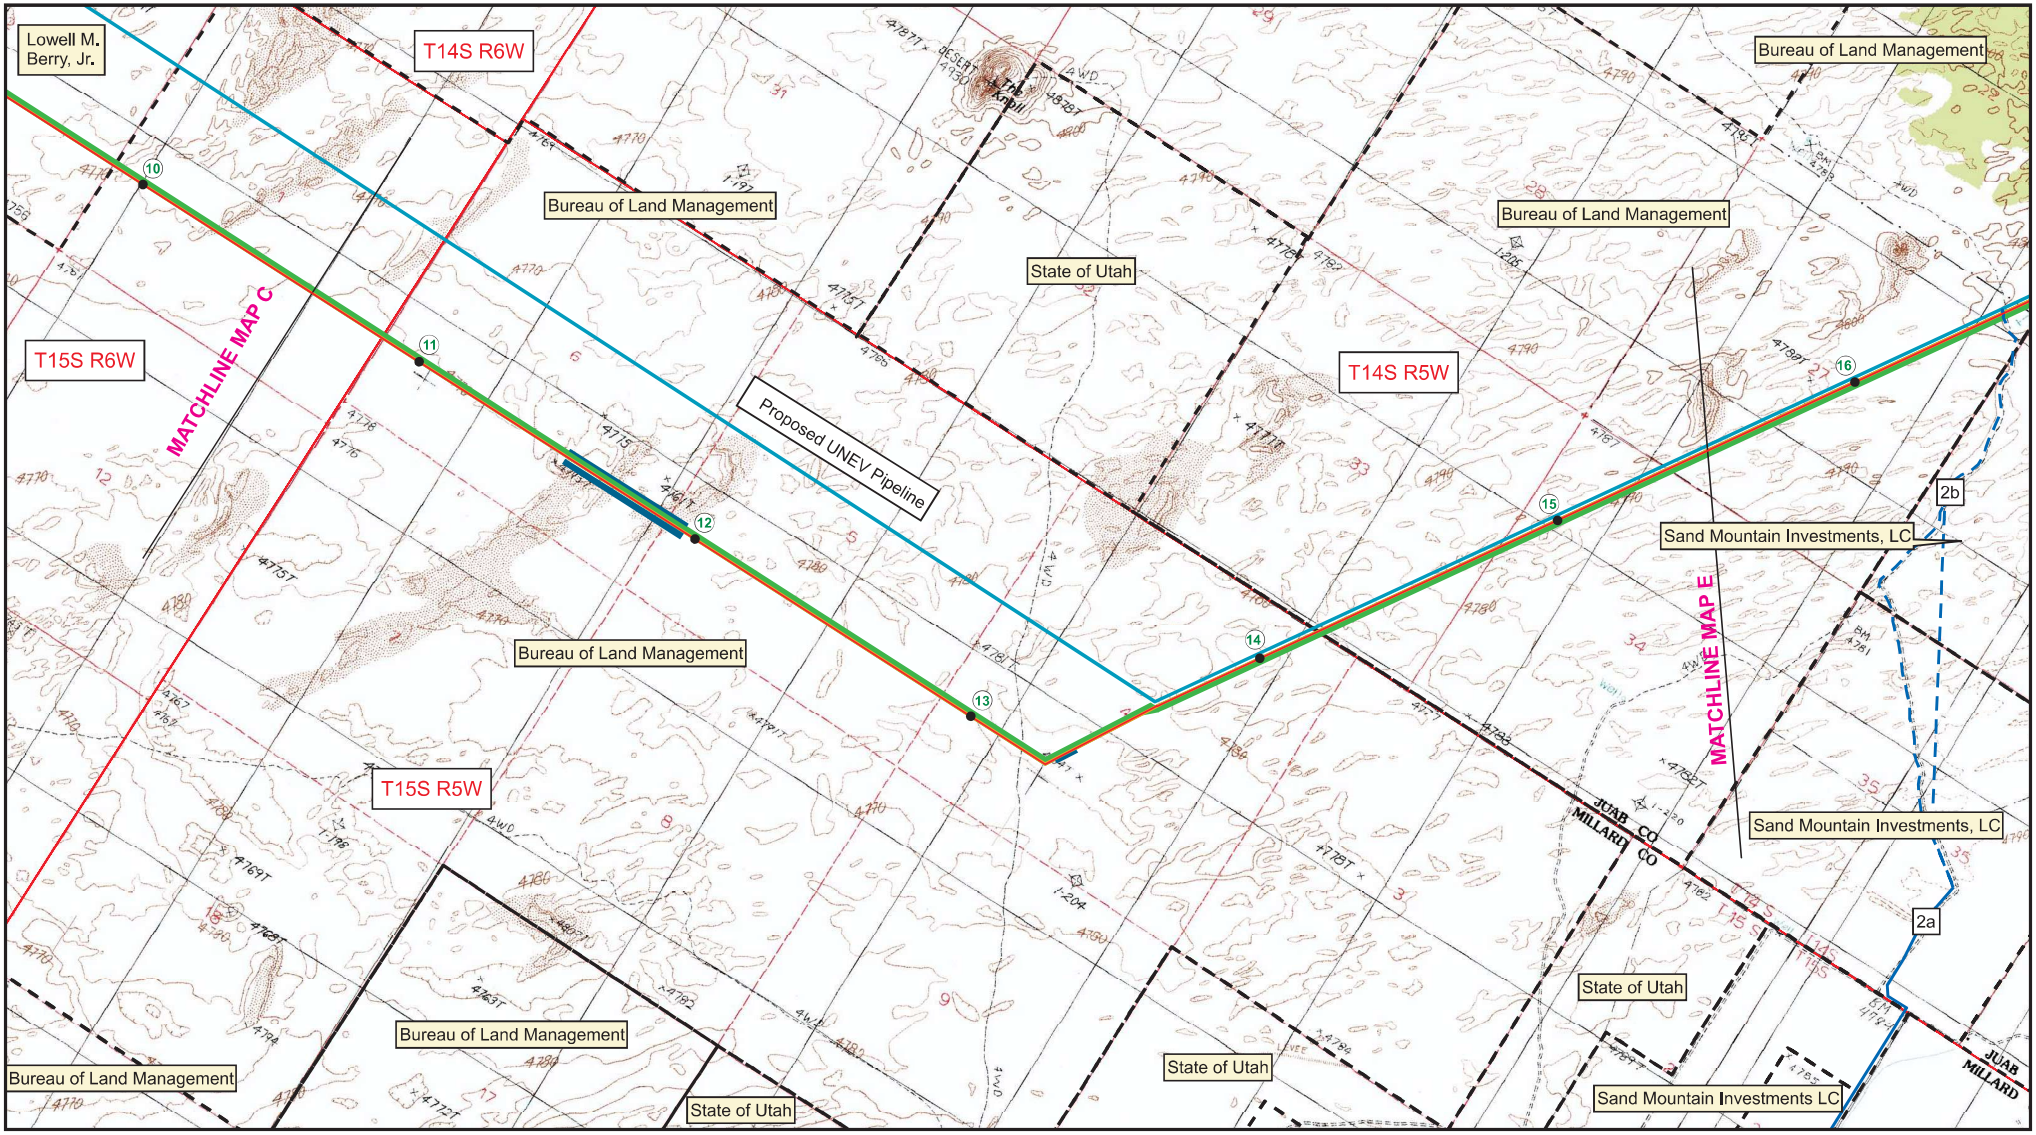


Storage Area
Permanent Right-of-way
Temporary Right-of-way
Additional Temporary Work Space
Land Ownership

Proposed Pipeline Centerline
Access Road
Access Road To Be Improved
Storage Site Facilities Plan
Milepost

USGS 7.5' Quadrangles

Map D

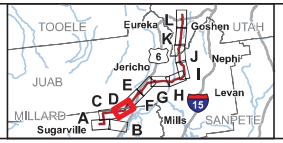

MAGNUM GAS STORAGE PROJECT

Proposed Storage Area, Pipeline Route, and Access Roads

ENTRIX
807 East South Temple, Suite 350
Salt Lake City, UT 84102
ph (801) 363-0116
fx (801) 363-0135
www.entrix.com


Coordinate System:
NAD 1983 UTM Zone 12N meter

N

0 1,000 2,000 4,000 Feet

1 inch = 2,000 feet 1:24,000


File: Entrix\Tetratech Magnum Pipeline Maps\Temp Work Space.mxd

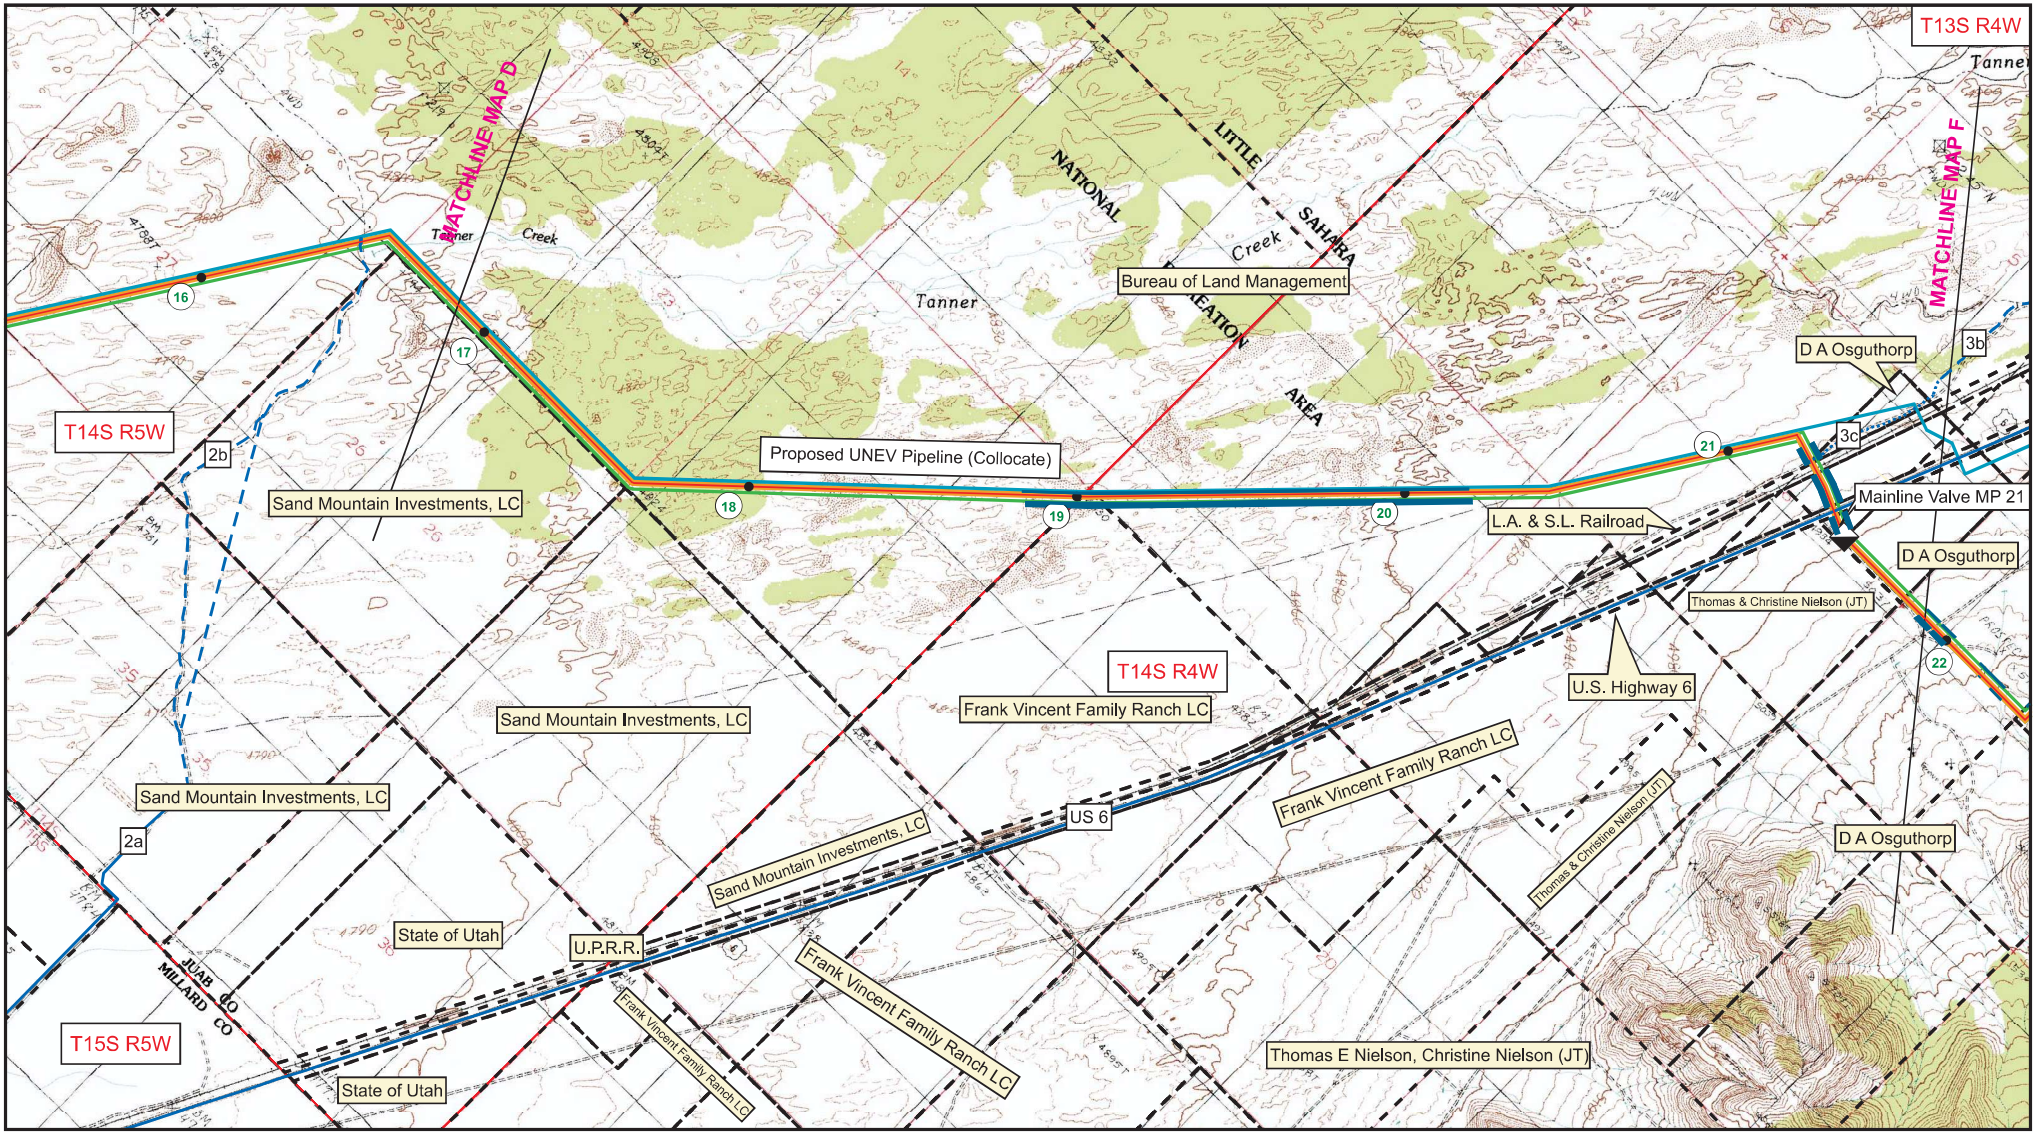

Storage Area
Permanent Right-of-way
Temporary Right-of-way
Additional Temporary Work Space
Land Ownership
Proposed Pipeline Centerline
Access Road
Improved
New
Storage Site Facilities Plan
Milepost

USGS 7.5' Quadrangles

Map E

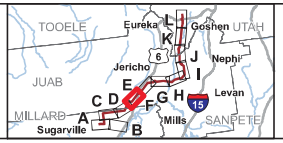

MAGNUM GAS STORAGE PROJECT

Proposed Storage Area, Pipeline Route, and Access Roads


ENTRIX
807 East South Temple, Suite 350
Salt Lake City, UT 84102
ph (801) 363-0116
fx (801) 363-0135
www.entrix.com

Coordinate System:
NAD 1983 UTM Zone 12N meter

0 1,000 2,000 4,000 Feet

1 inch = 2,000 feet 1:24,000


File: Entrix\Tetratech Magnum Pipeline Maps\Temp Work Space.mxd

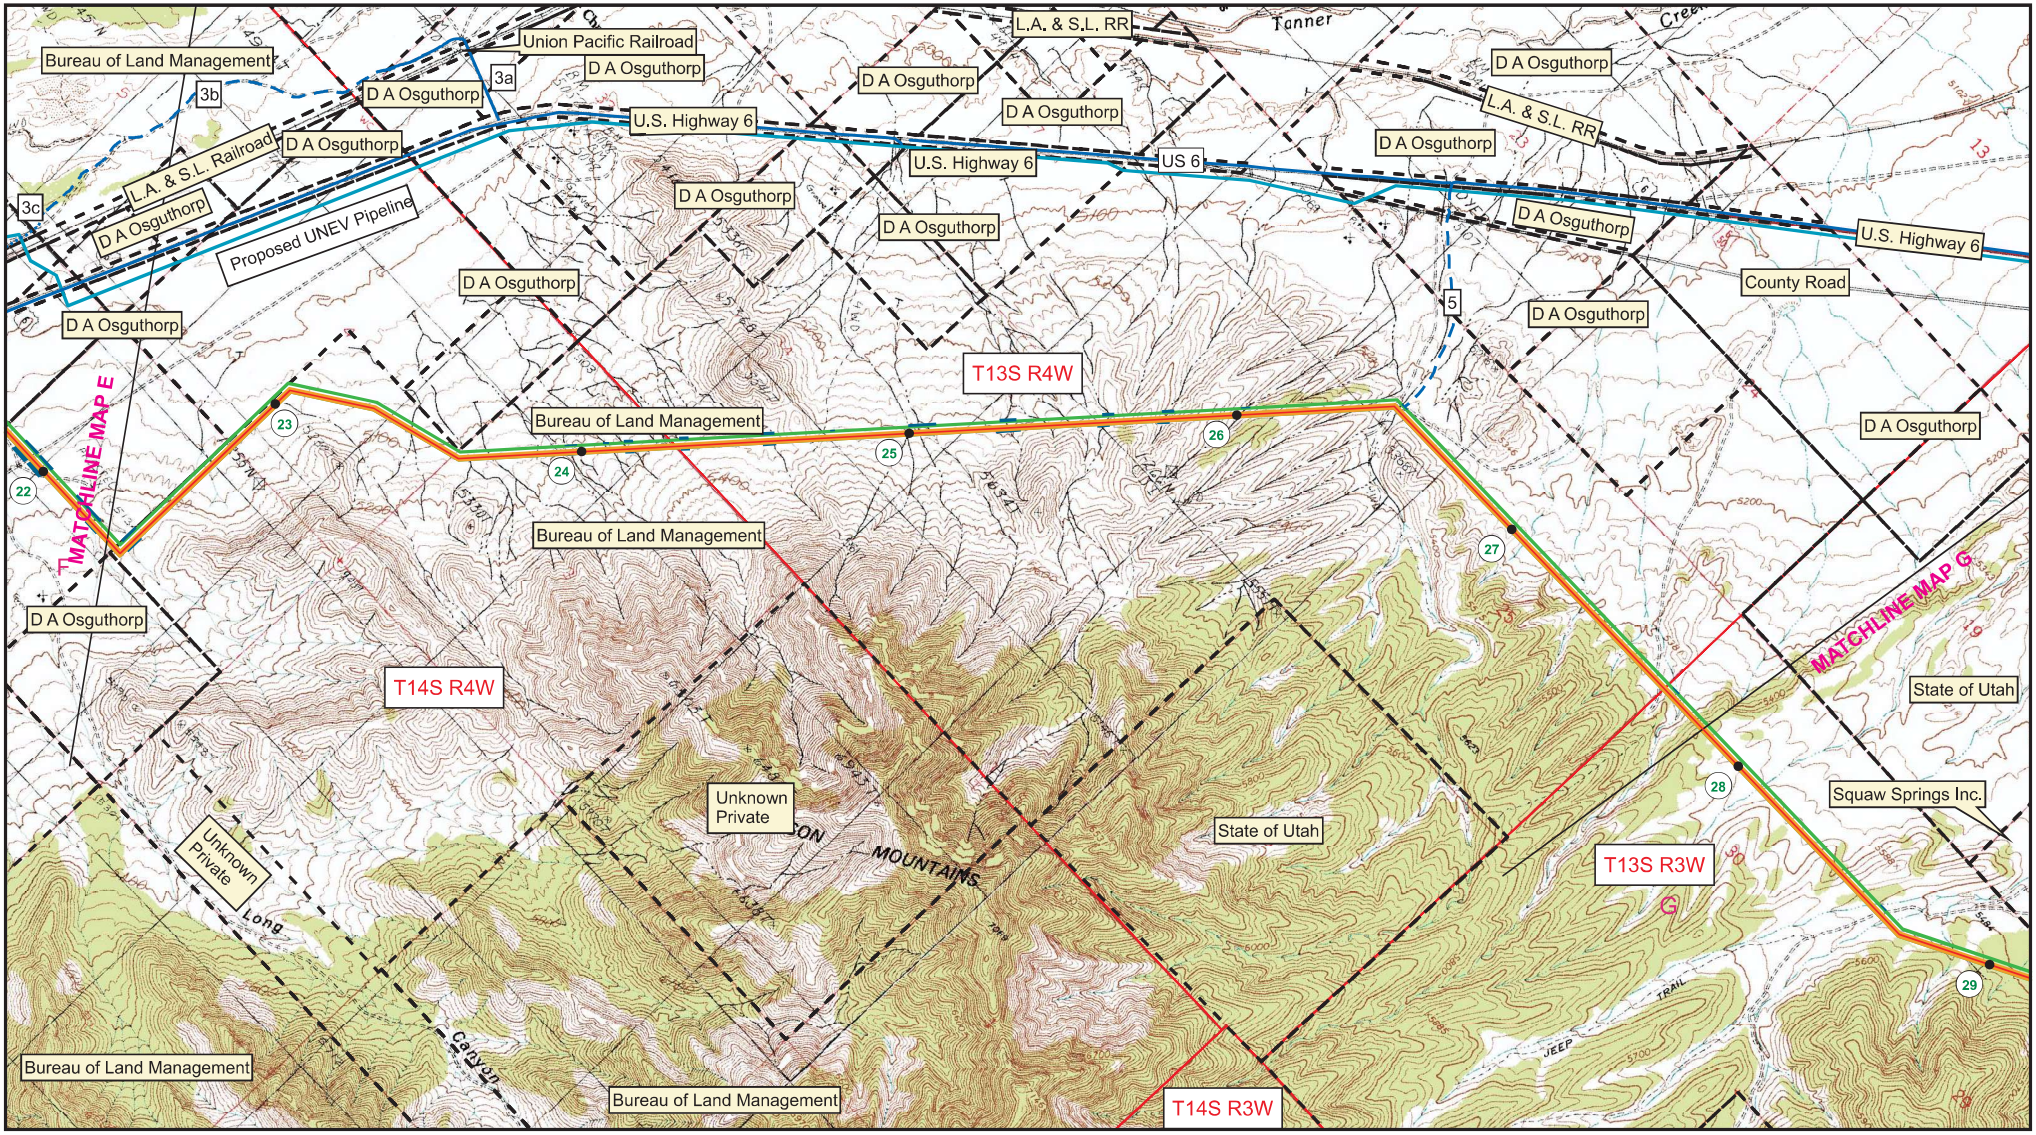

Storage Area	Proposed Pipeline Centerline
Permanent Right-of-way	Access Road
Temporary Right-of-way	Improved ····· New
Additional Temporary Work Space	Storage Site Facilities Plan
Land Ownership	Milepost

USGS 7.5' Quadrangles

Map F

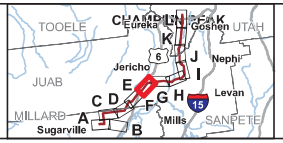

MAGNUM GAS STORAGE PROJECT

Proposed Storage Area, Pipeline Route, and Access Roads


ENTRIX
807 East South Temple, Suite 350
Salt Lake City, UT 84102
ph (801) 363-0116
fx (801) 363-0135
www.entrix.com

Coordinate System:
NAD 1983 UTM Zone 12N meter

0 1,000 2,000 4,000 Feet

1 inch = 2,000 feet 1:24,000

File: Entrix\Tetratech Magnum Pipeline Maps\Temp Work Space.mxd

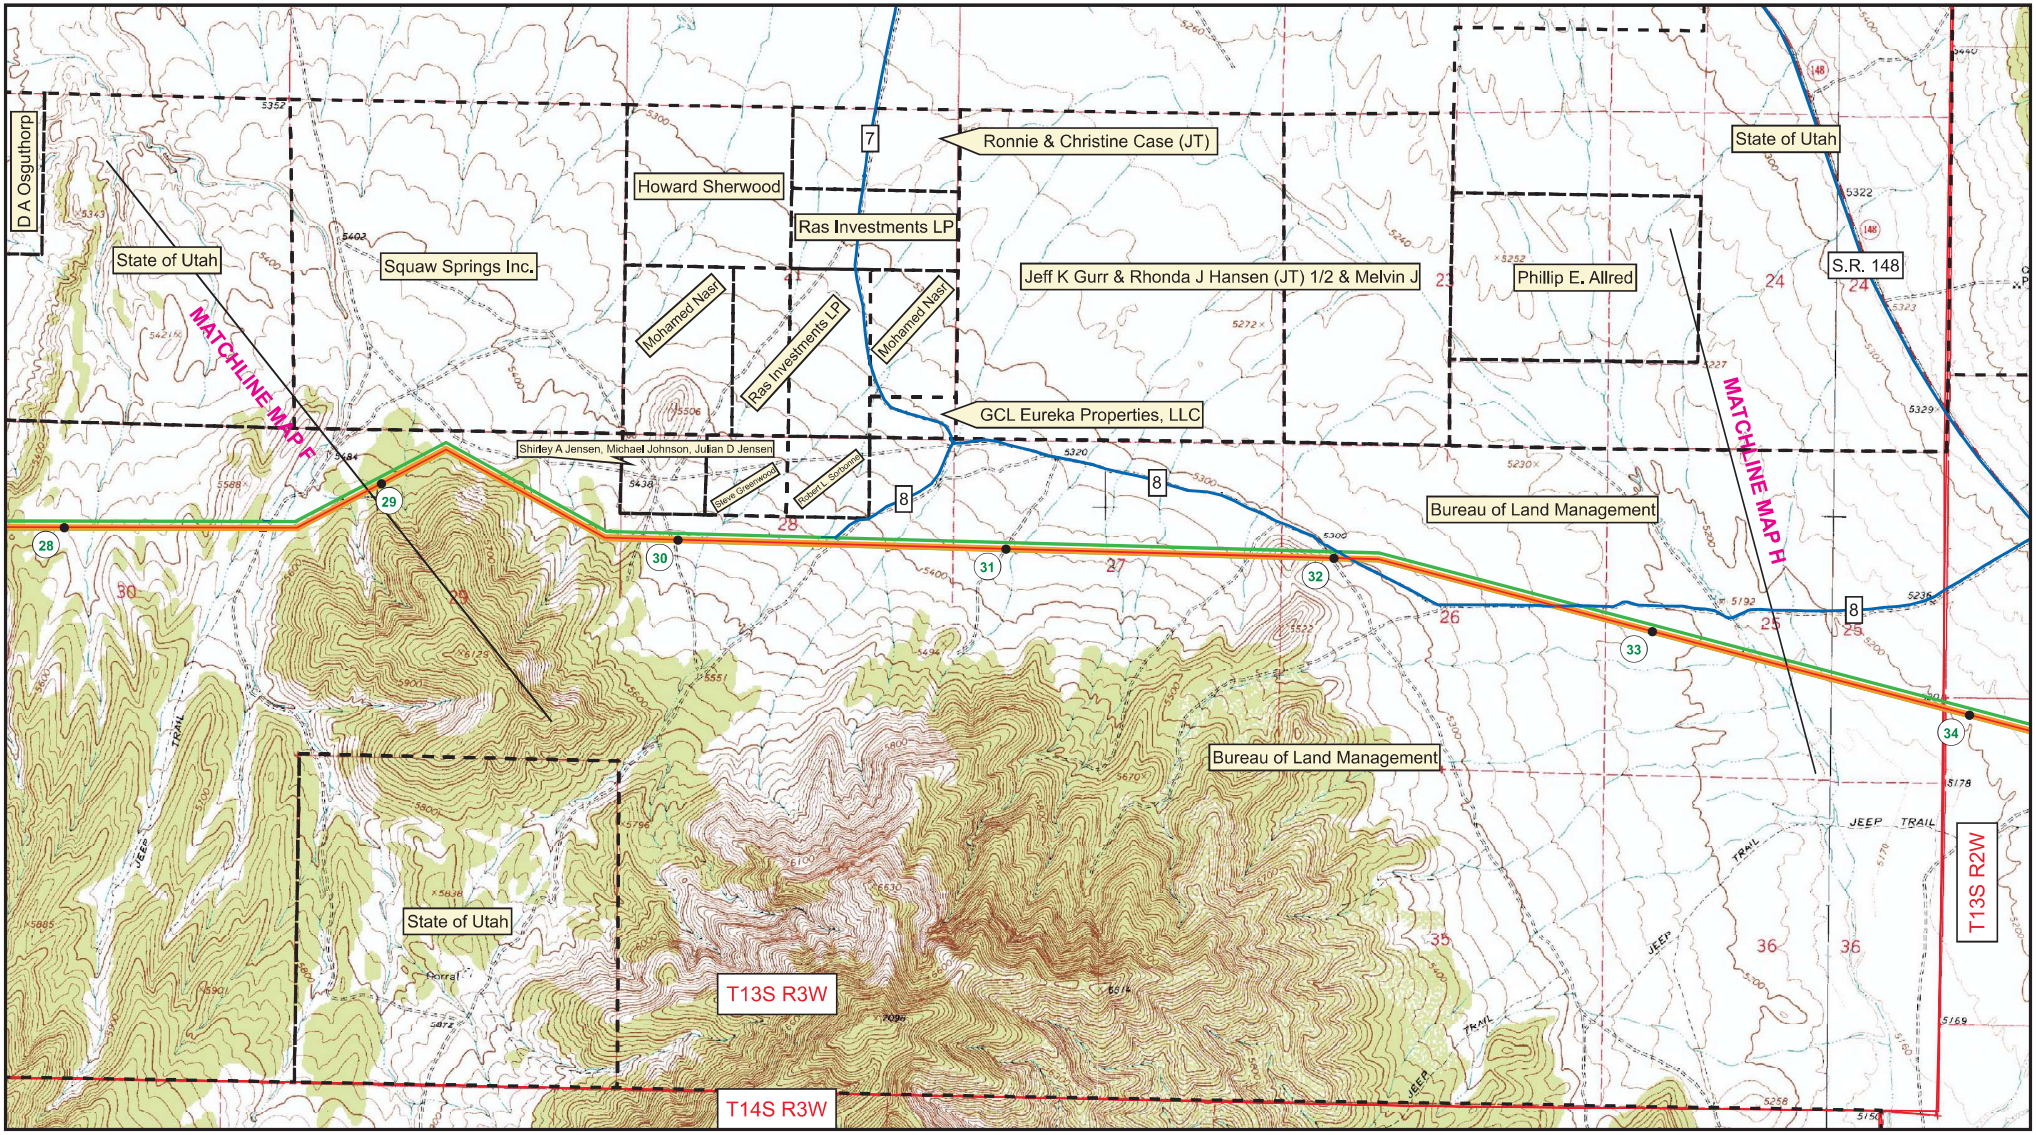


Storage Area
Permanent Right-of-way
Temporary Right-of-way
Additional Temporary Work Space
Land Ownership

Proposed Pipeline Centerline
Access Road
Storage Site Facilities Plan
Milepost

USGS 7.5' Quadrangles

Map G

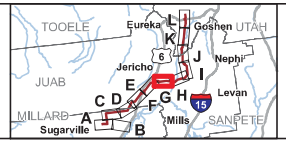

MAGNUM GAS STORAGE PROJECT

Proposed Storage Area, Pipeline Route, and Access Roads

ENTRIX
807 East South Temple, Suite 350
Salt Lake City, UT 84102
ph (801) 363-0116
fx (801) 363-0135
www.entrix.com


Coordinate System:
NAD 1983 UTM Zone 12N meter

N

0 1,000 2,000 4,000 Feet

1 inch = 2,000 feet 1:24,000

File: Entrix\Tetratech Magnum Pipeline Maps\Temp Work Space.mxd

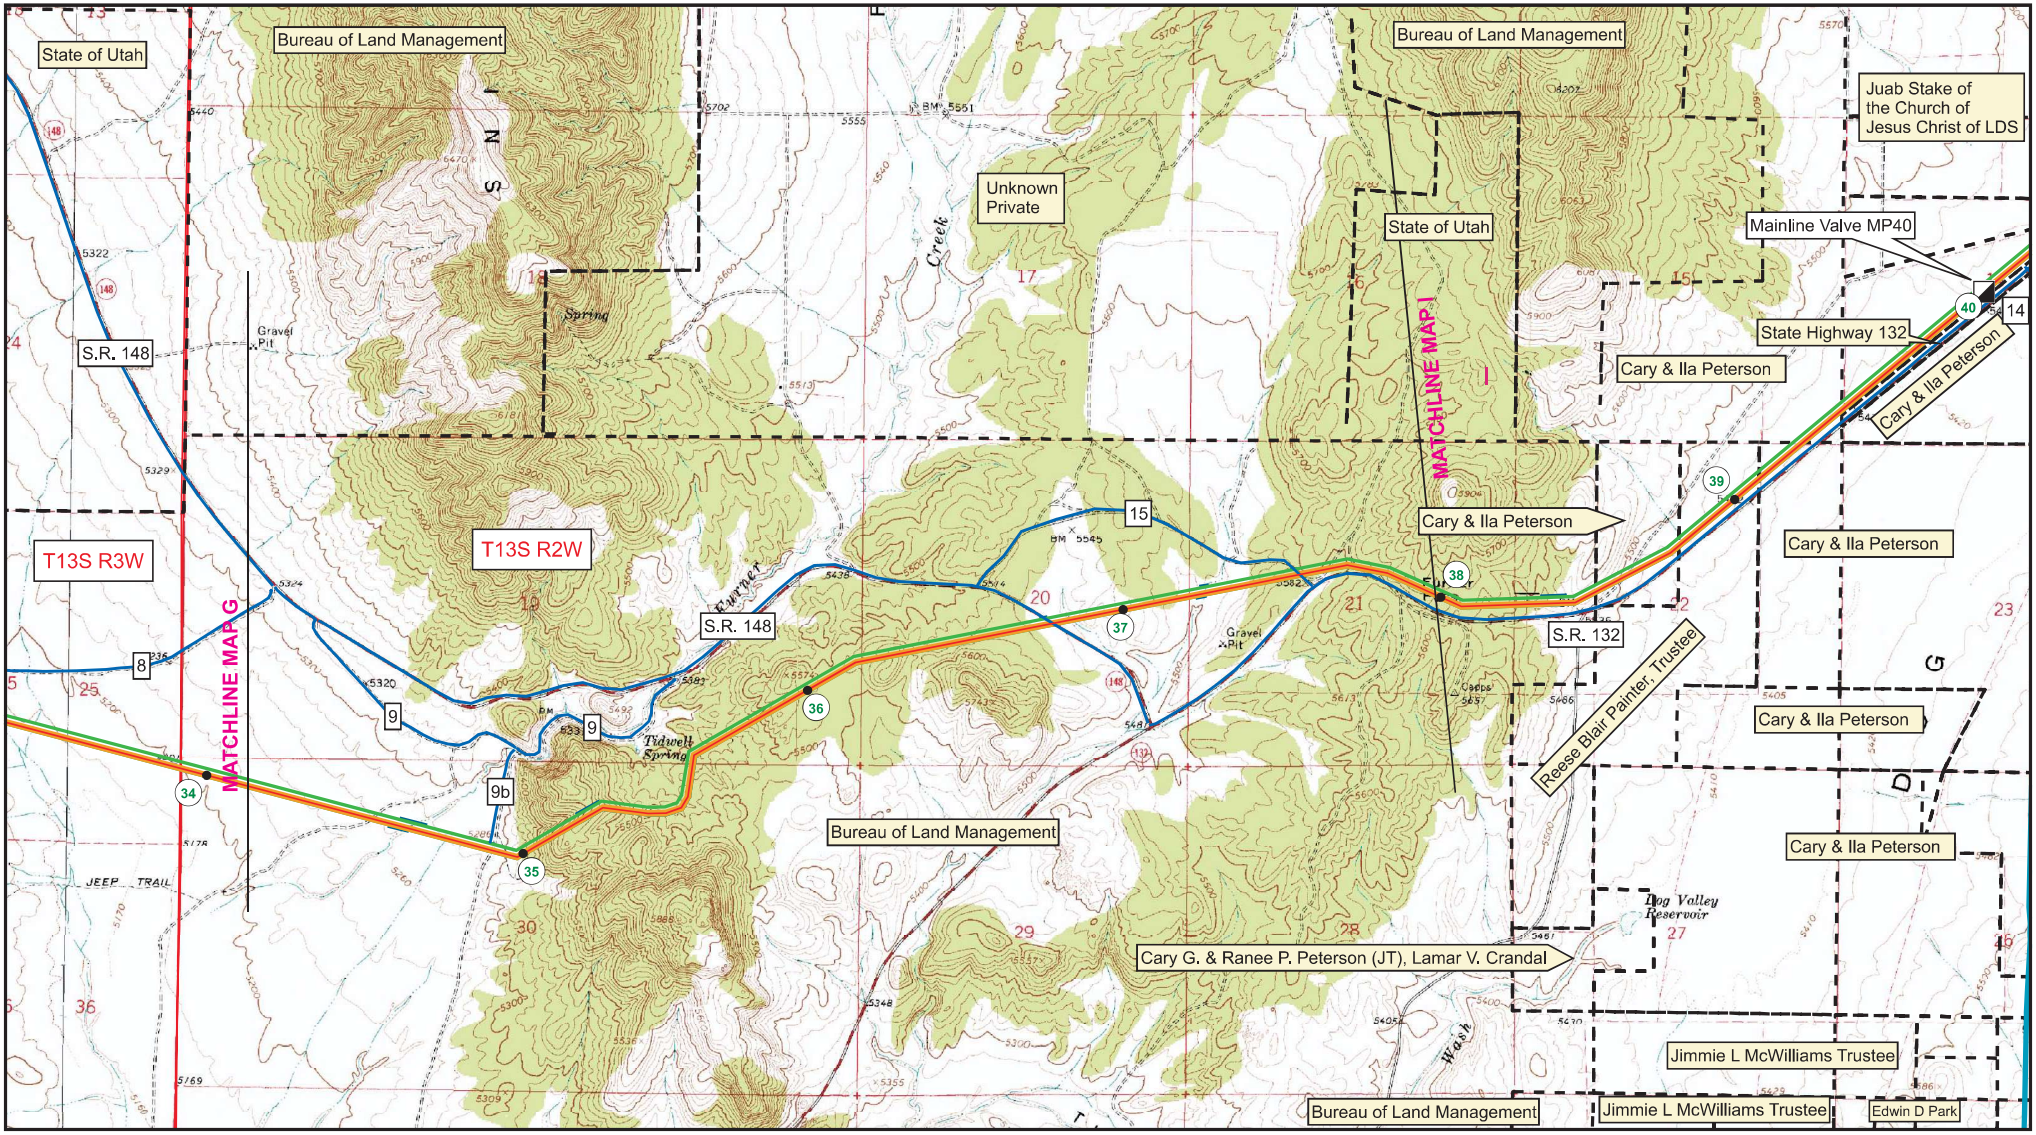


Storage Area
Permanent Right-of-way
Temporary Right-of-way
Additional Temporary Work Space
Land Ownership

Proposed Pipeline Centerline
Access Road
Storage Site Facilities Plan
Milepost

USGS 7.5' Quadrangles

Map H

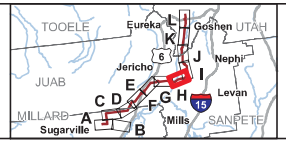

MAGNUM GAS STORAGE PROJECT

Proposed Storage Area, Pipeline Route, and Access Roads

ENTRIX
807 East South Temple, Suite 350
Salt Lake City, UT 84102
ph (801) 363-0116
fx (801) 363-0135
www.entrix.com


Coordinate System:
NAD 1983 UTM Zone 12N meter

N

0 1,000 2,000 4,000 Feet


1 inch = 2,000 feet 1:24,000

File: Entrix\Tetratech Magnum Pipeline Maps\Temp Work Space.mxd

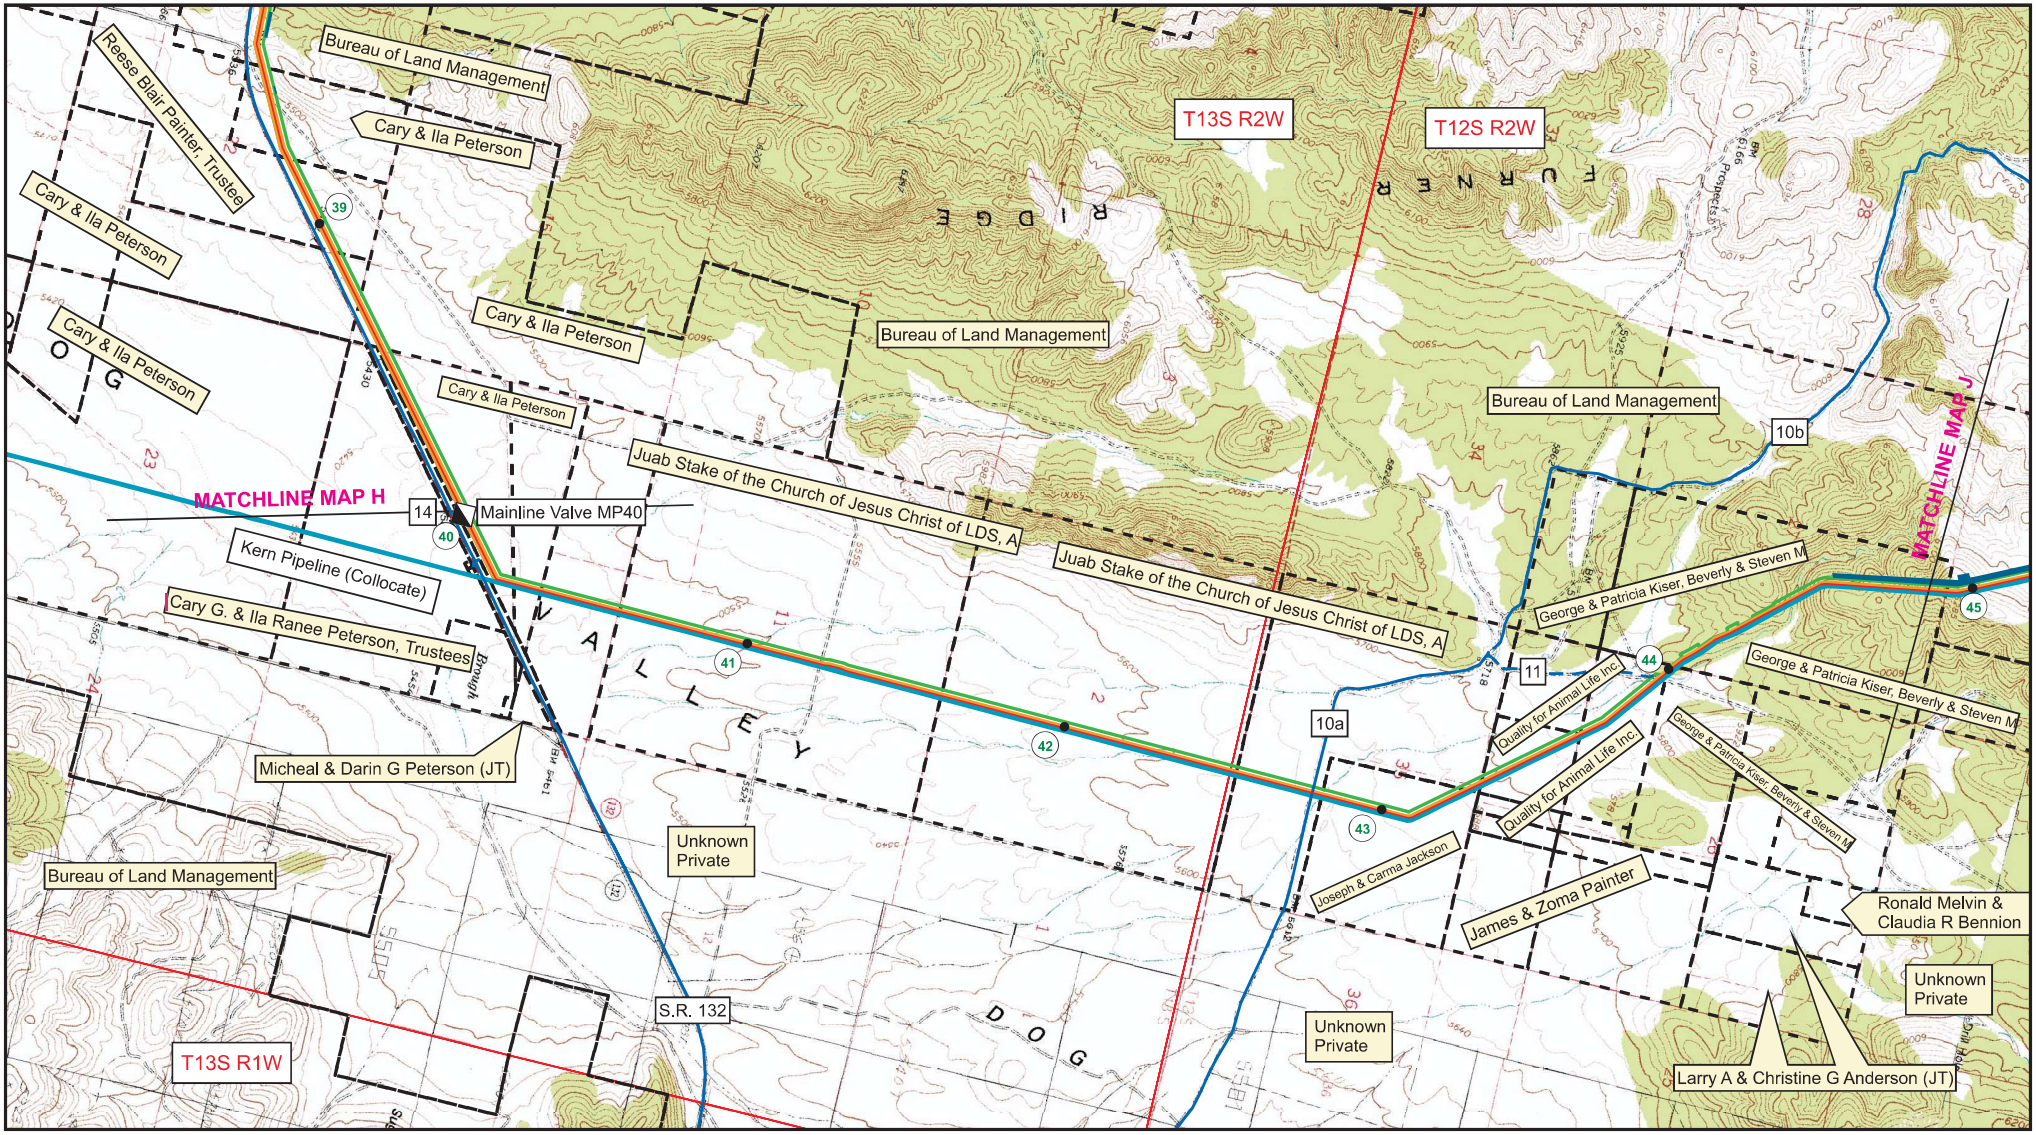

Storage Area
Permanent Right-of-way
Temporary Right-of-way
Additional Temporary Work Space
Land Ownership
Proposed Pipeline Centerline
Access Road
Access Road To Be Improved
Storage Site Facilities Plan
Milepost
USGS 7.5' Quadrangles

Map I

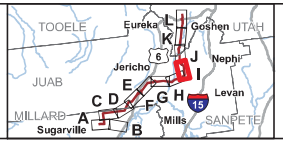

MAGNUM GAS STORAGE PROJECT

Proposed Storage Area, Pipeline Route, and Access Roads

ENTRIX
807 East South Temple, Suite 350
Salt Lake City, UT 84102
ph (801) 363-0116
fx (801) 363-0135
www.entrix.com


Coordinate System:
NAD 1983 UTM Zone 12N meter

N

0 1,000 2,000 4,000 Feet

1 inch = 2,000 feet 1:24,000


File: Entrix\Tetratech Magnum Pipeline Maps\Temp Work Space.mxd

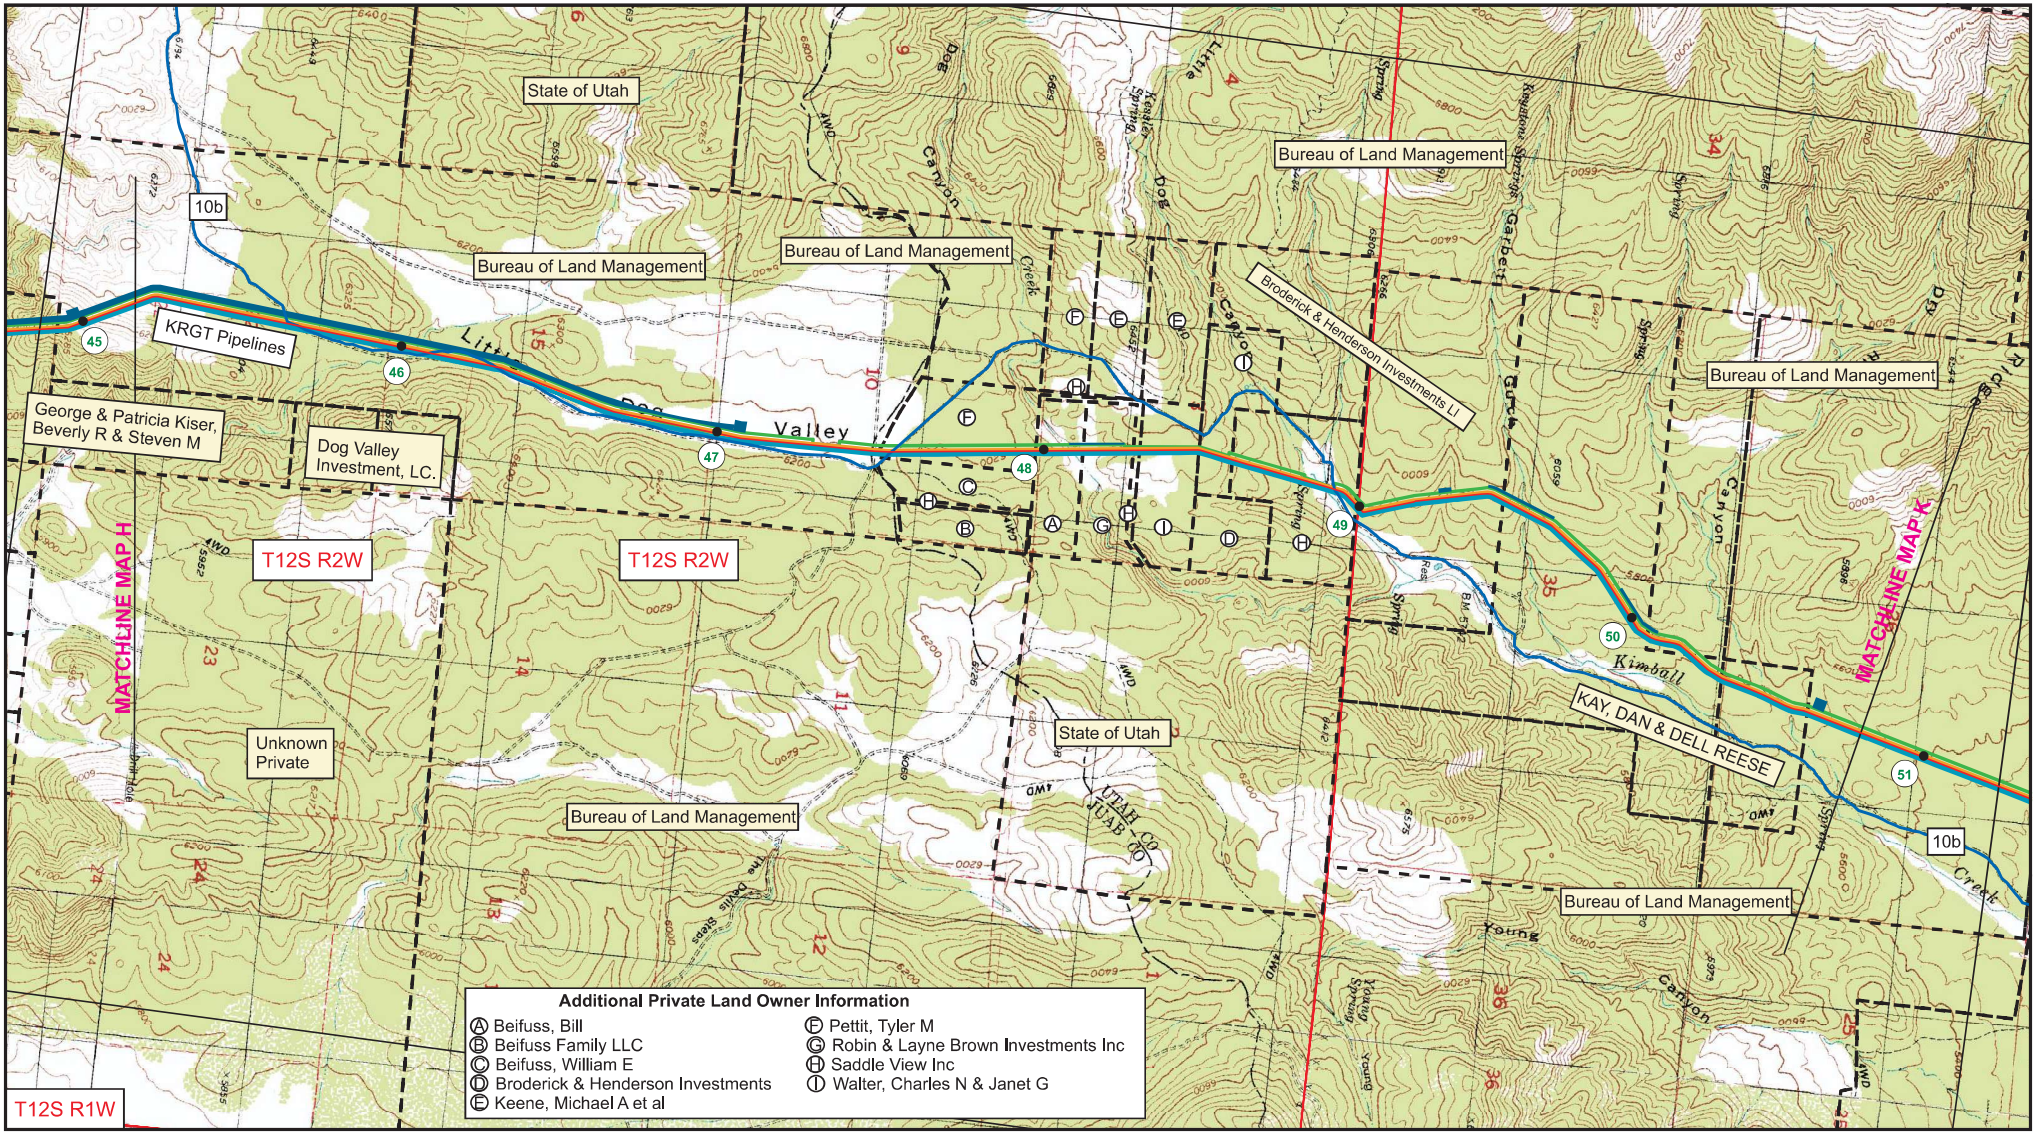

Storage Area
Permanent Right-of-way
Temporary Right-of-way
Additional Temporary Work Space
Land Ownership
Proposed Pipeline Centerline
Access Road
Storage Site Facilities Plan
Milepost

USGS 7.5' Quadrangles

Map J

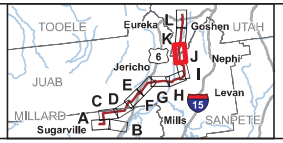

MAGNUM GAS STORAGE PROJECT

Proposed Storage Area, Pipeline Route, and Access Roads


ENTRIX
907 East South Temple, Suite 350
Salt Lake City, UT 84102
ph (801) 363-0116
fx (801) 363-0135
www.entrix.com

Coordinate System:
NAD 1983 UTM Zone 12N meter

0 1,000 2,000 4,000 Feet

1 inch = 2,000 feet 1:24,000


File: Entrix\Tetratech Magnum Pipeline Maps\Temp Work Space.mxd

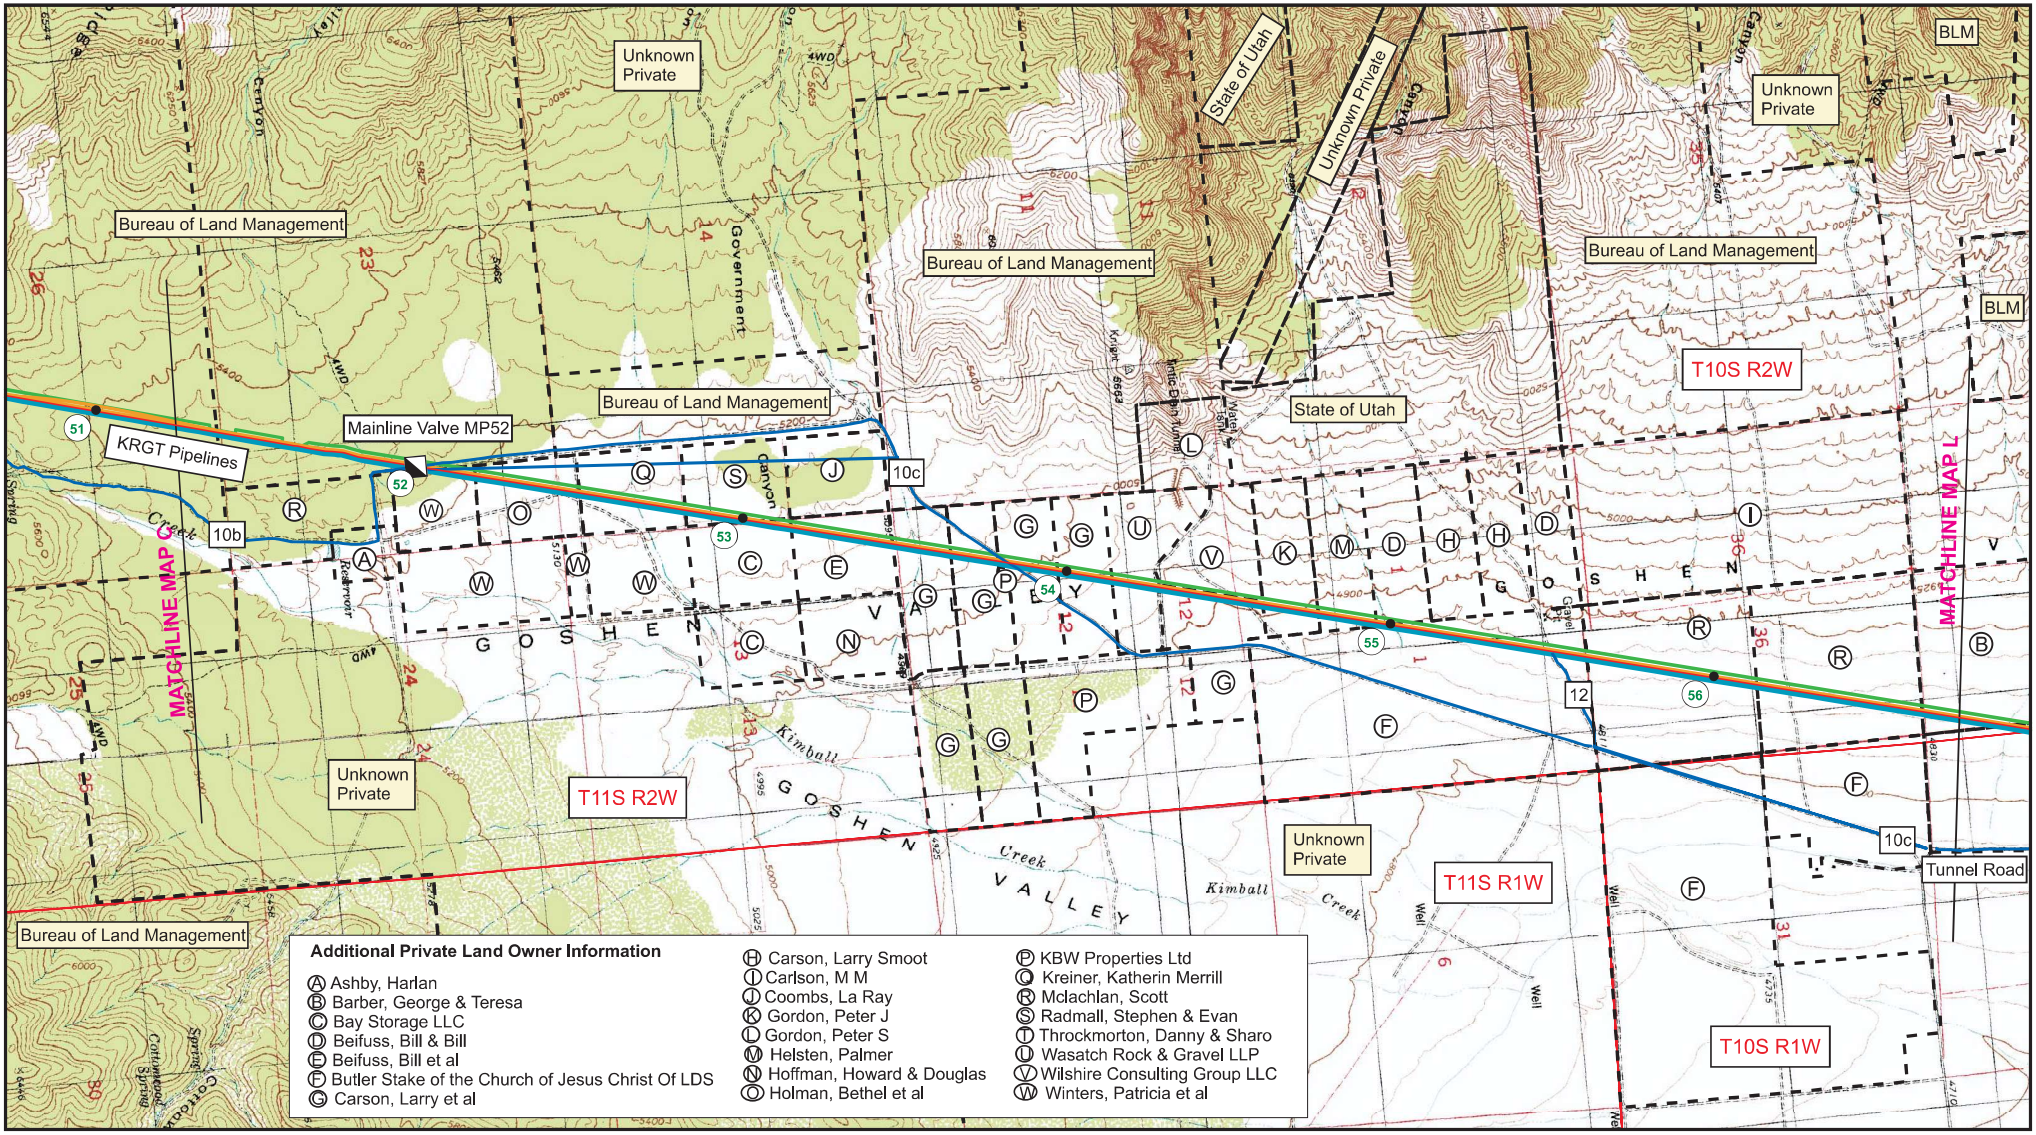

Storage Area
Permanent Right-of-way
Temporary Right-of-way
Additional Temporary Work Space
Land Ownership
Proposed Pipeline Centerline
Access Road
Storage Site Facilities Plan
Milepost

USGS 7.5' Quadrangles

Map K

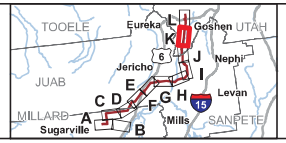

MAGNUM GAS STORAGE PROJECT

Proposed Storage Area, Pipeline Route, and Access Roads


ENTRIX
807 East South Temple, Suite 350
Salt Lake City, UT 84102
ph (801) 363-0116
fx (801) 363-0135
www.entrix.com

Coordinate System:
NAD 1983 UTM Zone 12N meter

0 1,000 2,000 4,000 Feet

1 inch = 2,000 feet 1:24,000


File: Entrix\Tetratech Magnum Pipeline Maps\Temp Work Space.mxd

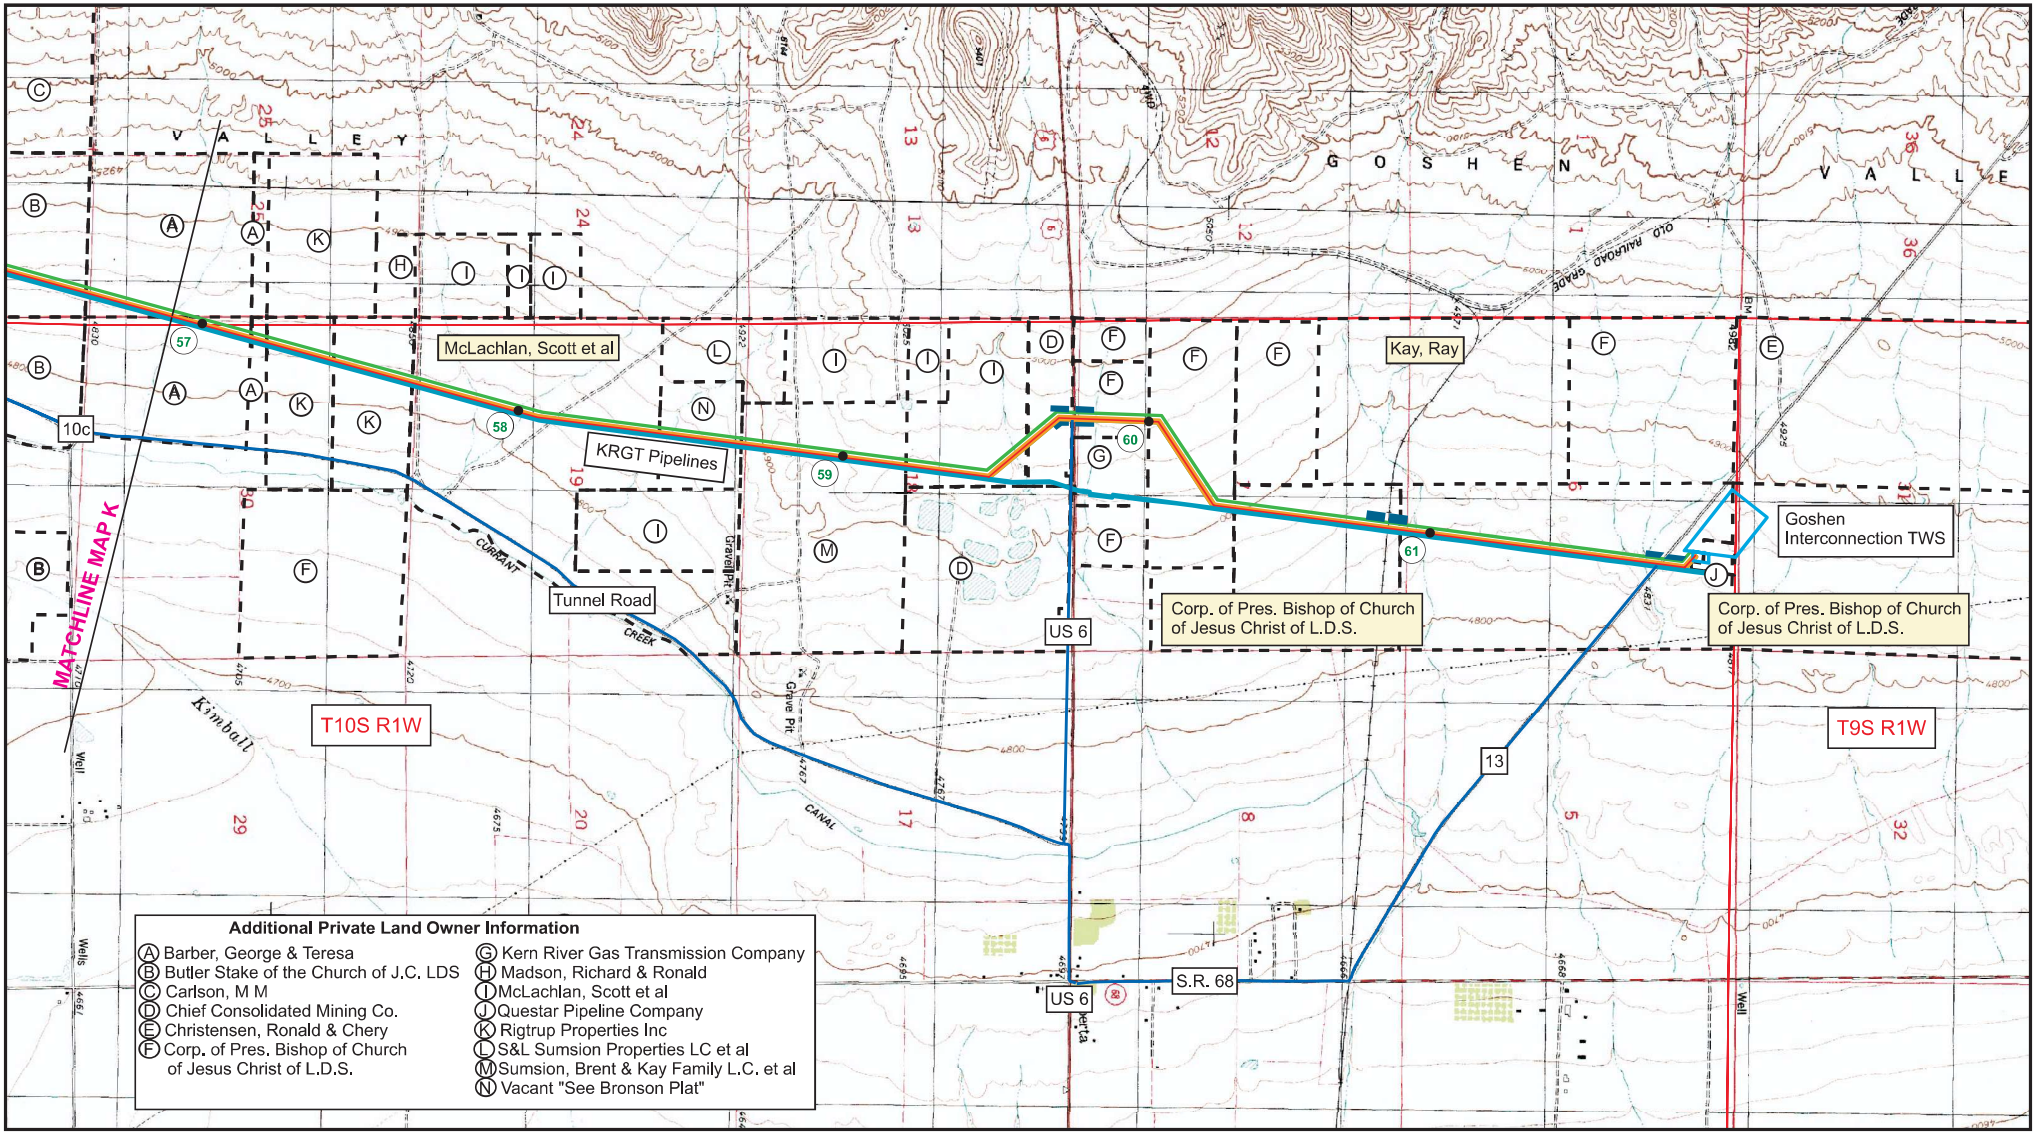

Storage Area
Permanent Right-of-way
Temporary Right-of-way
Additional Temporary Work Space
Land Ownership
Proposed Pipeline Centerline
Access Road
Storage Site Facilities Plan
Milepost

USGS 7.5' Quadrangles

Map L

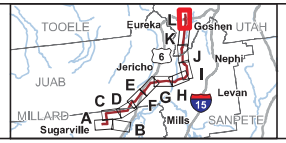

MAGNUM GAS STORAGE PROJECT


Proposed Storage Area, Pipeline Route, and Access Roads

ENTRIX
807 East South Temple, Suite 350
Salt Lake City, UT 84102
ph (801) 363-0116
fx (801) 363-0135
www.entrix.com

Coordinate System:
NAD 1983 UTM Zone 12N meter

N
0 1,000 2,000 4,000 Feet
1 inch = 2,000 feet 1:24,000


File: Entrix\Tetratech Magnum Pipeline Maps\Temp Work Space.mxd

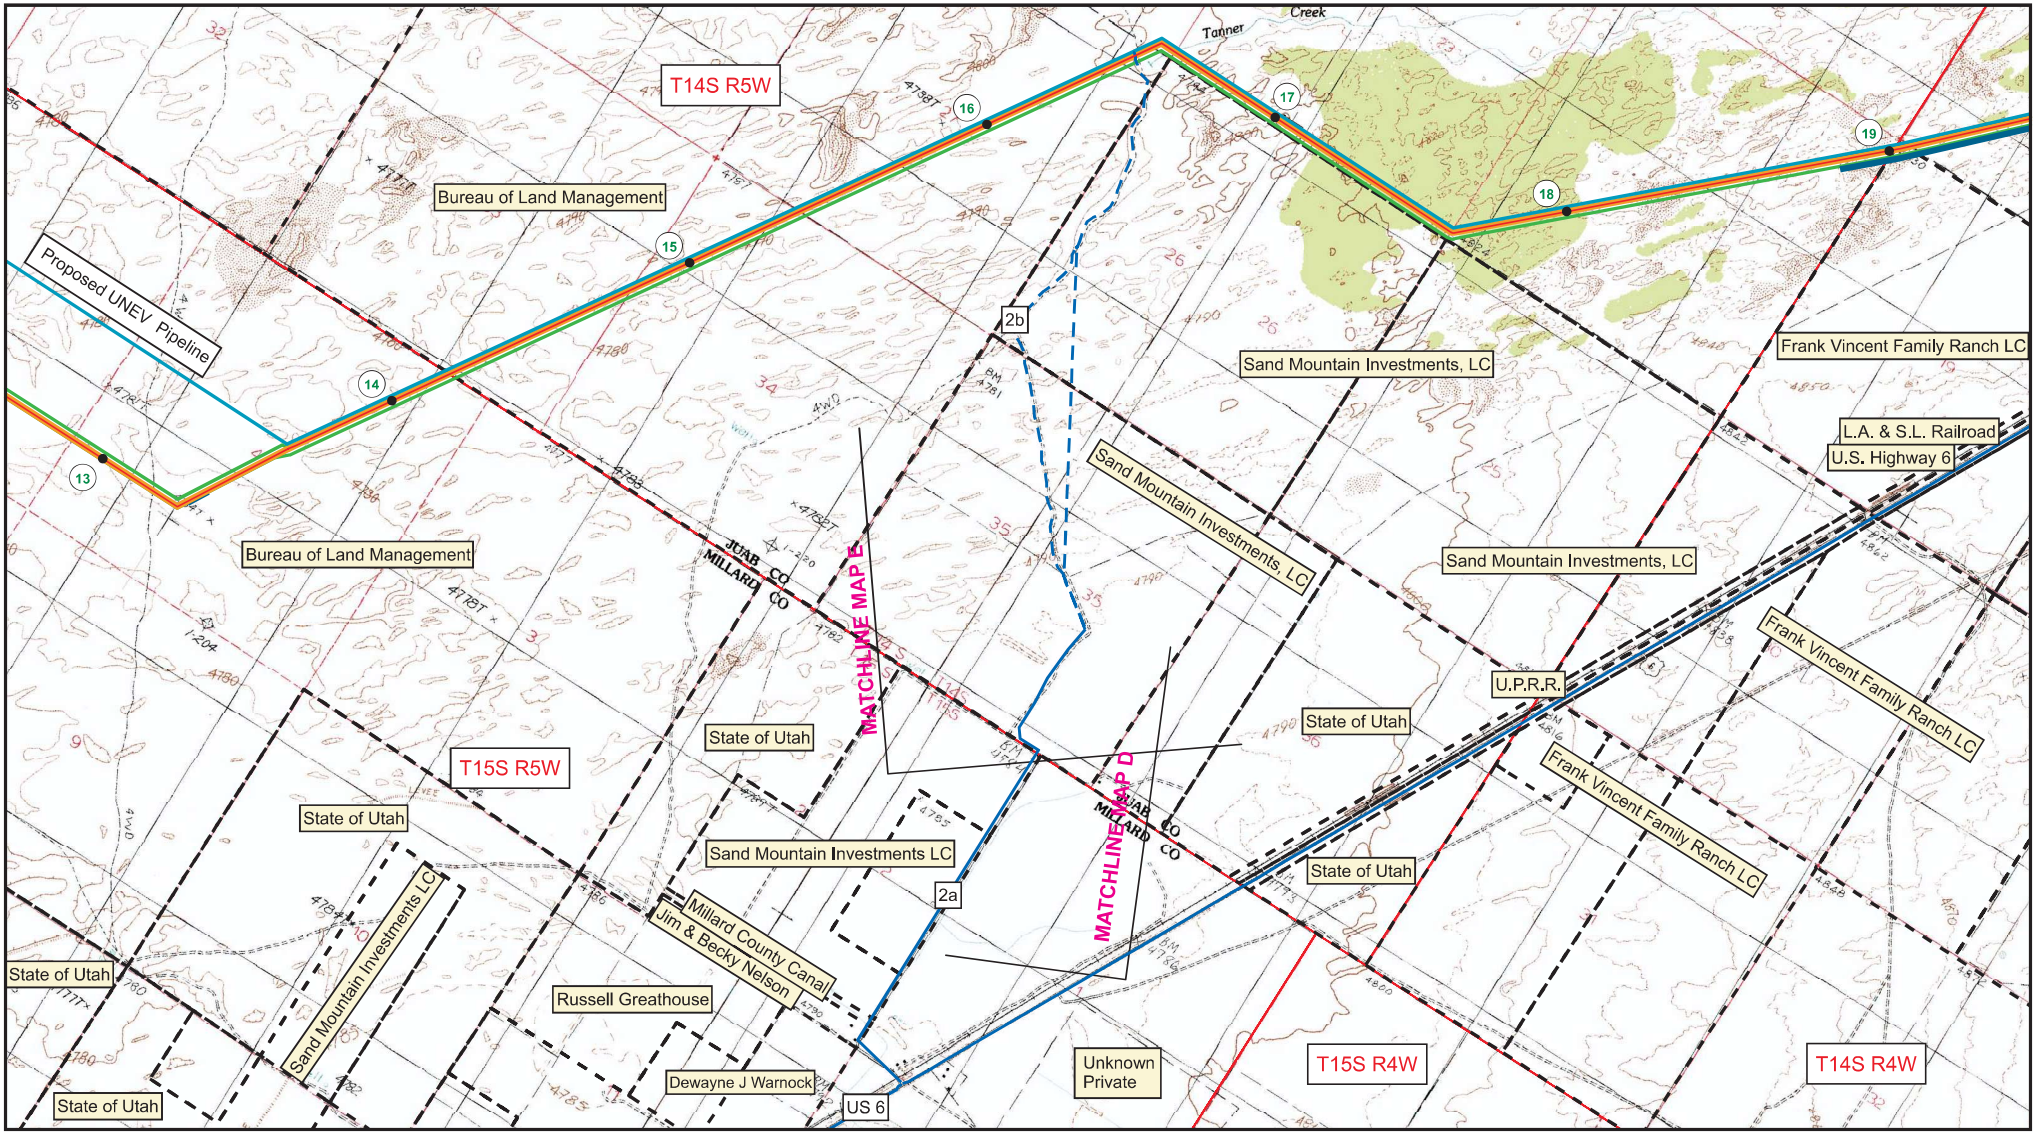

Storage Area
Permanent Right-of-way
Temporary Right-of-way
Additional Temporary Work Space
Land Ownership
Proposed Pipeline Centerline
Access Road
Access Road To Be Improved
Storage Site Facilities Plan
Milepost

USGS 7.5' Quadrangles

Map M

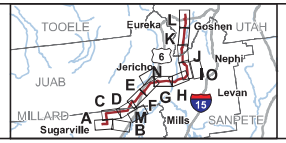

MAGNUM GAS STORAGE PROJECT

Proposed Storage Area, Pipeline Route, and Access Roads


ENTRIX
807 East South Temple, Suite 350
Salt Lake City, UT 84102
ph (801) 363-0116
fx (801) 363-0135
www.entrix.com

Coordinate System:
NAD 1983 UTM Zone 12N meter

0 1,000 2,000 4,000 Feet

1 inch = 2,000 feet 1:24,000


File: Entrix\Tetratech Magnum Pipeline Maps\Temp Work Space.mxd

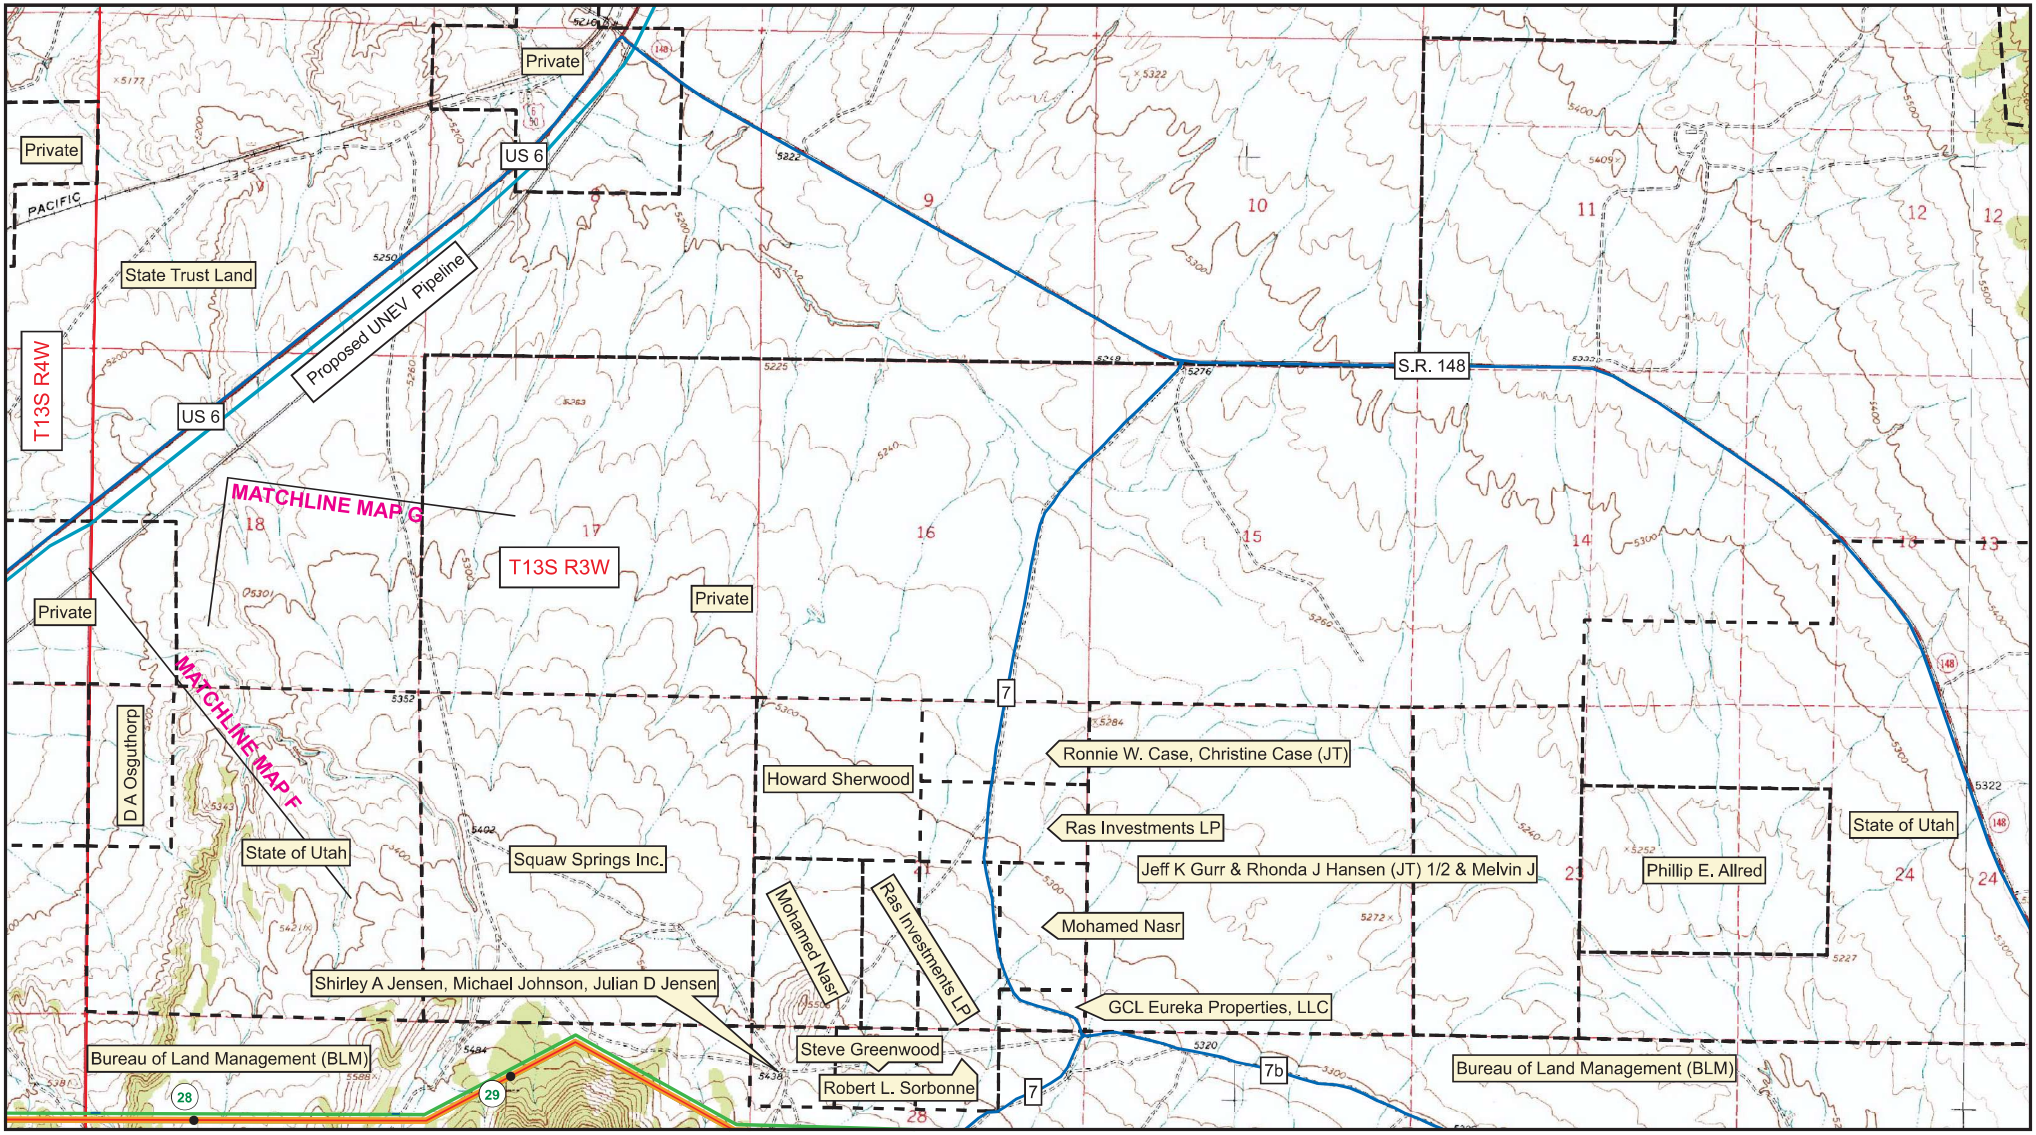

Storage Area
Permanent Right-of-way
Temporary Right-of-way
Additional Temporary Work Space
Land Ownership
Proposed Pipeline Centerline
Access Road
Storage Site Facilities Plan
Milepost

USGS 7.5' Quadrangles

Map N

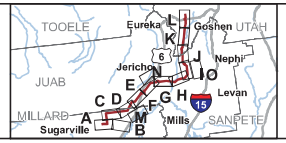

MAGNUM GAS STORAGE PROJECT

Proposed Storage Area, Pipeline Route, and Access Roads

ENTRIX
807 East South Temple, Suite 350
Salt Lake City, UT 84102
ph (801) 363-0116
fx (801) 363-0135
www.entrix.com


Coordinate System:
NAD 1983 UTM Zone 12N meter

N

0 1,000 2,000 4,000 Feet

1 inch = 2,000 feet 1:24,000


File: Entrix\Tetratech Magnum Pipeline Maps\Temp Work Space.mxd

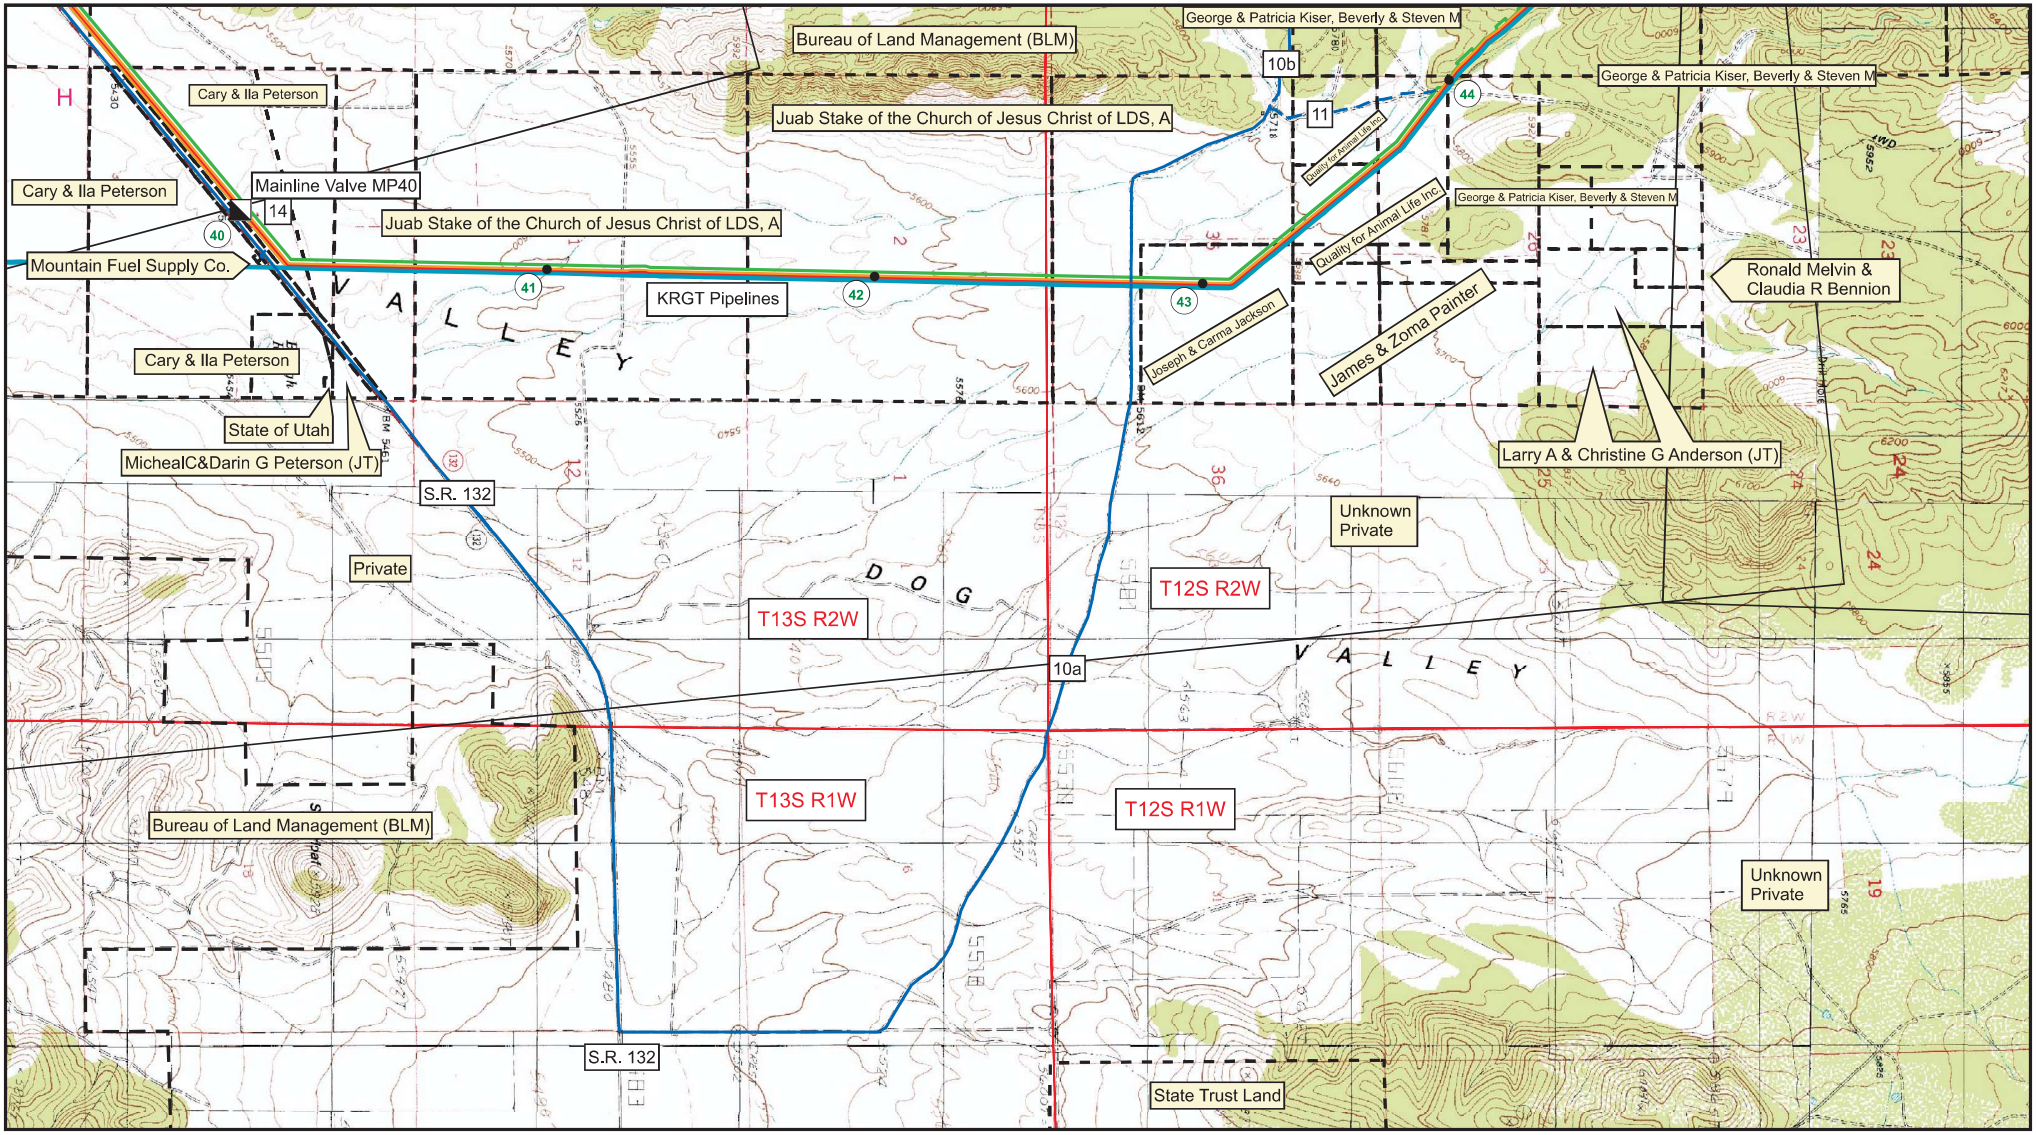

- Storage Area
- Permanent Right-of-way
- Temporary Right-of-way
- Additional Temporary Work Space
- Land Ownership
- Proposed Pipeline Centerline
- Access Road
- Access Road To Be Improved
- Storage Site Facilities Plan
- Milepost

USGS 7.5' Quadrangles

Map O

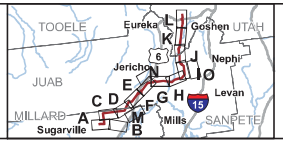

MAGNUM GAS STORAGE PROJECT

Proposed Storage Area, Pipeline Route, and Access Roads

ENTRIX
807 East South Temple, Suite 350
Salt Lake City, UT 84102
ph (801) 363-0116
fx (801) 363-0135
www.entrix.com

Coordinate System:
NAD 1983 UTM Zone 12N meter

0 1,000 2,000 4,000 Feet

1 inch = 2,000 feet 1:24,000

File: Entrix\Tetratech Magnum Pipeline Maps\Temp Work Space.mxd