APPENDIX A

MAPS AND CONSTRUCTION ALIGNMENT SHEETS

- **Appendix A-1 – Project Location Maps**
- **Appendix A-2 – National Wetlands Inventory and Soils Maps**
- **Appendix A-3 – Project Construction Alignment Sheets**
- **Appendix A-4 – Mercer Compressor Station Plan Drawing**
- **Appendix A-5 – Construction ROW Configuration Figures**

Appendix A-1 – Project Location Maps

Project Overview Map

USGS Project Location Map

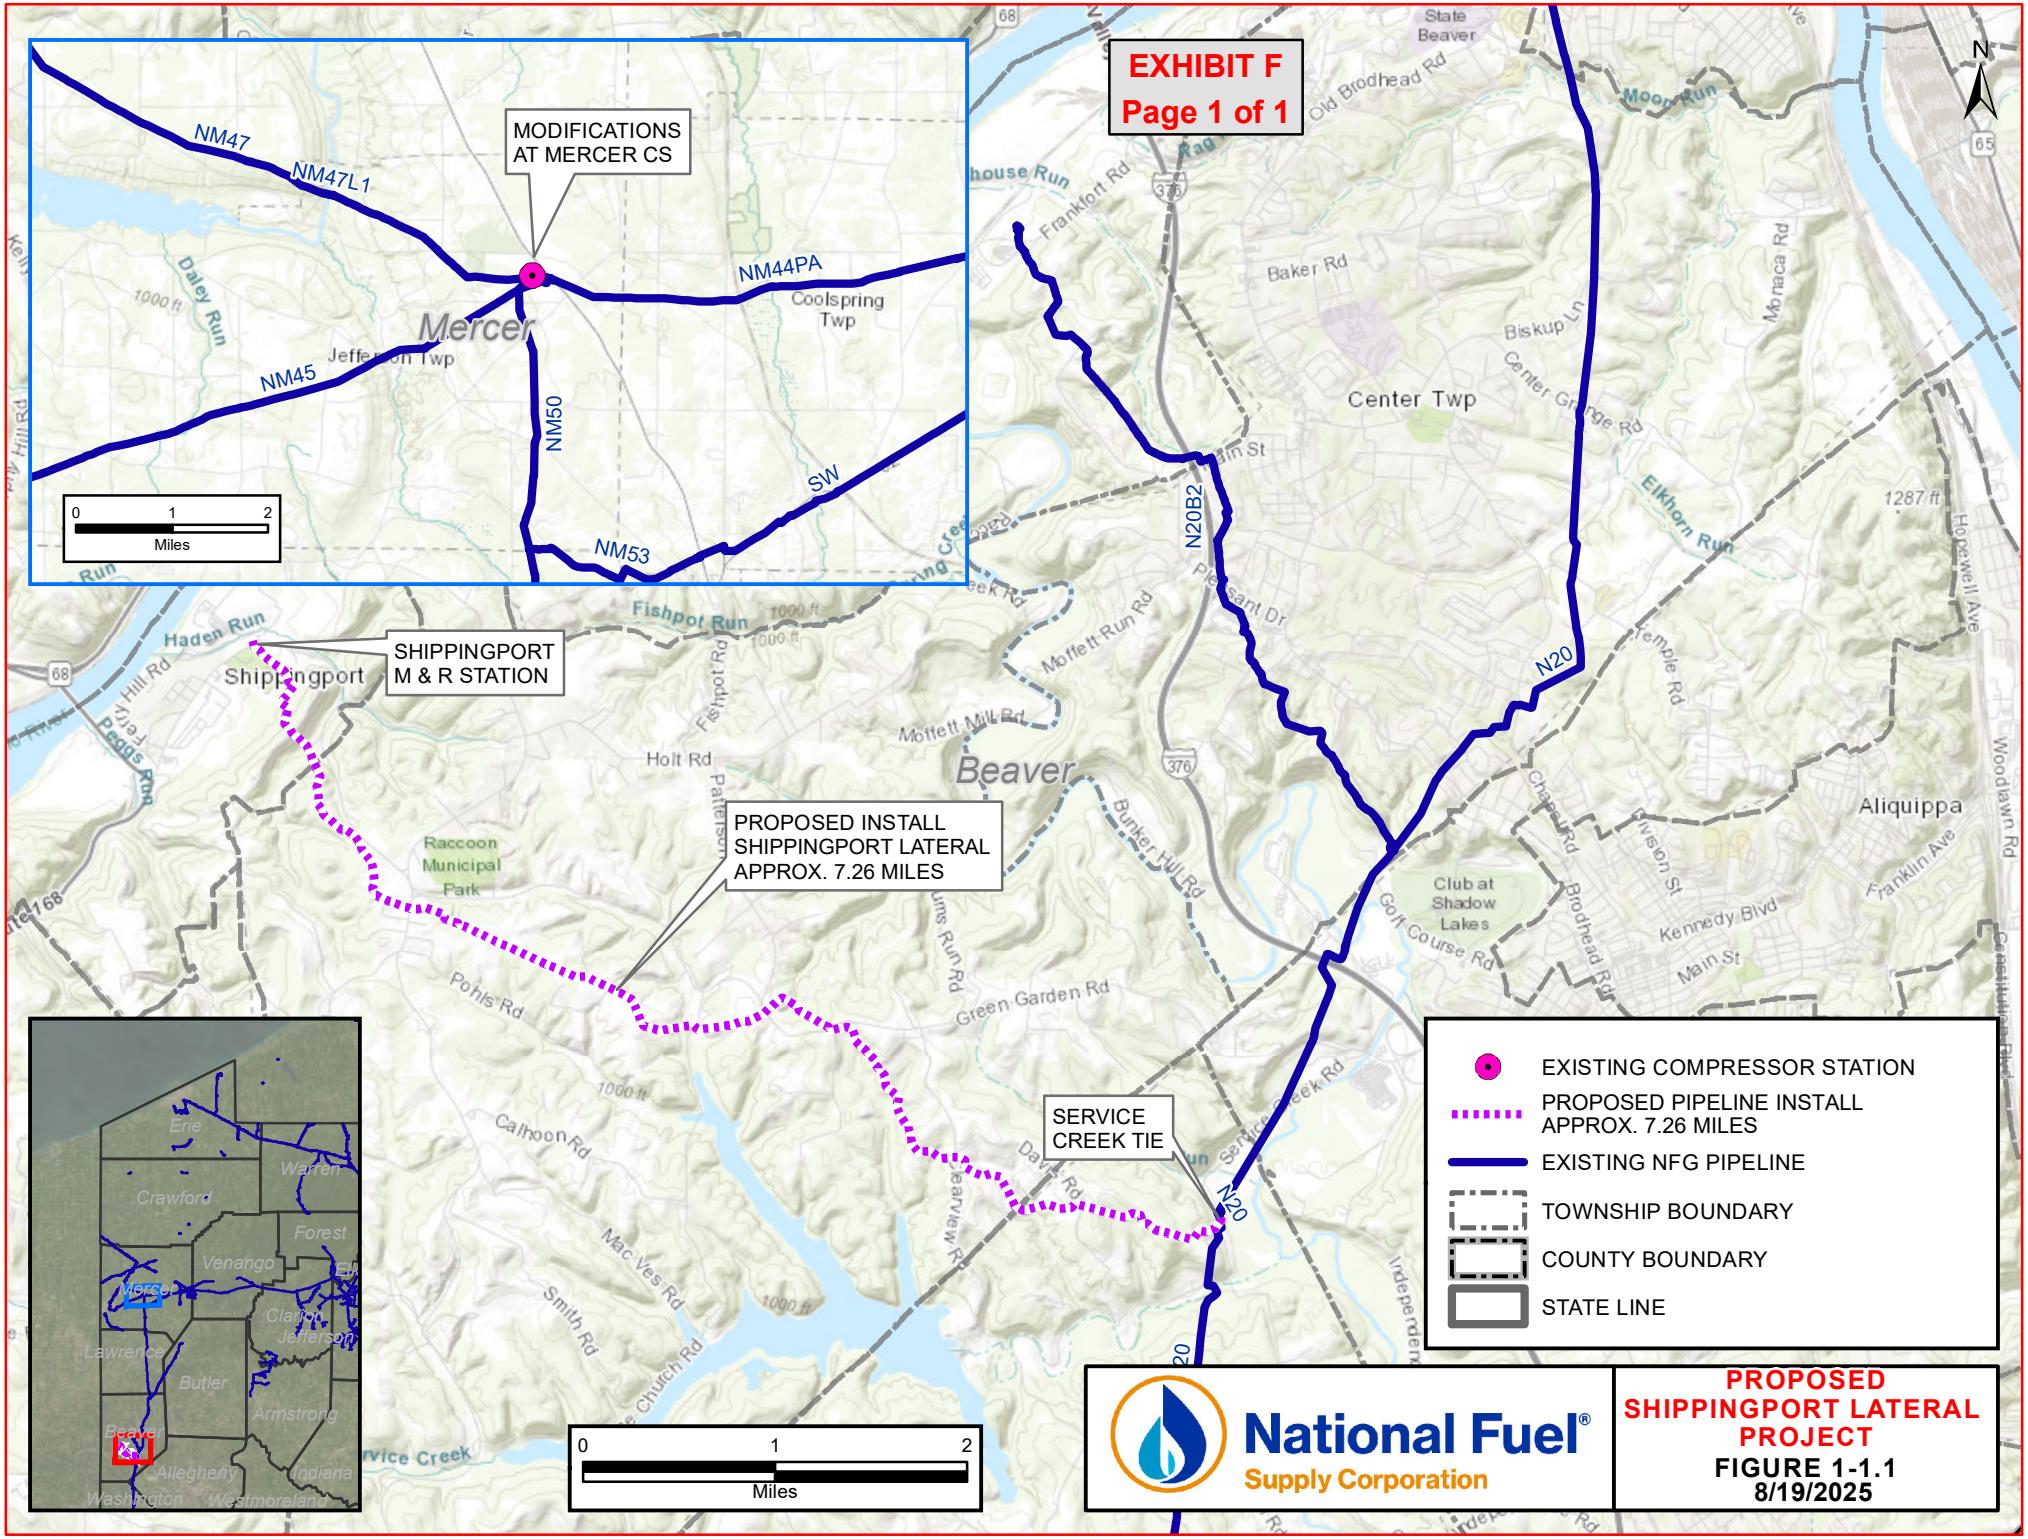
EXHIBIT F
Page 1 of 1
MODIFICATIONS AT MERCER CS
NM47
NM47L1
NM44PA
NM45
NM50
NM53
SW
Mercer
Jefferson Twp
Coolspring Twp
0 1 2
Miles
SHIPPINGPORT M & R STATION
Shippingport
PROPOSED INSTALL SHIPPINGPORT LATERAL APPROX. 7.26 MILES
SERVICE CREEK TIE
Beaver
Center Twp
Aliquippa
N20
N20B2
Haden Run
Fishpot Run
Moffett Run Rd
Moffett Mill Rd
Holt Rd
Pohls Rd
Green Garden Rd
Calhoun Rd
Mac Ves Rd
Smith Rd
Church Rd
Frankfort Rd
Baker Rd
Old Brodhead Rd
Elkhorn Run
Raccoon Municipal Park
Club at Shadow Lakes
Kennedy Blvd
Main St
Franklin Ave
Woodlawn Rd
Bunker Hill Rd
Temple Rd
Brodhead Rd
Golf Course Rd
Peggs Run Rd
Fishpot Rd
Patterson
Pleasant Dr
Biskup Ln
Center Grange Rd
Monaca Rd
Hopewell Ave
Division St
Chapel Rd
Moon Run
Rag
Daley Run
Service Creek
Erie
Warren
Crawford
Forest
Venango
Clarion
Jefferson
Lawrence
Butler
Armstrong
Beaver
Allegheny
Indiana
Washington
Westmoreland
EXISTING COMPRESSOR STATION
PROPOSED PIPELINE INSTALL APPROX. 7.26 MILES
EXISTING NFG PIPELINE
TOWNSHIP BOUNDARY
COUNTY BOUNDARY
STATE LINE
National Fuel®
Supply Corporation
PROPOSED SHIPPINGPORT LATERAL PROJECT
FIGURE 1-1.1
8/19/2025
File Path: P:\Transmission\Projects\Expansion\2025\Supply\Line N - Shippingport Lateral\Map Requests\MXDs\ProposedNLateral_ExhibitF.mxd

Shippingport M&R Station
Staging Area 2
Staging Area 3
Staging Area 5
Staging Area 4
Staging Area 6
Staging Area 7
Staging Area 8
Service Creek Tie
Midland
Hookstown
Beaver
Aliquippa
RACCOON
CENTER
RACCOON CREEK

- Line N Lateral
- Permanent Access Road (PAR)
- Temporary Access Road (TAR)
- Staging Areas
- Service Creek Tie
- Shippingport M&R Station
- USGS Quadrangle Boundary

0 670 1,340 Meters

0 2,000 4,000 Feet

Scale: 1:28,000

Source: ESRI US Topo 2013
Spatial Reference: NAD 1983 2011 StatePlane Pennsylvania South FIPS 3702 Ft US

N

Shippingport Lateral Project

USGS Project Location
Beaver County, Pennsylvania

Prepared For: National Fuel Supply Corporation	Sheet 1 of 3
Prepared By: TETRA TECH	Date: 8/18/2025

Path: C:\Users\Julie.gibson\Tetra Tech, Inc\My Data Science - My PCP\212C-BF-00598 NFG Line N\3 Client Deliverables\P1B_Figures.aprx

Cartographer: JULIE.GIBSON

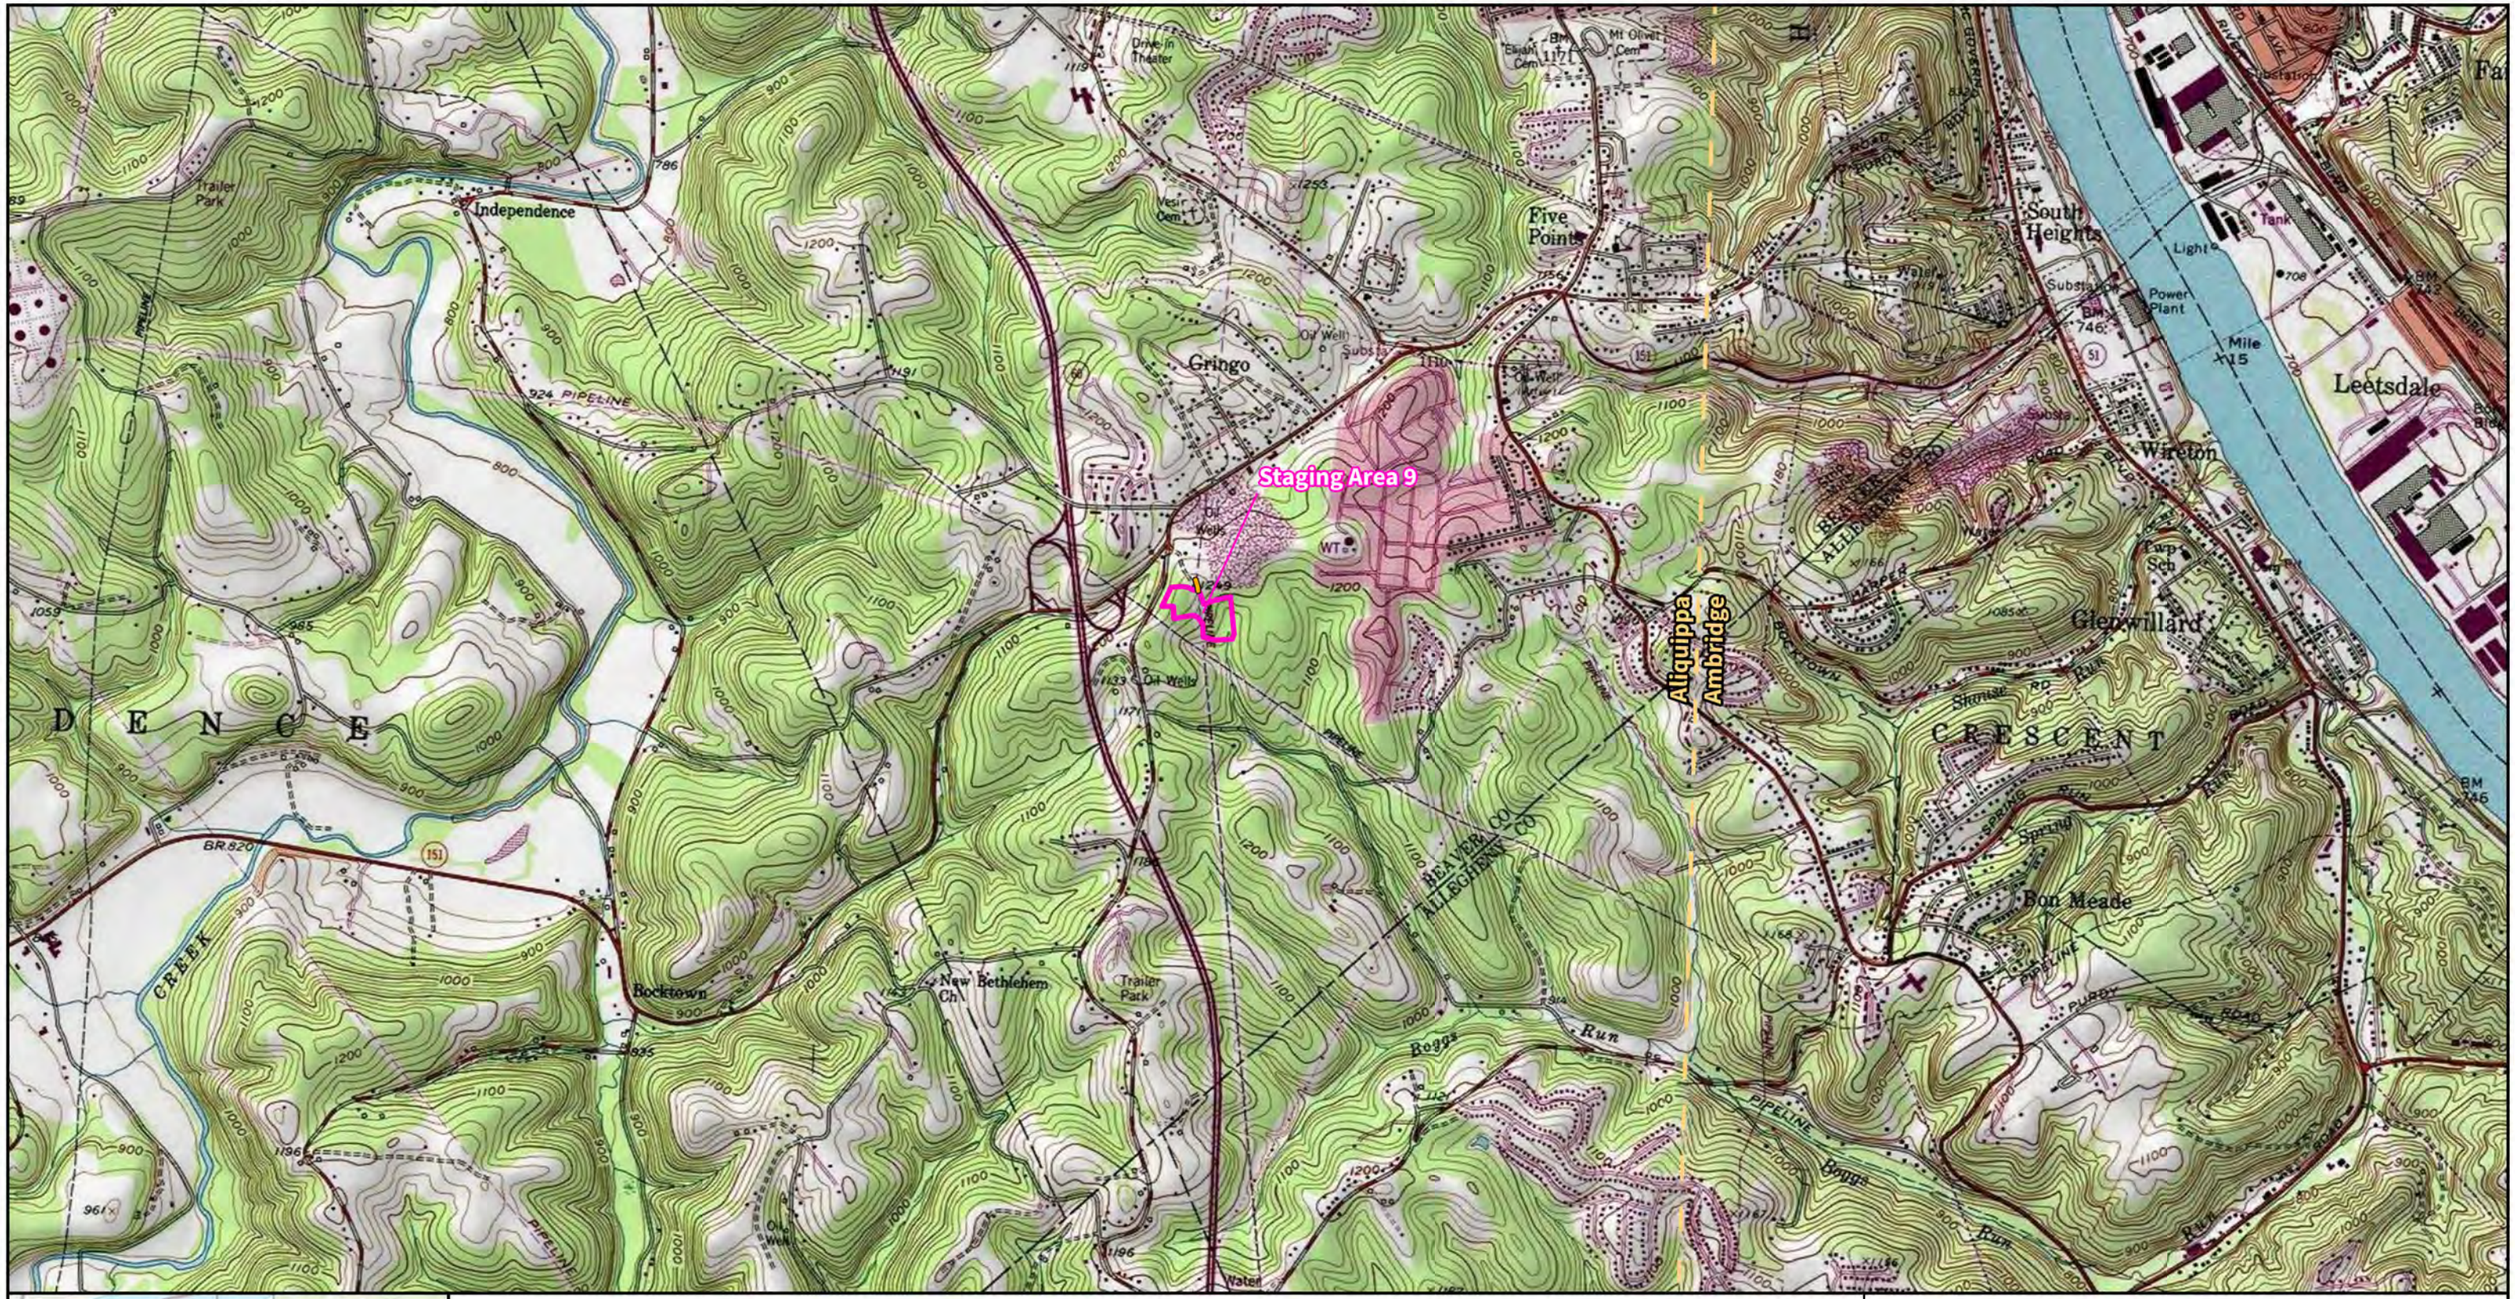

Temporary Access Road (TAR)

Staging Areas

USGS Quadrangle Boundary

0 575 1,150 Meters

0 2,000 4,000 Feet

Scale: 1:24,000

Source: ESRI US Topo 2013
Spatial Reference: NAD 1983 2011 StatePlane Pennsylvania South FIPS 3702 Ft US

N

Shippingport Lateral Project

USGS Project Location

Beaver County, Pennsylvania

Prepared For: National Fuel Supply Corporation	Sheet 2 of 3
Prepared By: TETRA TECH	Date: 8/18/2025

Path: C:\Users\Julie.gibson\Tetra Tech, Inc\My Data Science - My PCP\212C-BF-00598 NFG Line N\3 Client Deliverables\P1B_Figures.aprx

Cartographer: JULIE.GIBSON

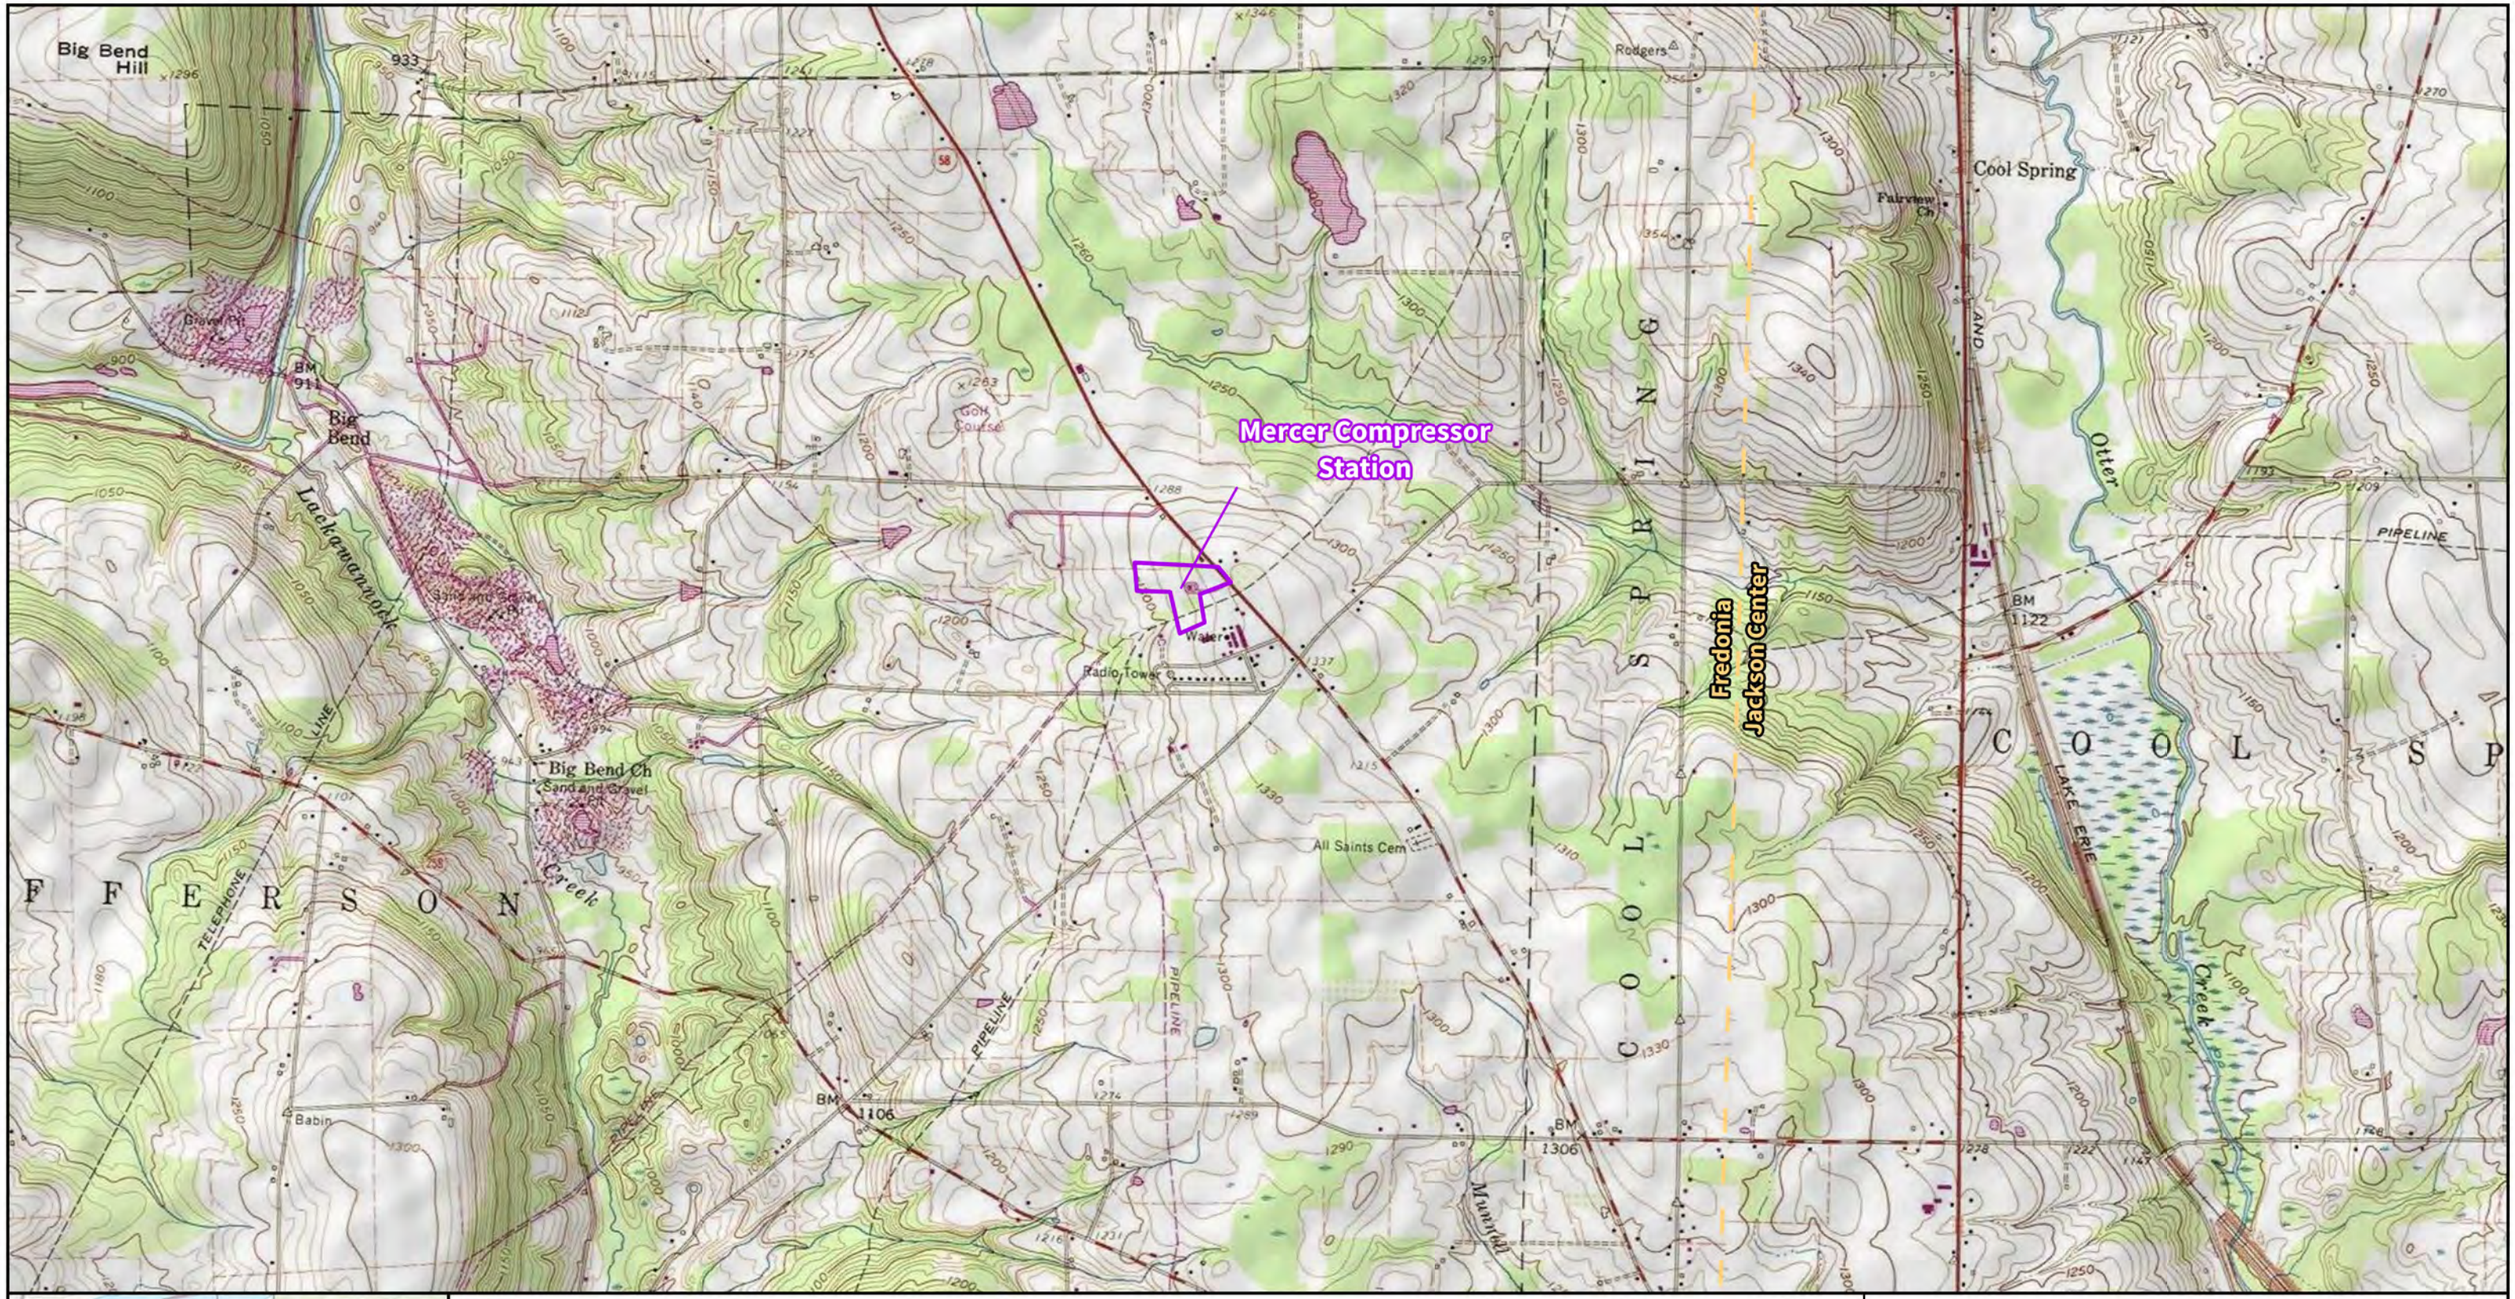

Mercer Compressor Station

USGS Quadrangle Boundary

0 575 1,150 Meters

0 2,000 4,000 Feet

Scale: 1:24,000

Source: ESRI US Topo 2013
Spatial Reference: NAD 1983 2011 StatePlane Pennsylvania South FIPS 3702 Ft US

N

Shippingport Lateral Project

USGS Project Location

Mercer County, Pennsylvania

Prepared For: National Fuel Supply Corporation	Sheet 3 of 3
Prepared By: TETRA TECH	Date: 8/18/2025

Path: C:\Users\Julie.gibson\Tetra Tech, Inc\My Data Science - My PCP\212C-BF-00598 NFG Line N\3 Client Deliverables\P1B_Figures.aprx

Cartographer: JULIE.GIBSON

Appendix A-2 – National Wetlands Inventory and Soils Maps

National Wetlands Inventory Maps

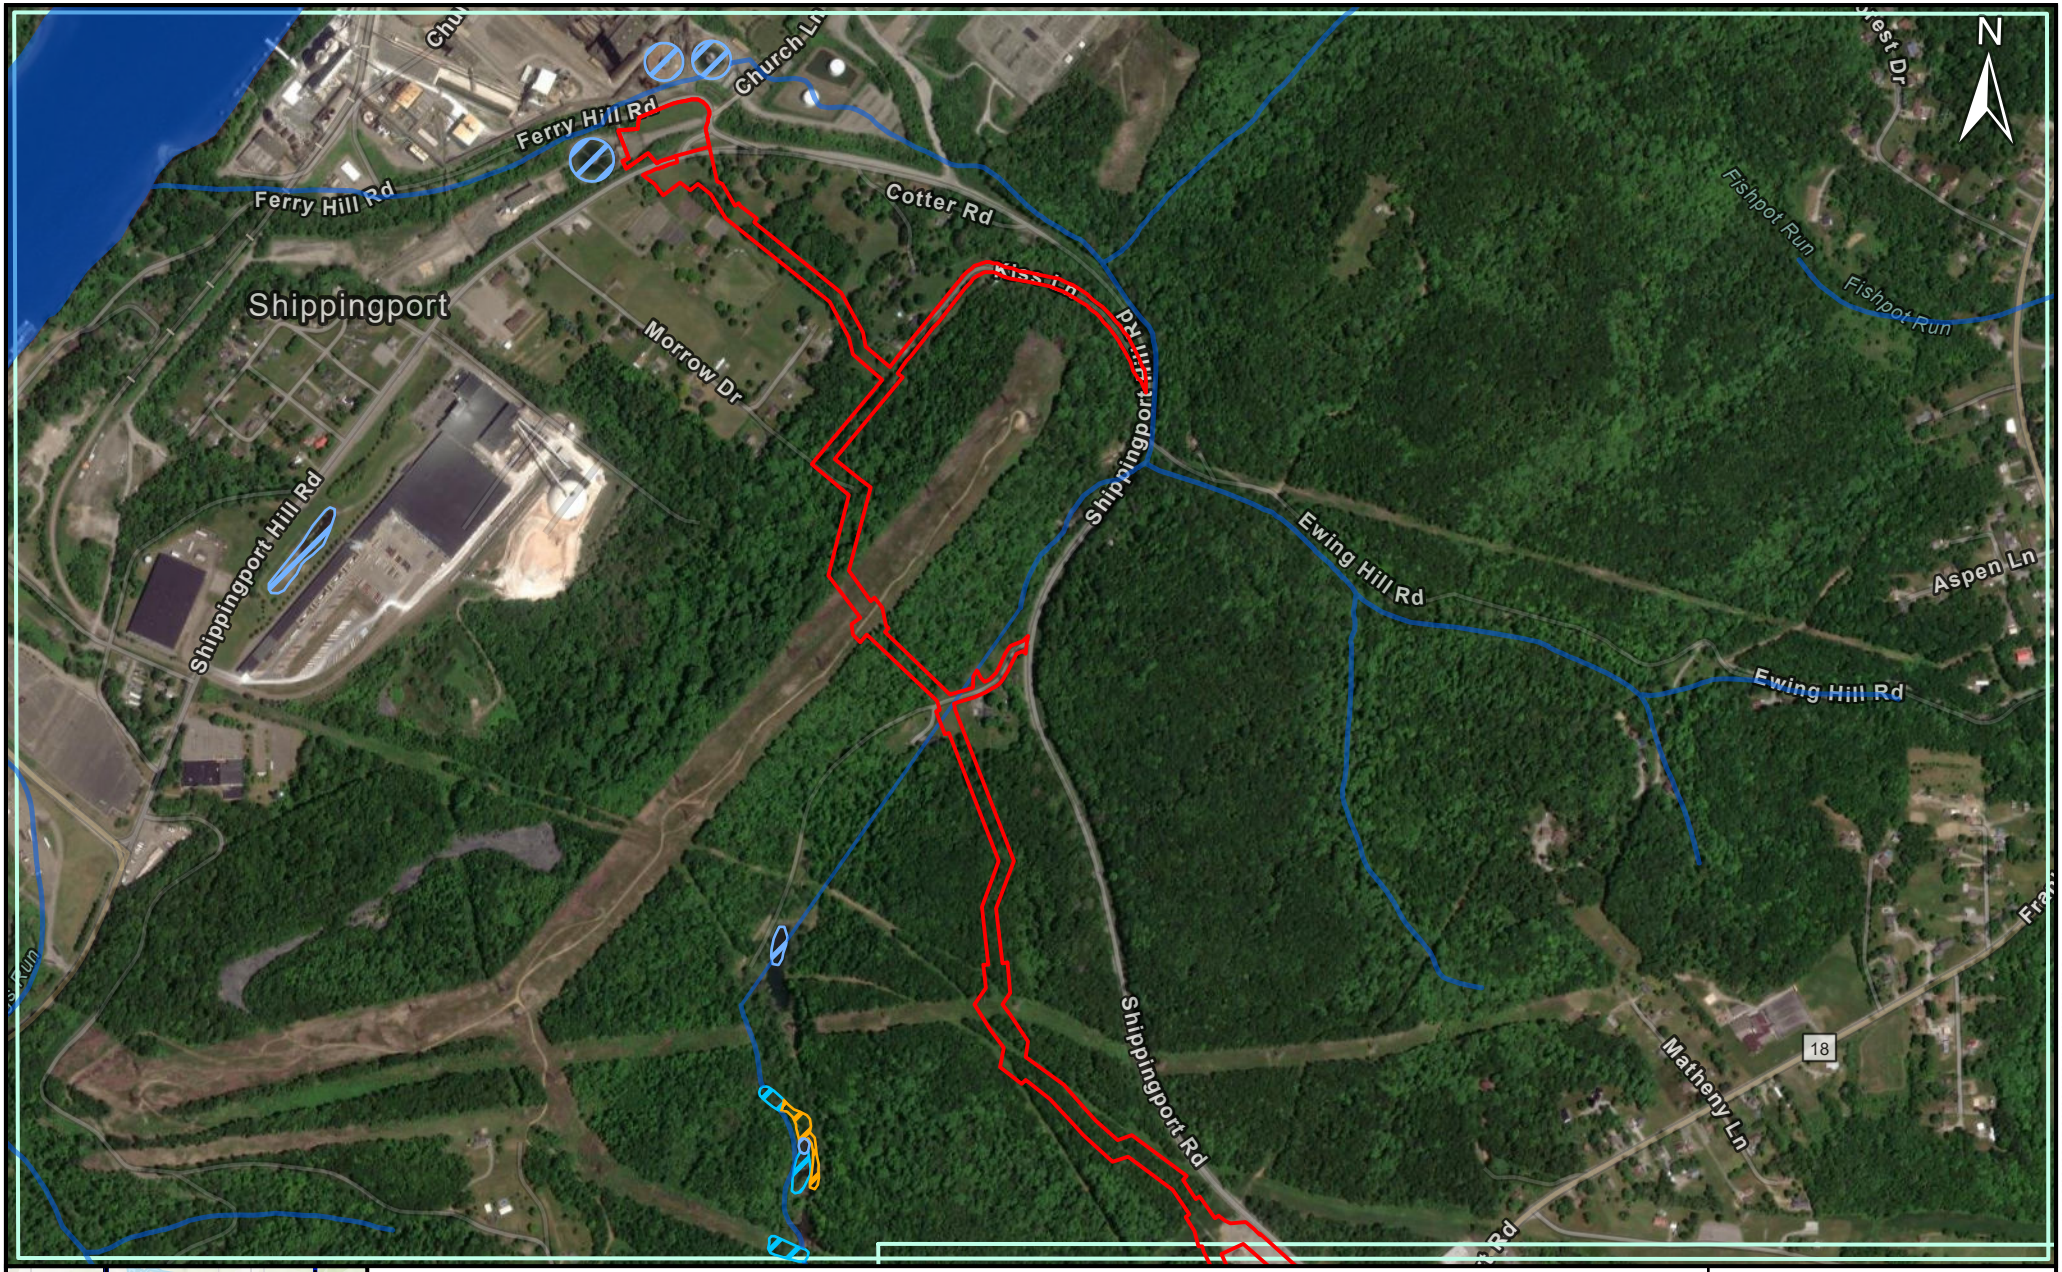

Figure 3.
National Wetlands Inventory Map
Shippingport Lateral Project
Beaver County, Pennsylvania

Prepared For: National Fuel Supply Corporation

Prepared By: TETRA TECH

Cartographer: jen.laslovich

NOT FOR CONSTRUCTION

Date: 8/13/2025

Path: C:\Users\jen.laslovich\Tetra Tech, Inc\My Data Science - My PCP\212C-BF-00598 NFG Line N\FERC\FERC.aprx

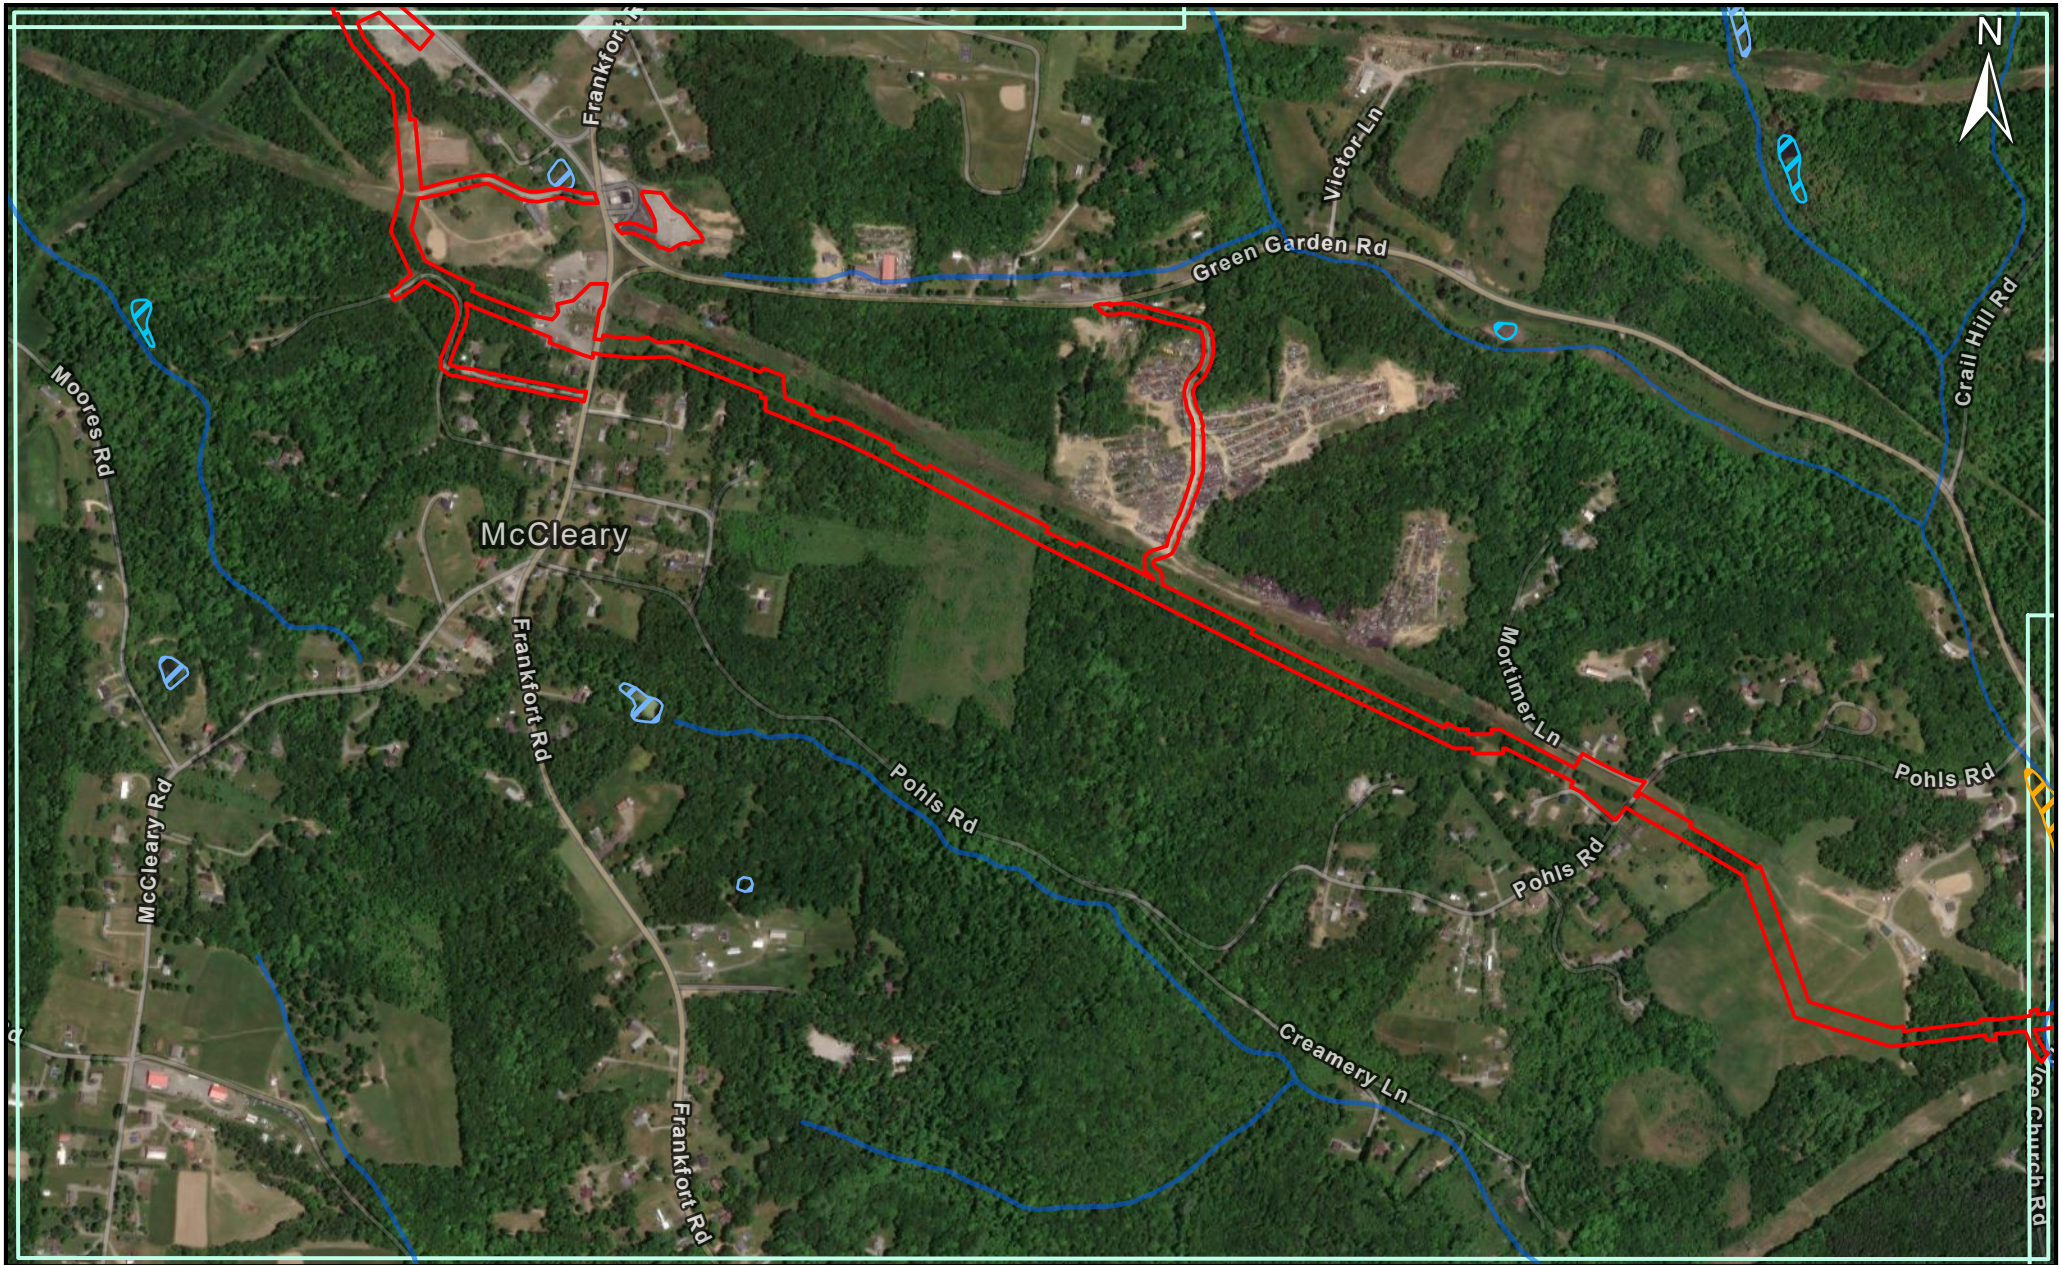

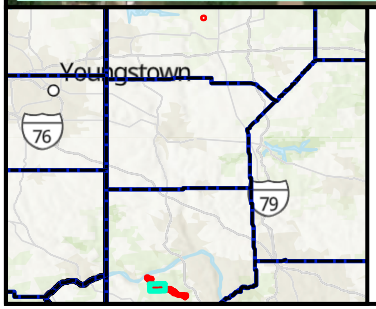

- Limit of Disturbance
- Freshwater Emergent Wetland
- Freshwater Forested/Shrub Wetland
- Freshwater Pond
- Riverine
- Sheet Boundary

0 120 240
Meters

0 490 980
Feet

Scale: 1:12,000

Spatial Reference: NAD 1983 StatePlane Pennsylvania South FIPS 3702 Feet

Basemap: ESRI World Imagery (5/27/2023)

SHEET 2 OF 6

Figure 3.
National Wetlands Inventory Map
Shippingport Lateral Project
Beaver County, Pennsylvania

Prepared For: National Fuel Supply Corporation

Prepared By: TETRA TECH

Cartographer: jen.laslovich

NOT FOR CONSTRUCTION

Date: 8/13/2025

Path: C:\Users\jen.laslovich\Tetra Tech, Inc\My Data Science - My PCP\212C-BF-00598 NFG Line N\FERC\FERC.aprx

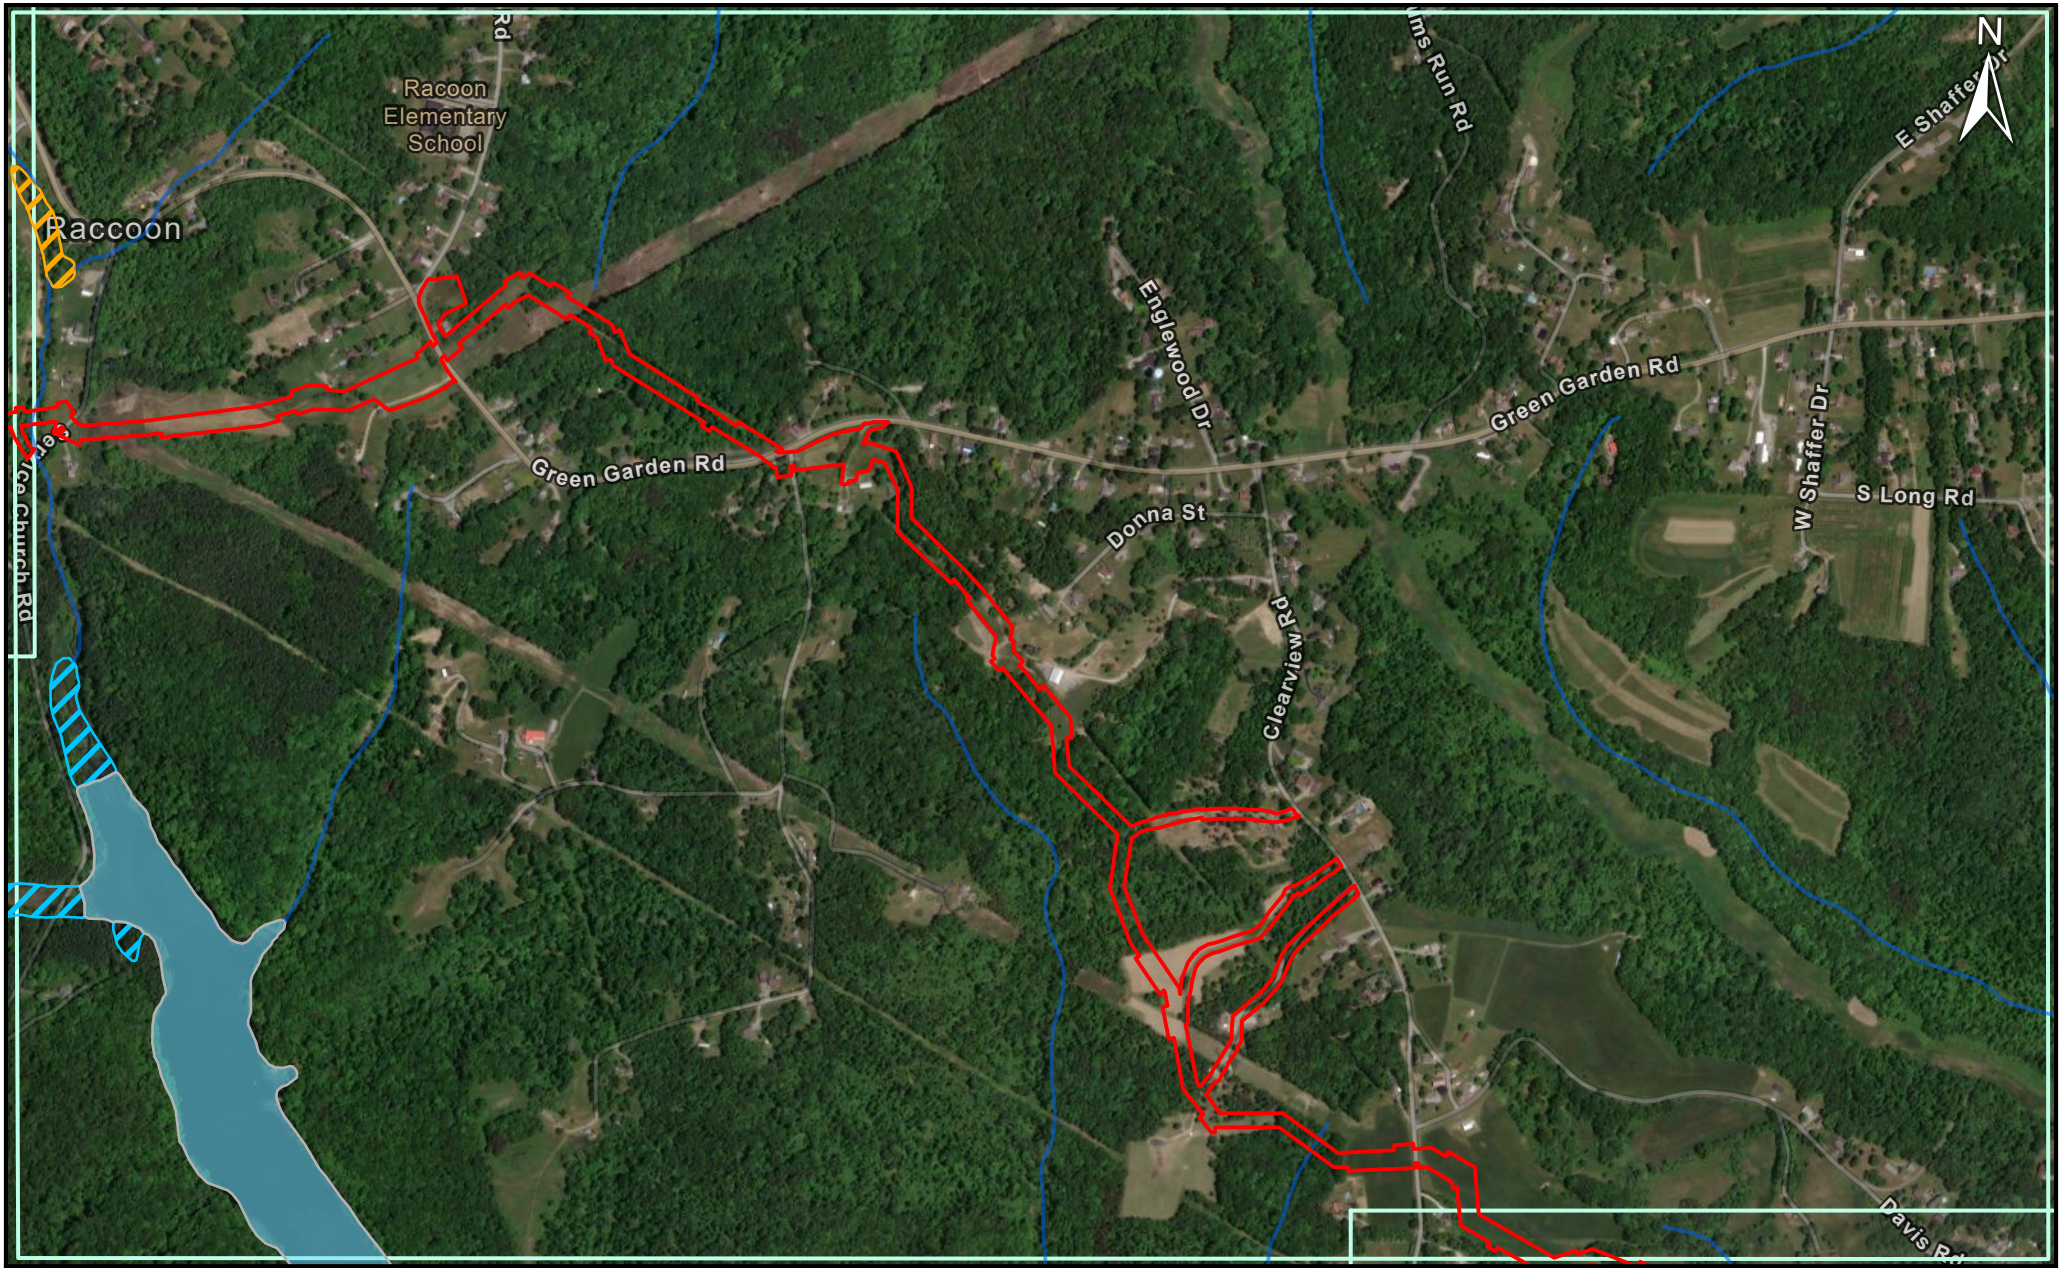

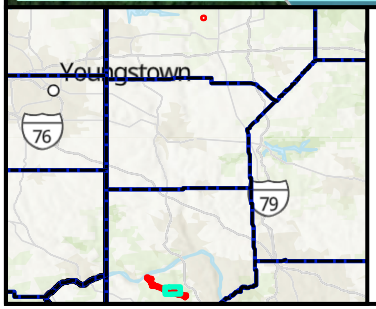

- Limit of Disturbance
- Freshwater Emergent Wetland
- Freshwater Forested/Shrub Wetland
- Lake
- Riverine
- Sheet Boundary

0 120 240
Meters

0 490 980
Feet

Scale: 1:12,000

Spatial Reference: NAD 1983 StatePlane Pennsylvania South FIPS 3702 Feet

Basemap: ESRI World Imagery (5/27/2023)

SHEET 3 OF 6

Figure 3.
National Wetlands Inventory Map
Shippingport Lateral Project
Beaver County, Pennsylvania

Prepared For: National Fuel Supply Corporation

Prepared By: TETRA TECH

Cartographer: jen.laslovich

NOT FOR CONSTRUCTION

Date: 8/13/2025

Path: C:\Users\jen.laslovich\Tetra Tech, Inc\My Data Science - My PCP\212C-BF-00598 NFG Line N\FERC\FERC.aprx

Figure 3.
National Wetlands Inventory Map
Shippingport Lateral Project
Beaver County, Pennsylvania

Prepared For: National Fuel Supply Corporation

Prepared By: TETRA TECH

Cartographer: jen.laslovich

NOT FOR CONSTRUCTION

Date: 8/13/2025

Path: C:\Users\jen.laslovich\Tetra Tech, Inc\My Data Science - My PCP\212C-BF-00598 NFG Line A\FERC\FERC.aprx

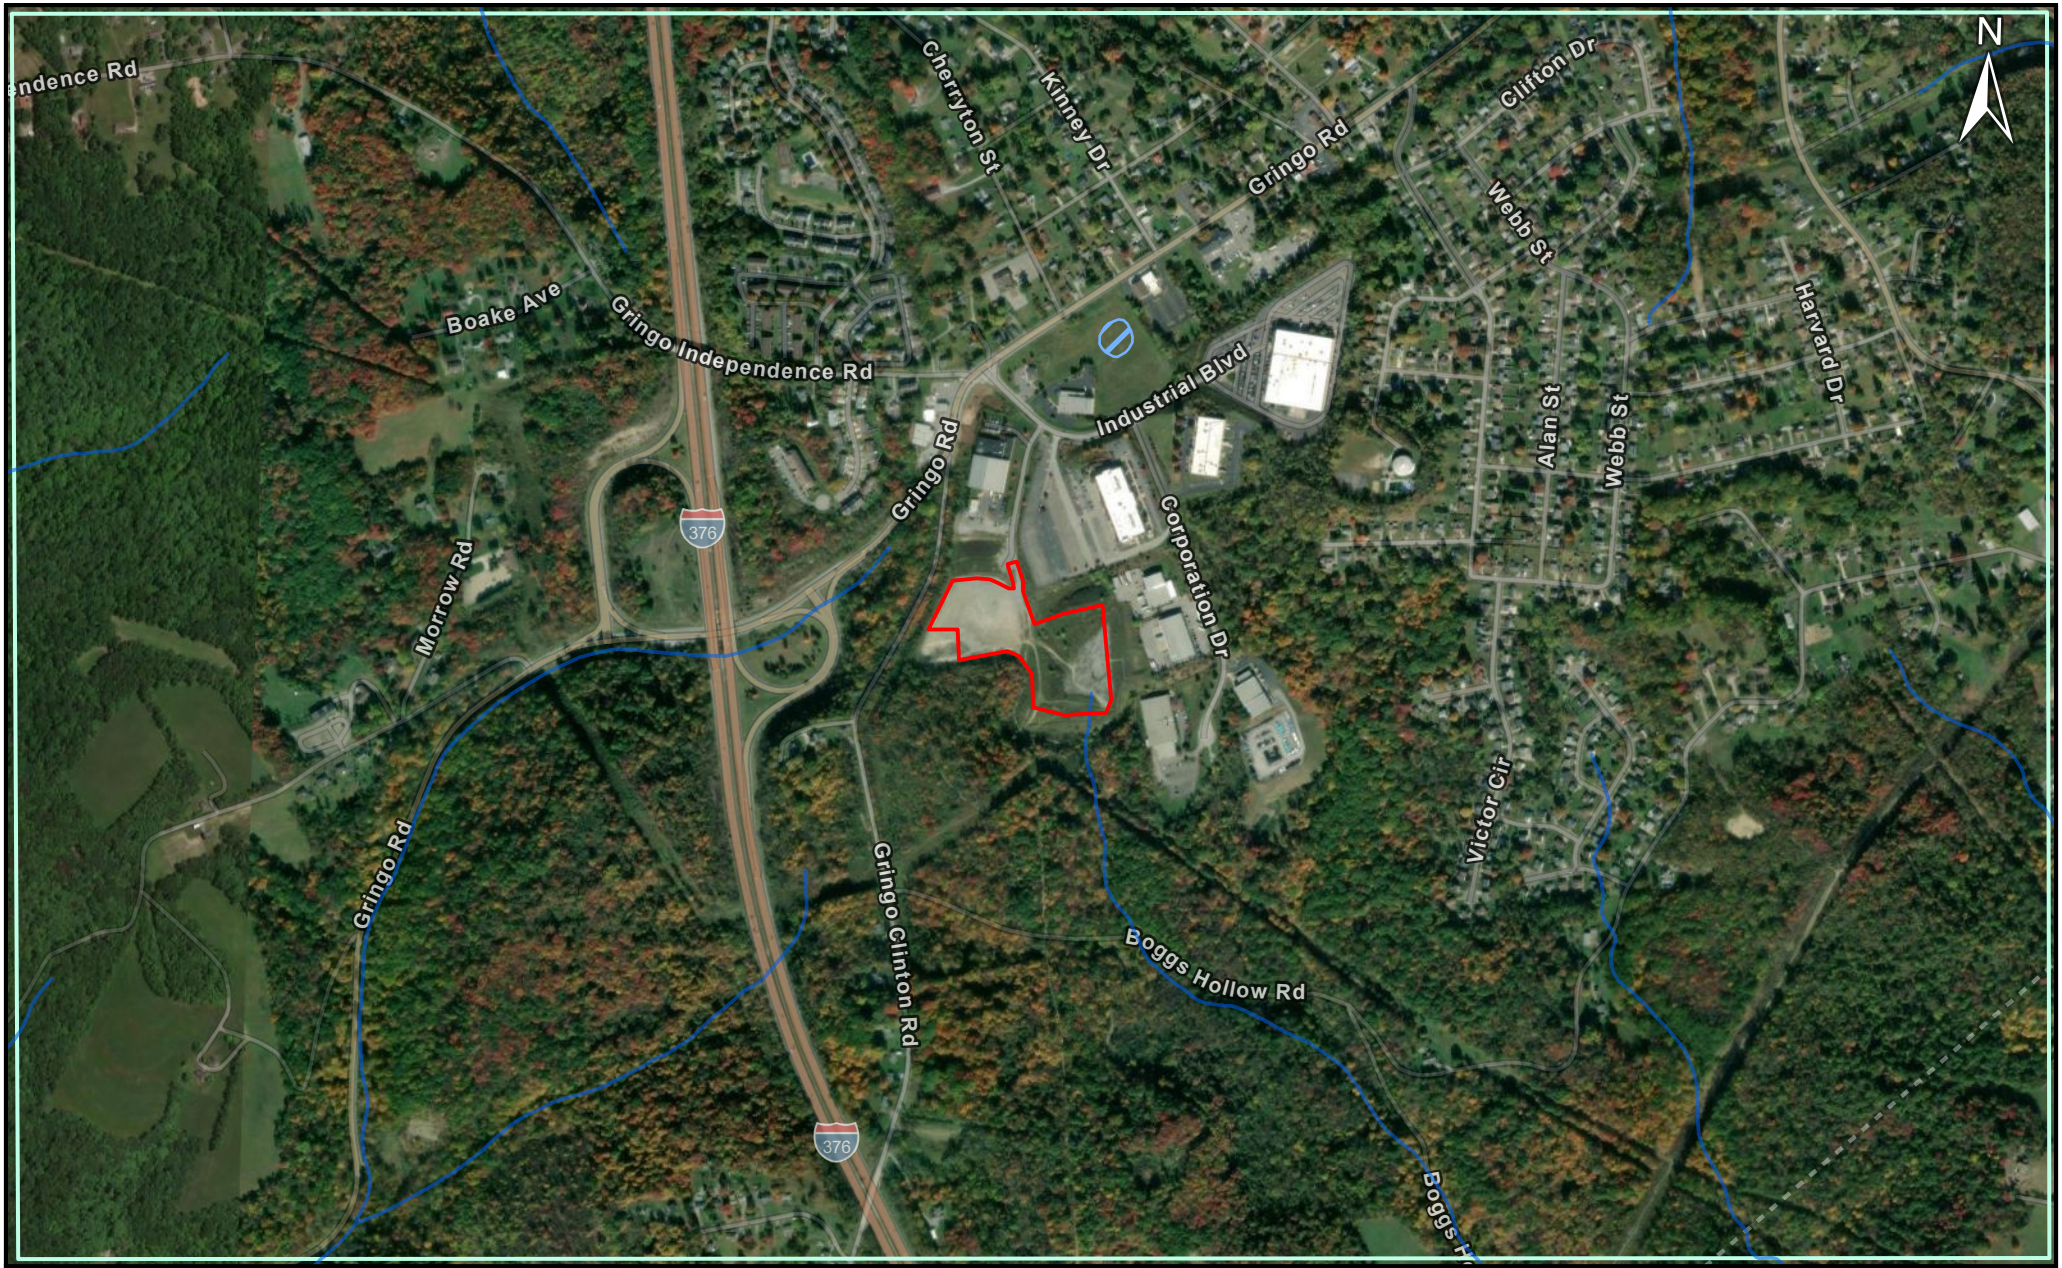

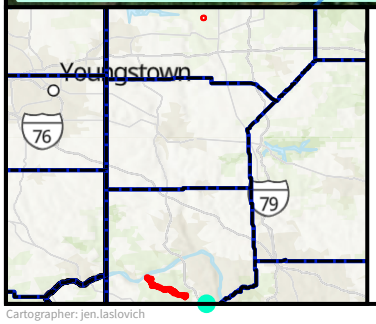

Limit of Disturbance
Freshwater Pond
Riverine
Sheet Boundary

0 120 240
Meters

0 490 980
Feet

Scale: 1:12,000

Spatial Reference: NAD 1983 StatePlane Pennsylvania South FIPS 3702 Feet

Basemap: ESRI World Imagery (11/23/2022, 10/21/2024, 5/27/2023)

SHEET 5 OF 6

Figure 3.
National Wetlands Inventory Map
Shippingport Lateral Project
Beaver County, Pennsylvania

Prepared For: National Fuel Supply Corporation

Prepared By: TETRA TECH

Cartographer: jen.laslovich

NOT FOR CONSTRUCTION

Date: 8/13/2025

Path: C:\Users\jen.laslovich\Tetra Tech, Inc\My Data Science - My PCPV\213C-BF-00598 NFG Line N\FERC\FERC.aprx

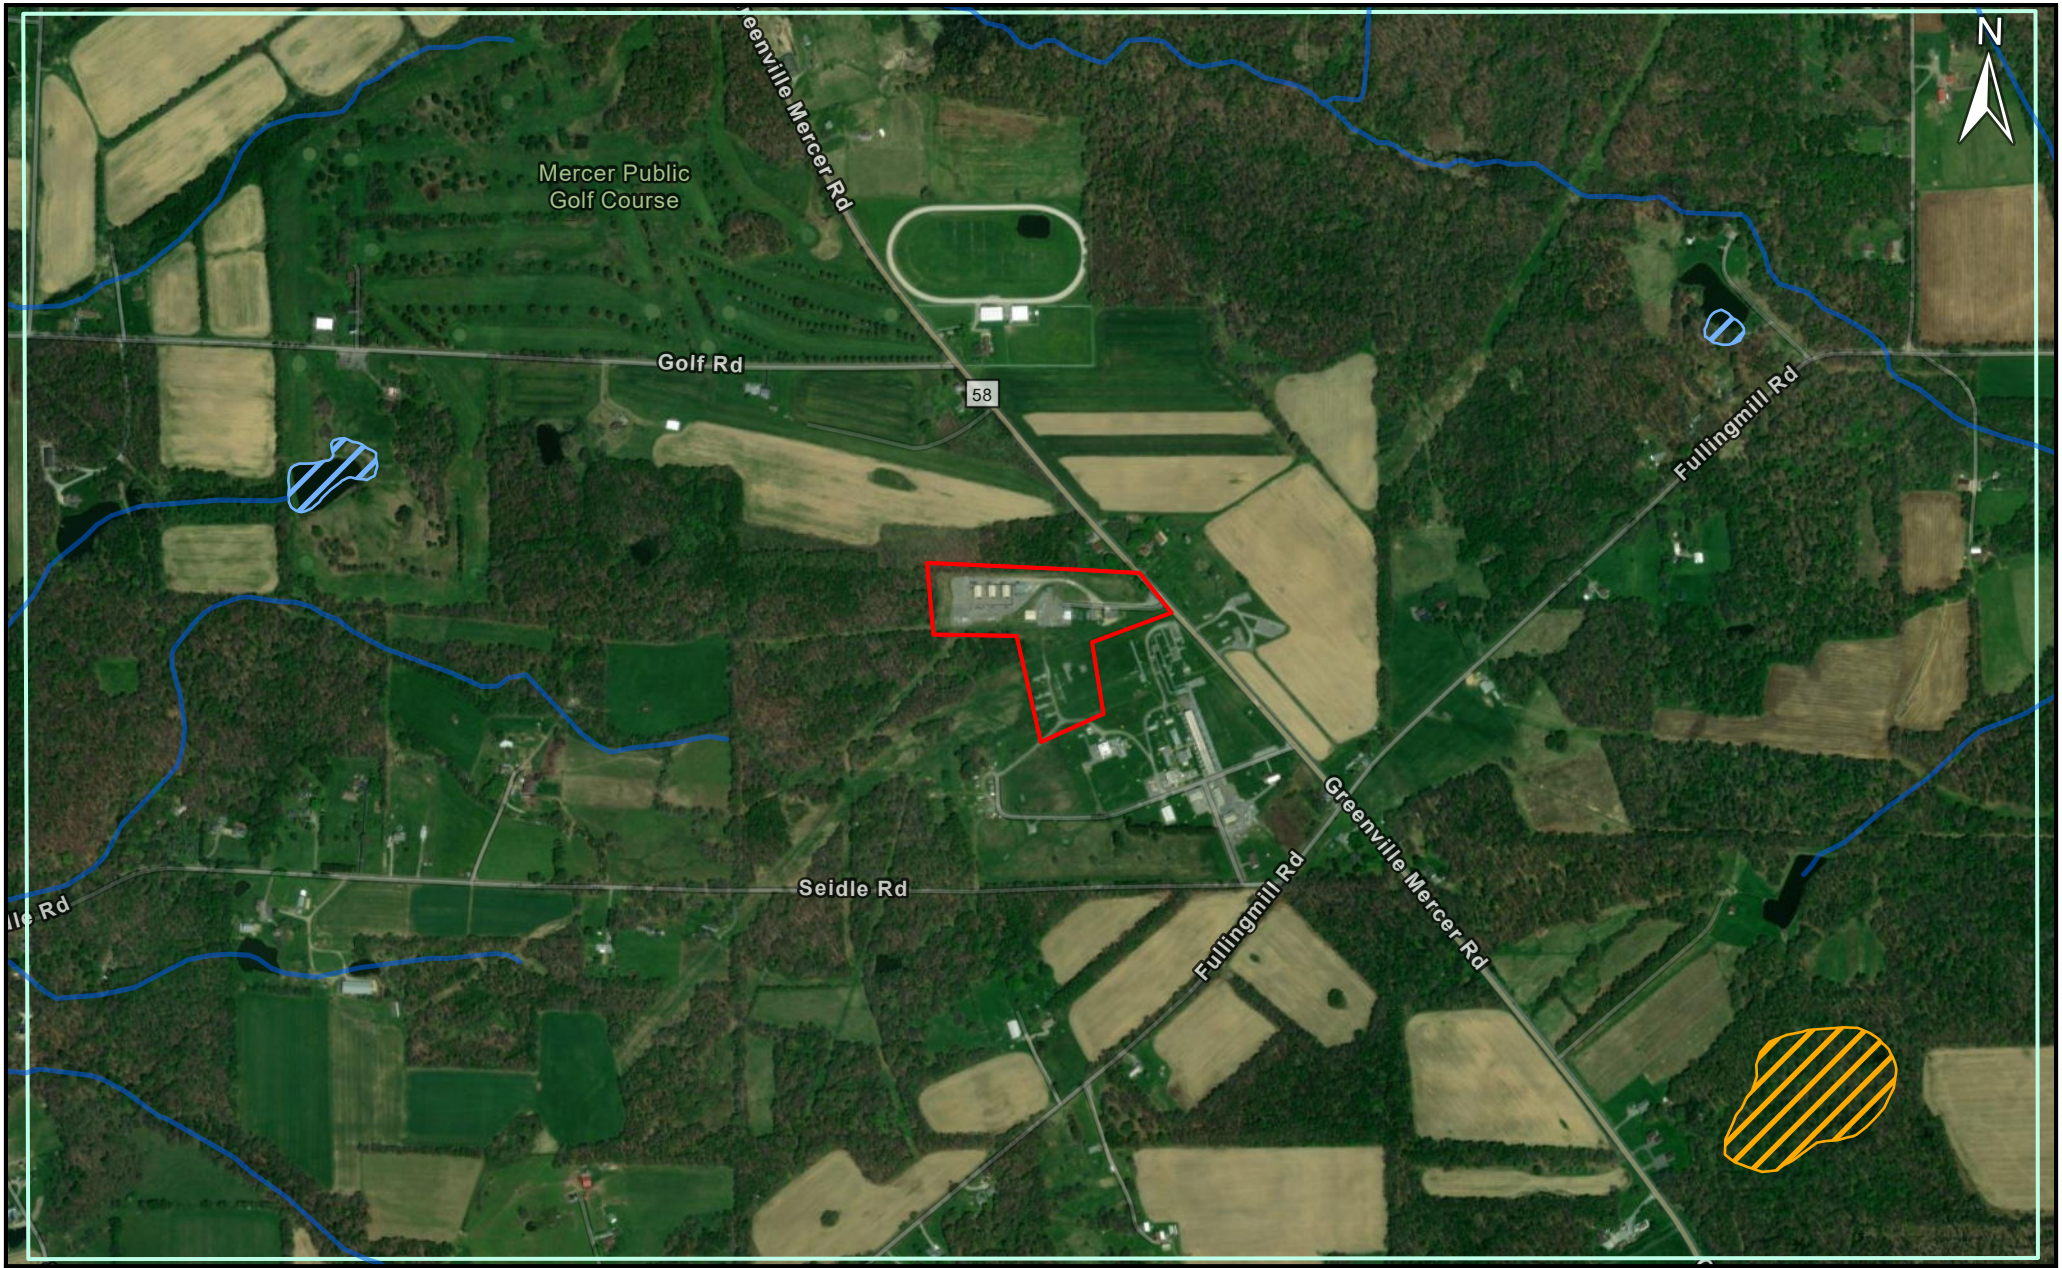

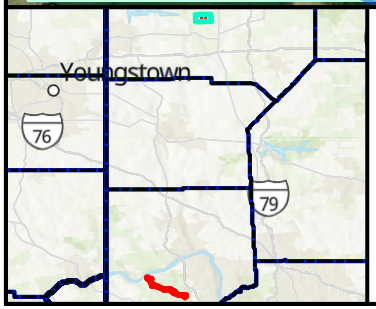

Limit of Disturbance
Freshwater Forested/Shrub Wetland
Freshwater Pond
Riverine
Sheet Boundary

0 120 240
Meters

0 490 980
Feet

Scale: 1:12,000

Spatial Reference: NAD 1983 StatePlane Pennsylvania South FIPS 3702 Feet

Basemap: ESRI World Imagery (5/2/2021)

SHEET 6 OF 6

Figure 3.
National Wetlands Inventory Map
Shippingport Lateral Project
Mercer Compressor Station
Mercer County, Pennsylvania

Prepared For: National Fuel Supply Corporation

Prepared By: TETRA TECH

Cartographer: jen.laslovich

NOT FOR CONSTRUCTION

Date: 8/13/2025

Path: C:\Users\jen.laslovich\Tetra Tech, Inc\My Data Science - My PCPv21\2C-BF-005598 NFG Line N\FERC\FERC.aprx

Soils Maps

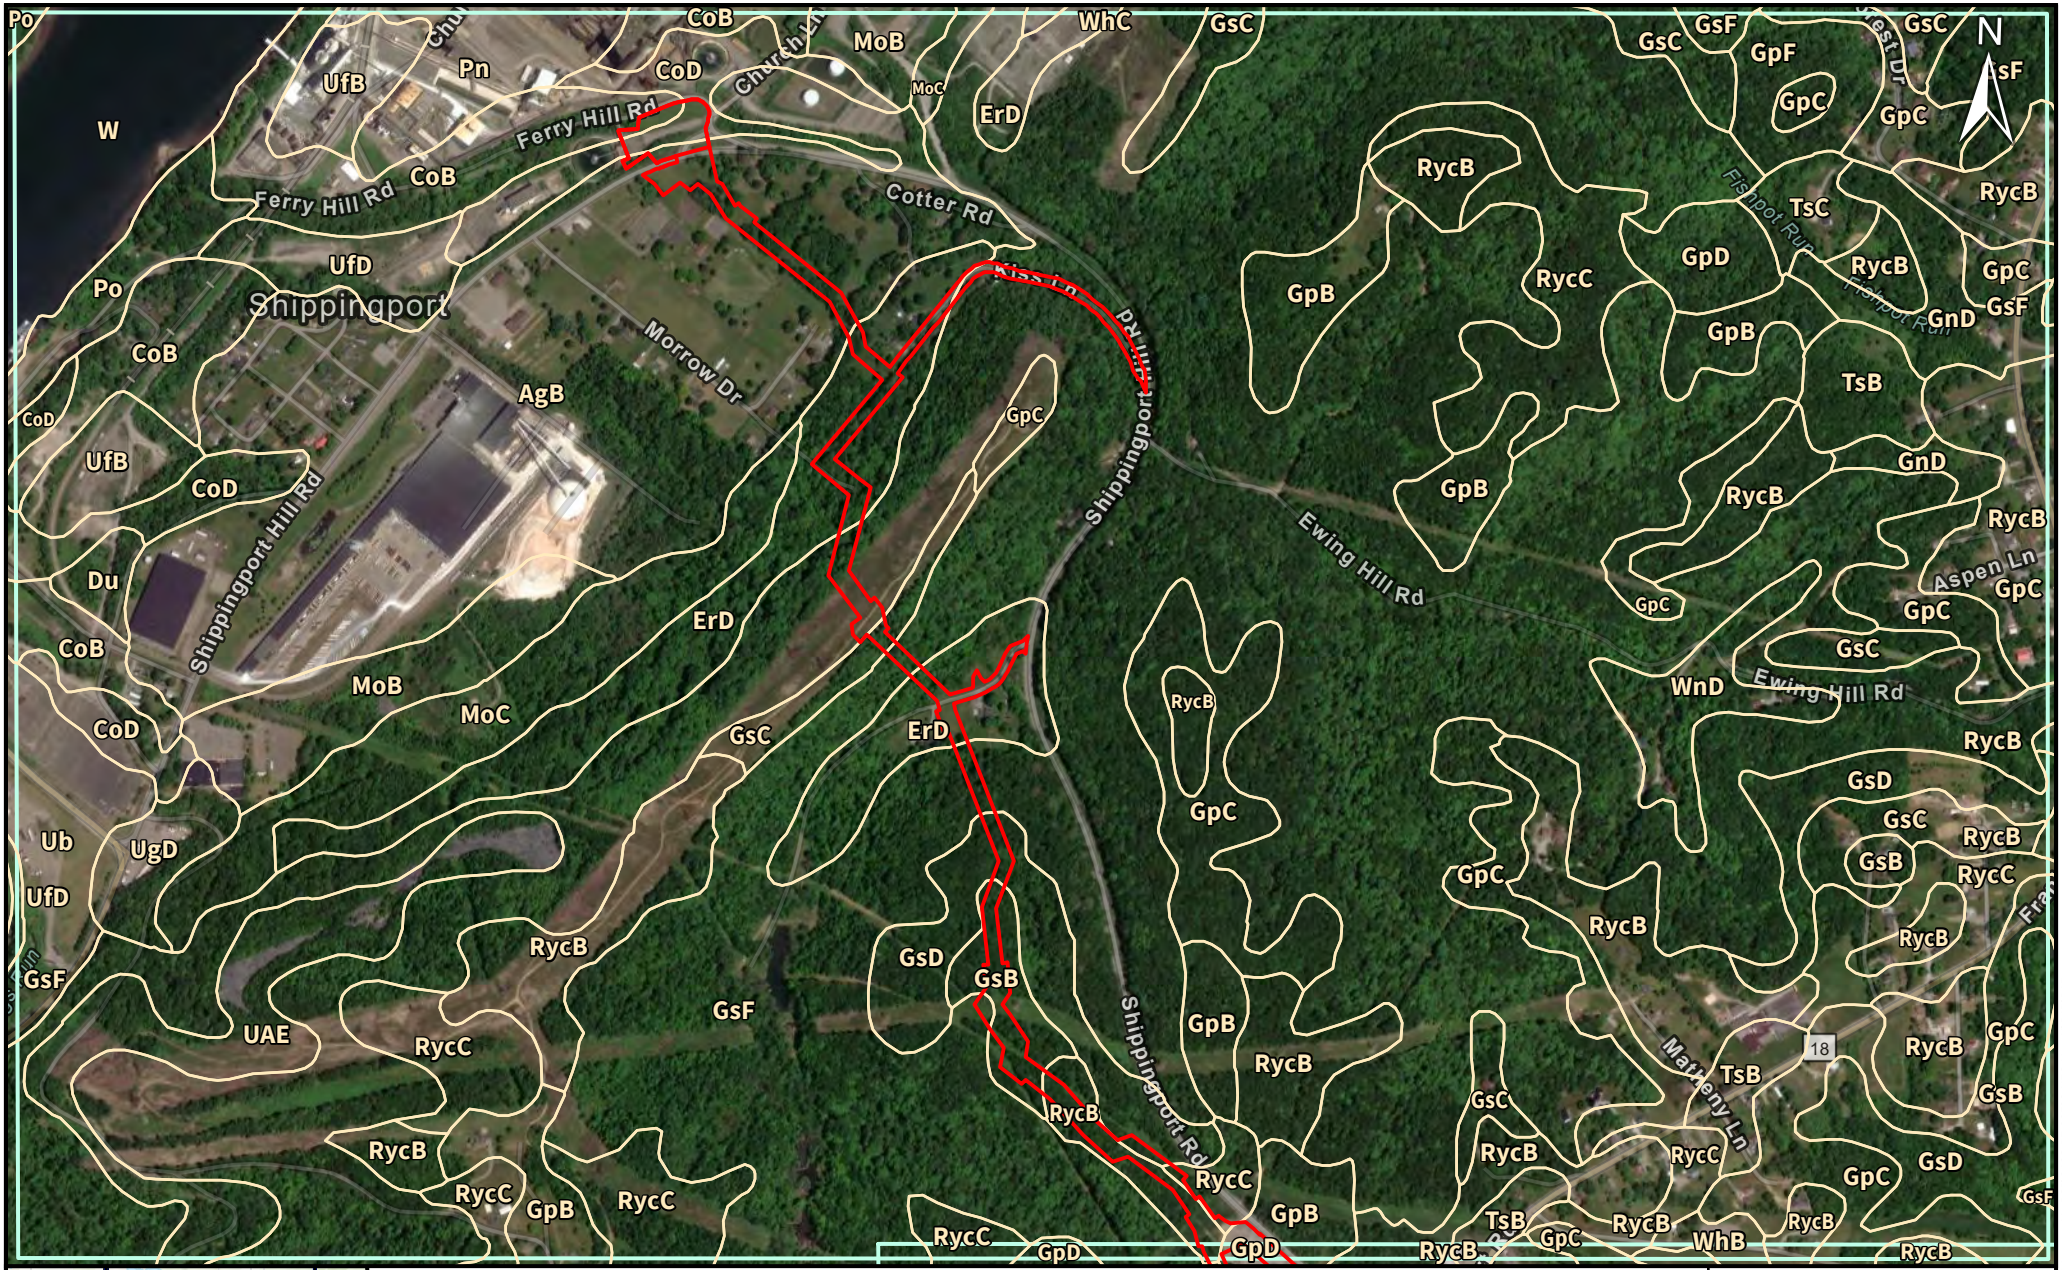

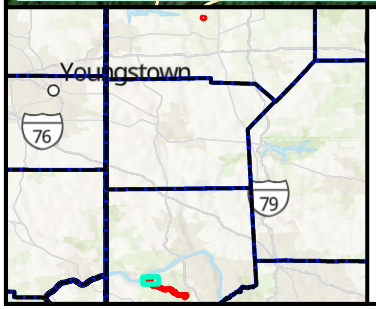

Limit of Disturbance

USDA Soil Boundary

Sheet Boundary

0 120 240
Meters

0 490 980
Feet

Scale: 1:12,000

Spatial Reference: NAD 1983 StatePlane Pennsylvania South FIPS 3702 Feet

Basemap: ESRI World Imagery (5/27/2023)

SHEET 1 OF 6

USDA NRCS Soils Map

Figure 4
Shippingport Lateral Project
Beaver County; Pennsylvania

Prepared For: National Fuel Supply Corporation

Prepared By: TETRA TECH

Cartographer: jen.laslovich

NOT FOR CONSTRUCTION

Date: 8/11/2025

Path: C:\Users\jen.laslovich\Tetra Tech, Inc\My Data Science - My PC\PA\12C-BF-00598 NFG Line NW\18\P18.aprx

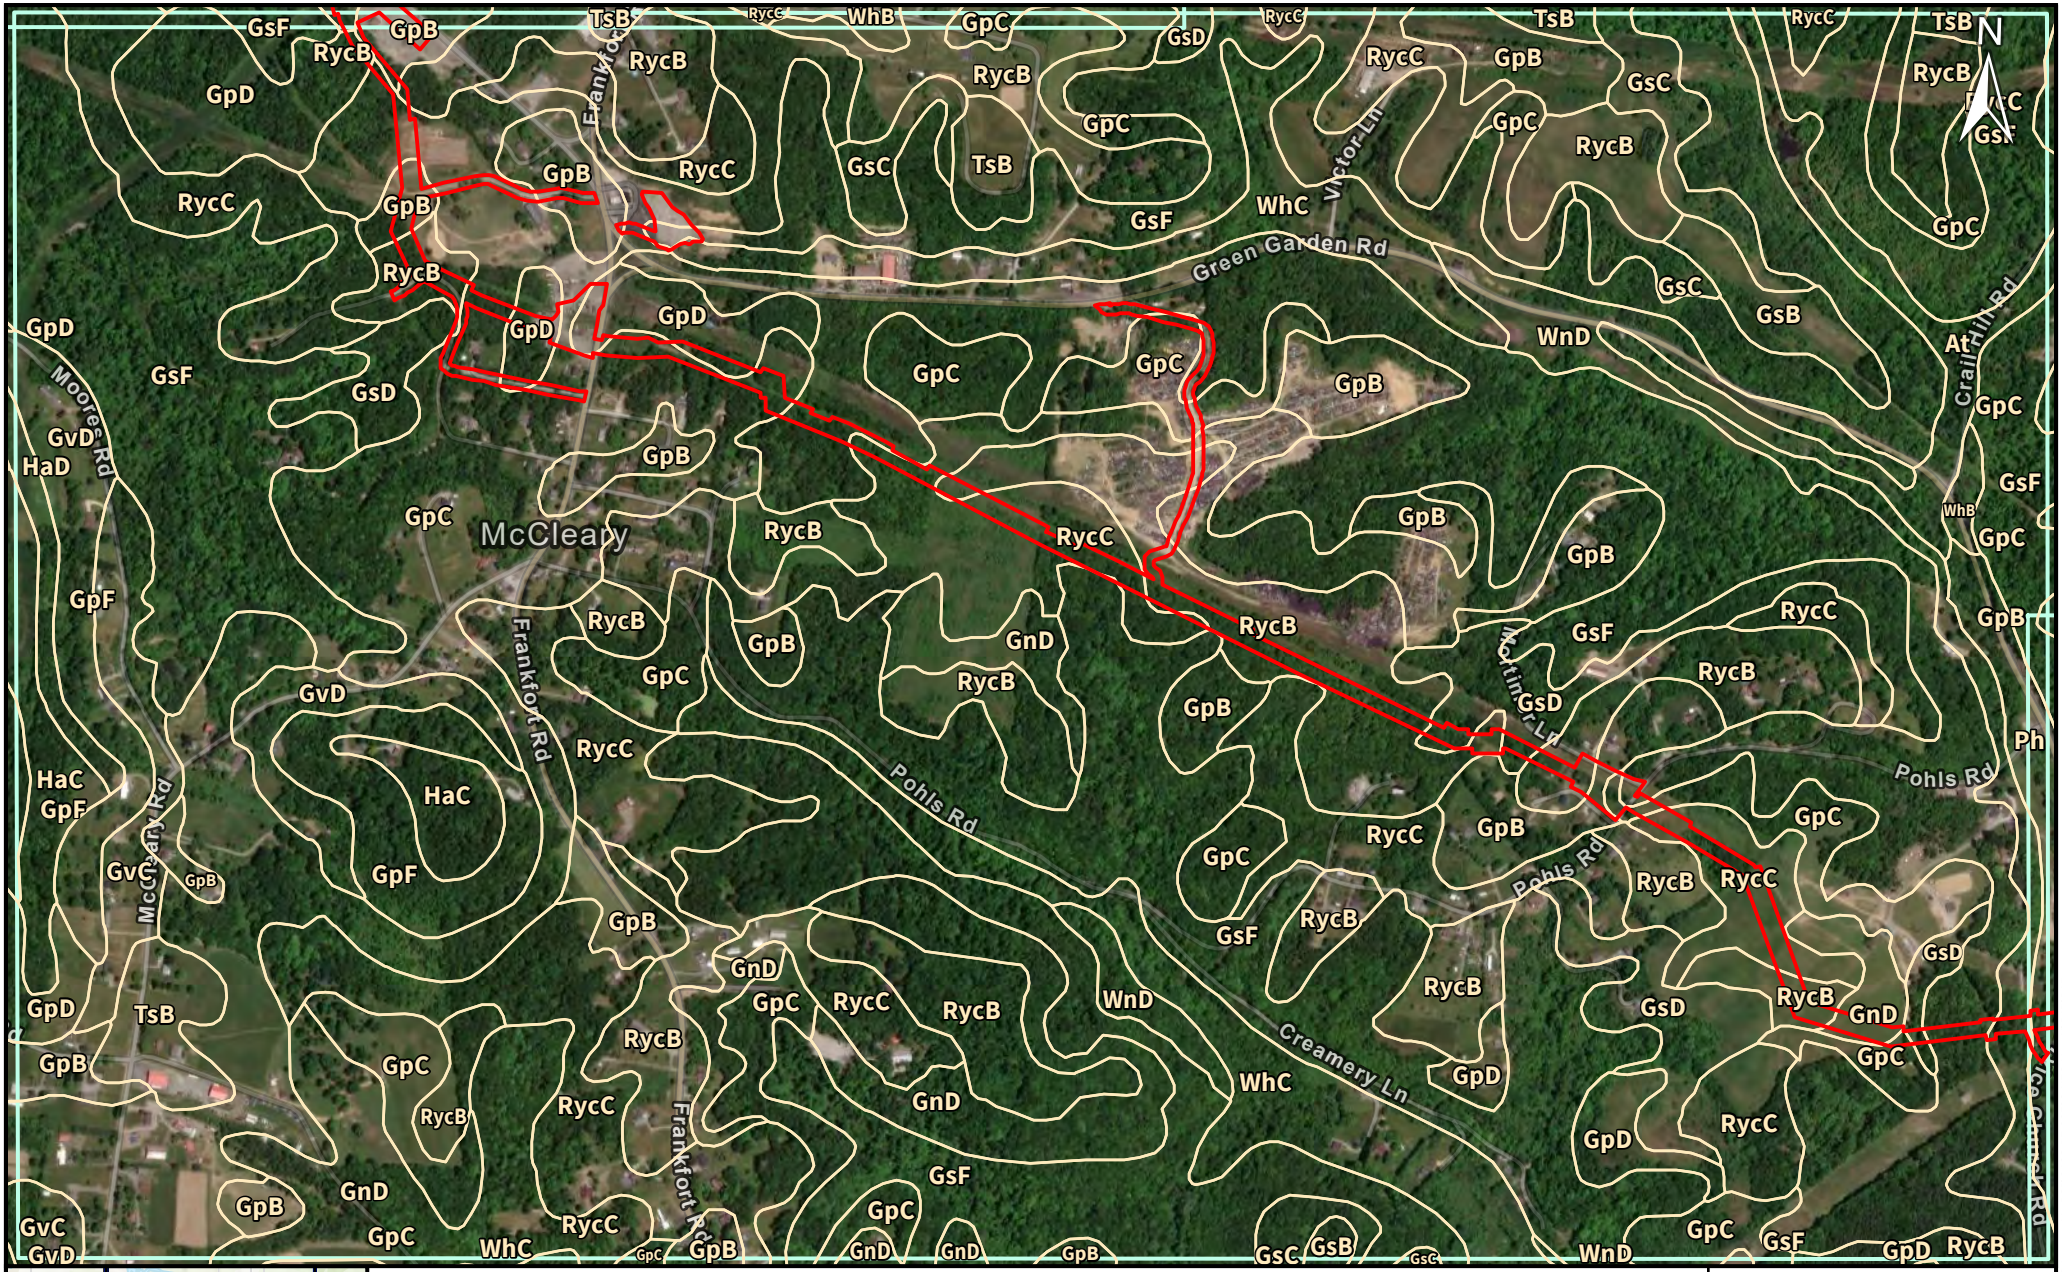

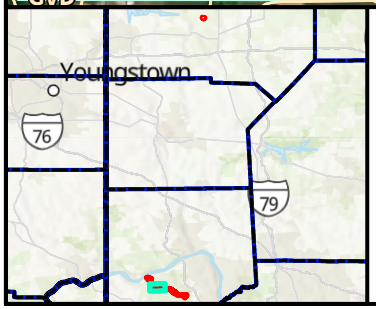

Limit of Disturbance

USDA Soil Boundary

Sheet Boundary

0 120 240
Meters

0 490 980
Feet

Scale: 1:12,000

Spatial Reference: NAD 1983 StatePlane Pennsylvania South FIPS 3702 Feet

Basemap: ESRI World Imagery (5/27/2023)

SHEET 2 OF 6

USDA NRCS Soils Map

Figure 4
Shippingport Lateral Project
Beaver County; Pennsylvania

Prepared For: National Fuel Supply Corporation

Prepared By: TETRA TECH

Cartographer: jen.laslovich

NOT FOR CONSTRUCTION

Date: 8/11/2025

Path: C:\Users\jen.laslovich\Tetra Tech, Inc\My Data Science - My PCPV\13C-DF-60598 NFG Line NW\18\P18.aprx

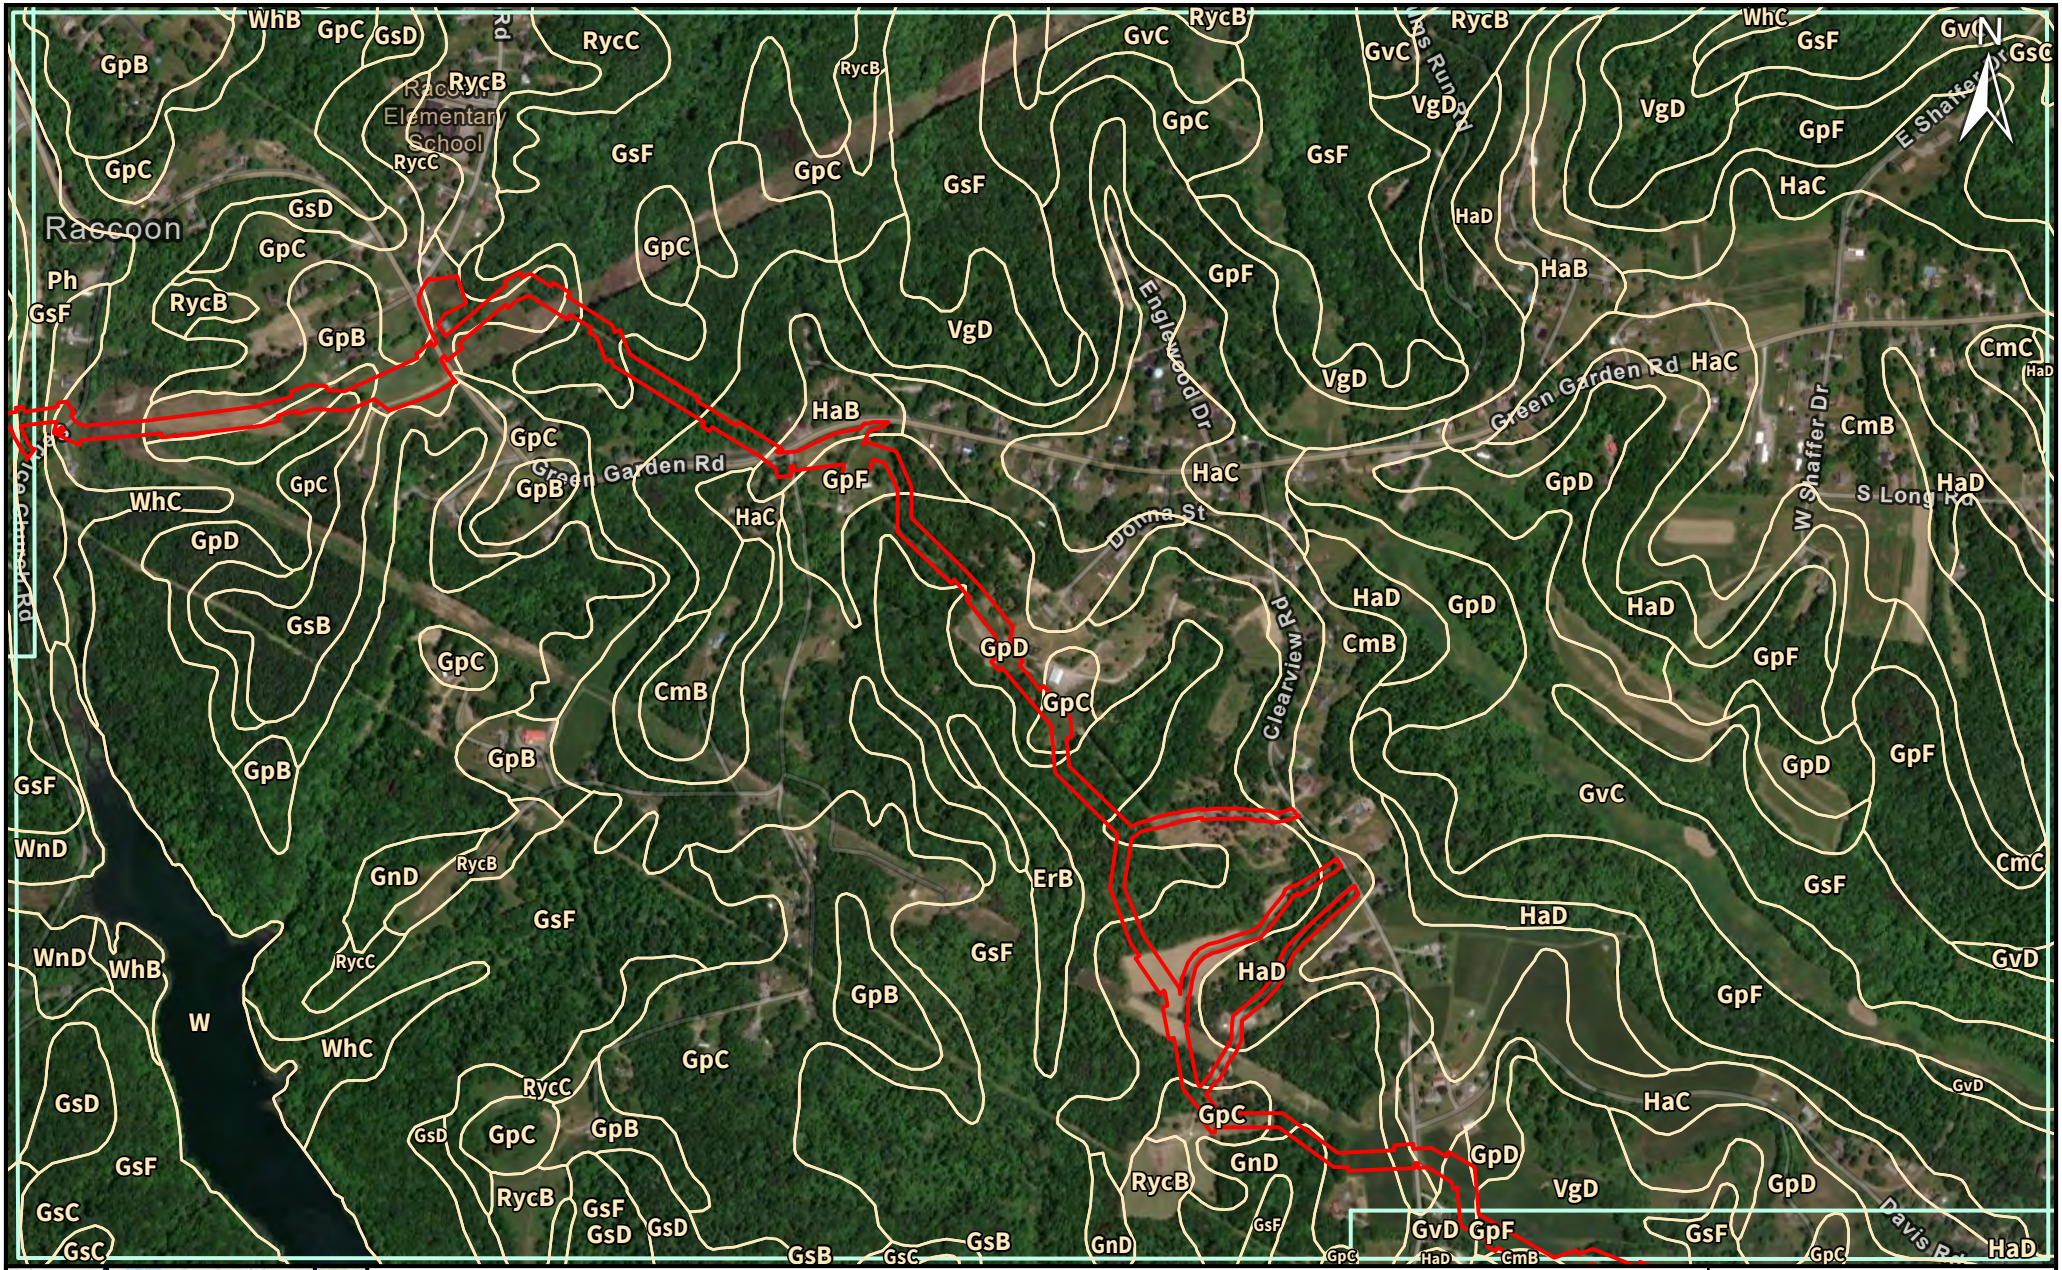

USDA NRCS Soils Map

Figure 4
Shippingport Lateral Project - LOD
Beaver County; Pennsylvania

Prepared For: National Fuel Supply Corporation

Prepared By: TETRA TECH

Cartographer: jen.laslovich

NOT FOR CONSTRUCTION

Date: 8/11/2025

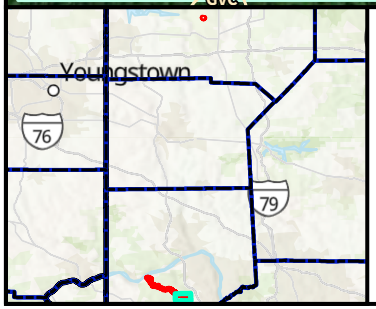

Limit of Disturbance

USDA Soil Boundary

Sheet Boundary

0 120 240
Meters

0 490 980
Feet

Scale: 1:12,000

Spatial Reference: NAD 1983 StatePlane Pennsylvania South FIPS 3702 Feet

Basemap: ESRI World Imagery (5/27/2023)

SHEET 4 OF 6

USDA NRCS Soils Map

Figure 4
Shippingport Lateral Project
Beaver County; Pennsylvania

Prepared For: National Fuel Supply Corporation

Prepared By: TETRA TECH

Cartographer: jen.laslovich

NOT FOR CONSTRUCTION

Date: 8/11/2025

Path: C:\Users\jen.laslovich\Tetra Tech, Inc\My Data Science - My PCPs\215C-DF-A0598 NFG Line NW1B\P1B.aprx

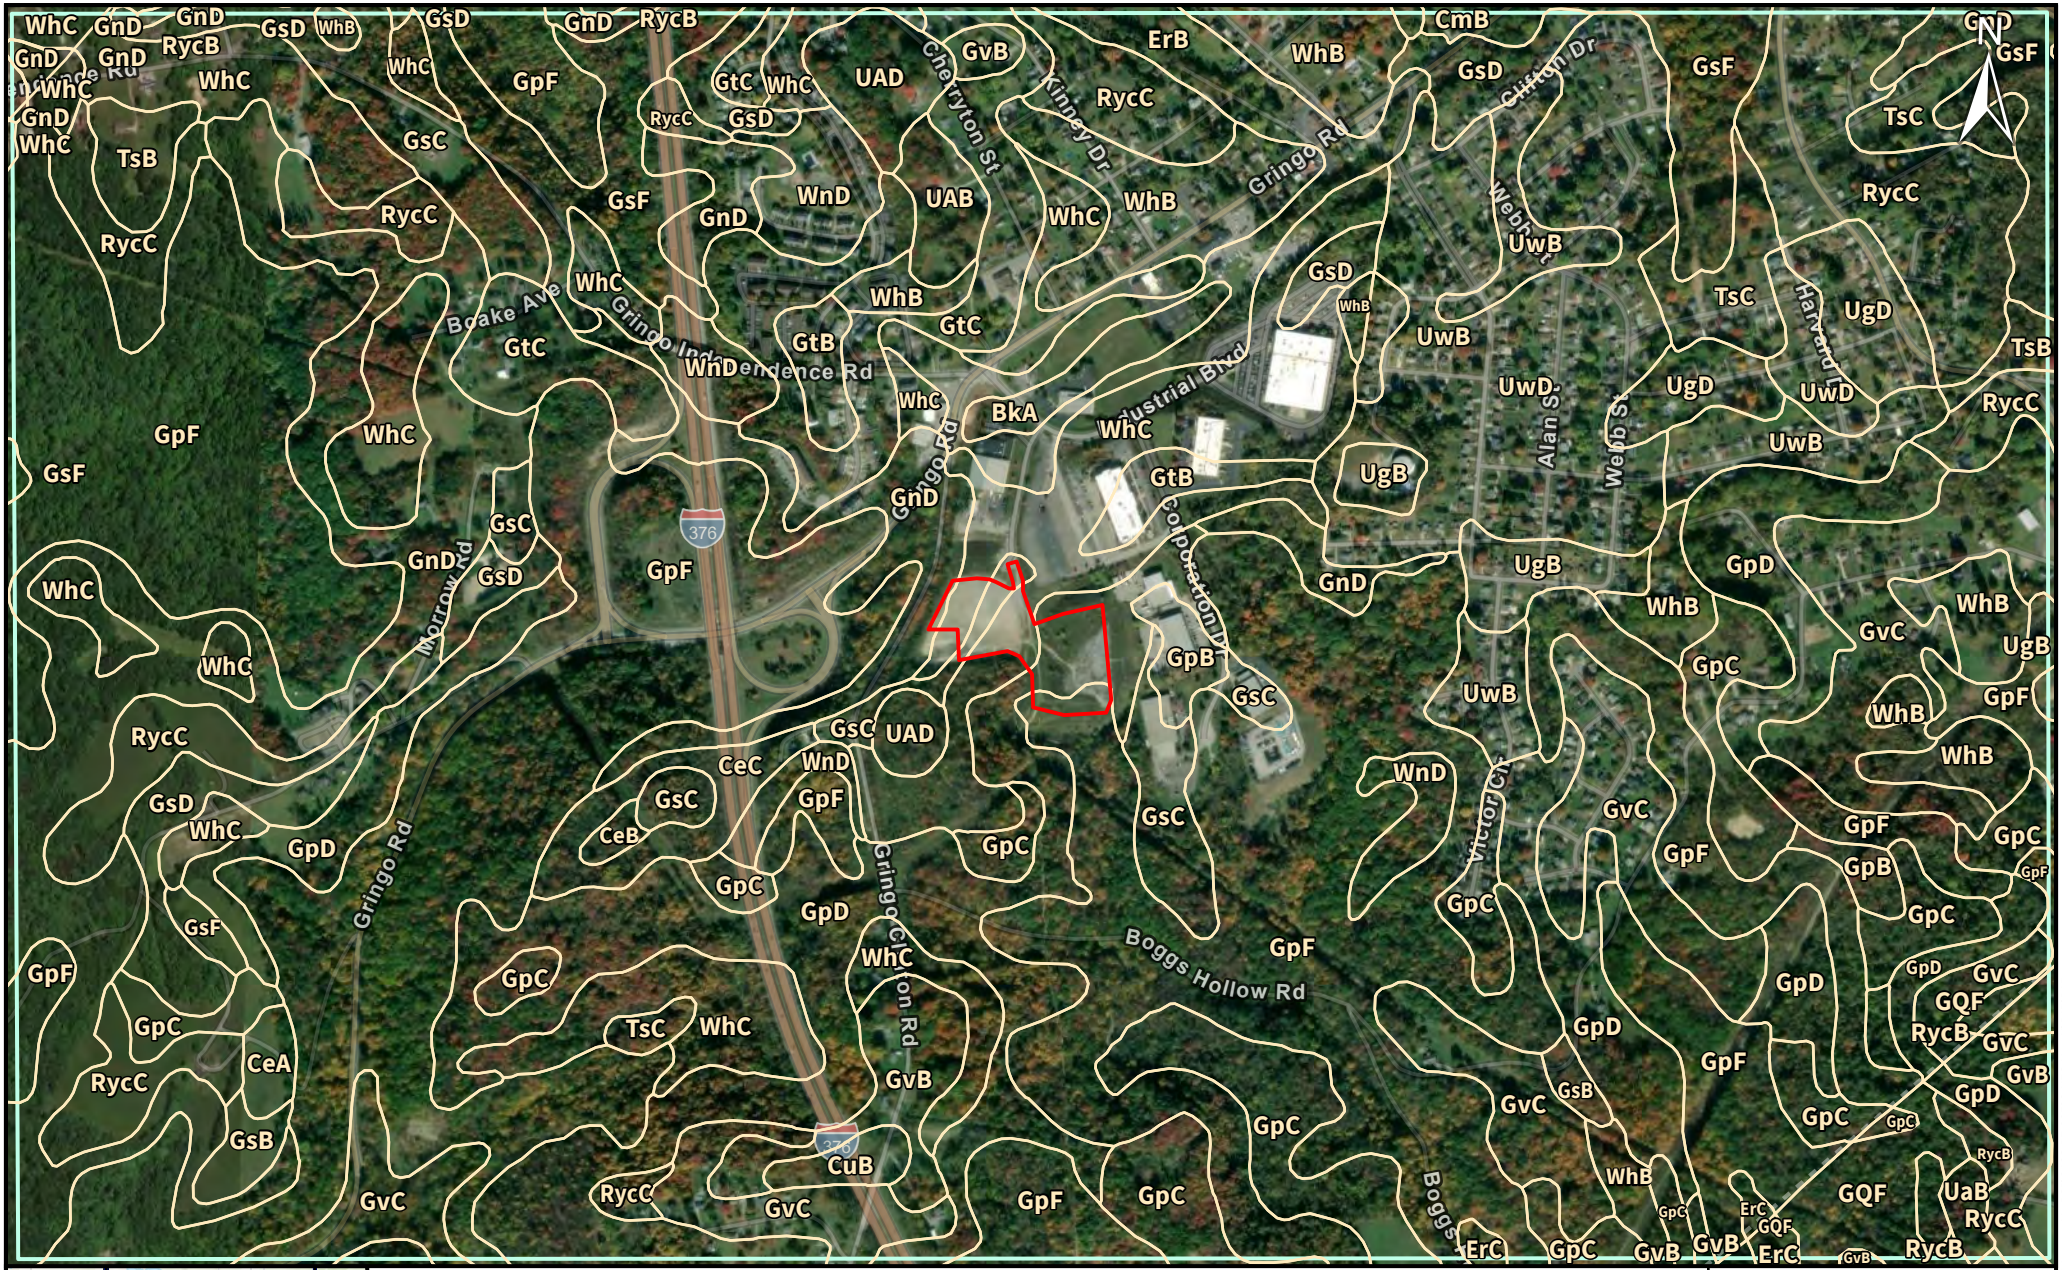

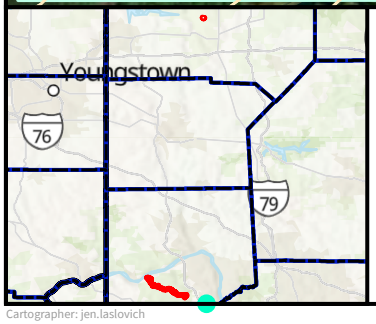

Limit of Disturbance

USDA Soil Boundary

Sheet Boundary

0 120 240
Meters

0 490 980
Feet

Scale: 1:12,000

Spatial Reference: NAD 1983 StatePlane Pennsylvania South FIPS 3702 Feet

Basemap: ESRI World Imagery (11/23/2022, 10/21/2024, 5/27/2023)

SHEET 5 OF 6

USDA NRCS Soils Map

Figure 4
Shippingport Lateral Project
Beaver County; Pennsylvania

Prepared For: National Fuel Supply Corporation

Prepared By: TETRA TECH

Cartographer: jen.laslovich

NOT FOR CONSTRUCTION

Date: 8/11/2025

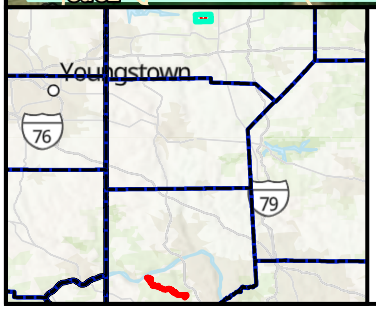

Limit of Disturbance

USDA Soil Boundary

Sheet Boundary

0 120 240
Meters

0 490 980
Feet

Scale: 1:12,000

Spatial Reference: NAD 1983 StatePlane Pennsylvania South FIPS 3702 Feet

Basemap: ESRI World Imagery (5/2/2021)

SHEET 6 OF 6

USDA NRCS Soils Map

Figure 4

Kinder Morgan OnCall Services

Mercer, Beaver County; Pennsylvania

Prepared For: National Fuel Supply Corporation

Prepared By: TETRA TECH

Cartographer: jen.laslovich

NOT FOR CONSTRUCTION

Date: 8/11/2025

Path: C:\Users\jen.laslovich\Tetra Tech, Inc\My Data Science - My PCPv21\C-BF-005598 NFG Line NW1B\P1B.aprx

Appendix A-3 – Project Construction Alignment Sheets

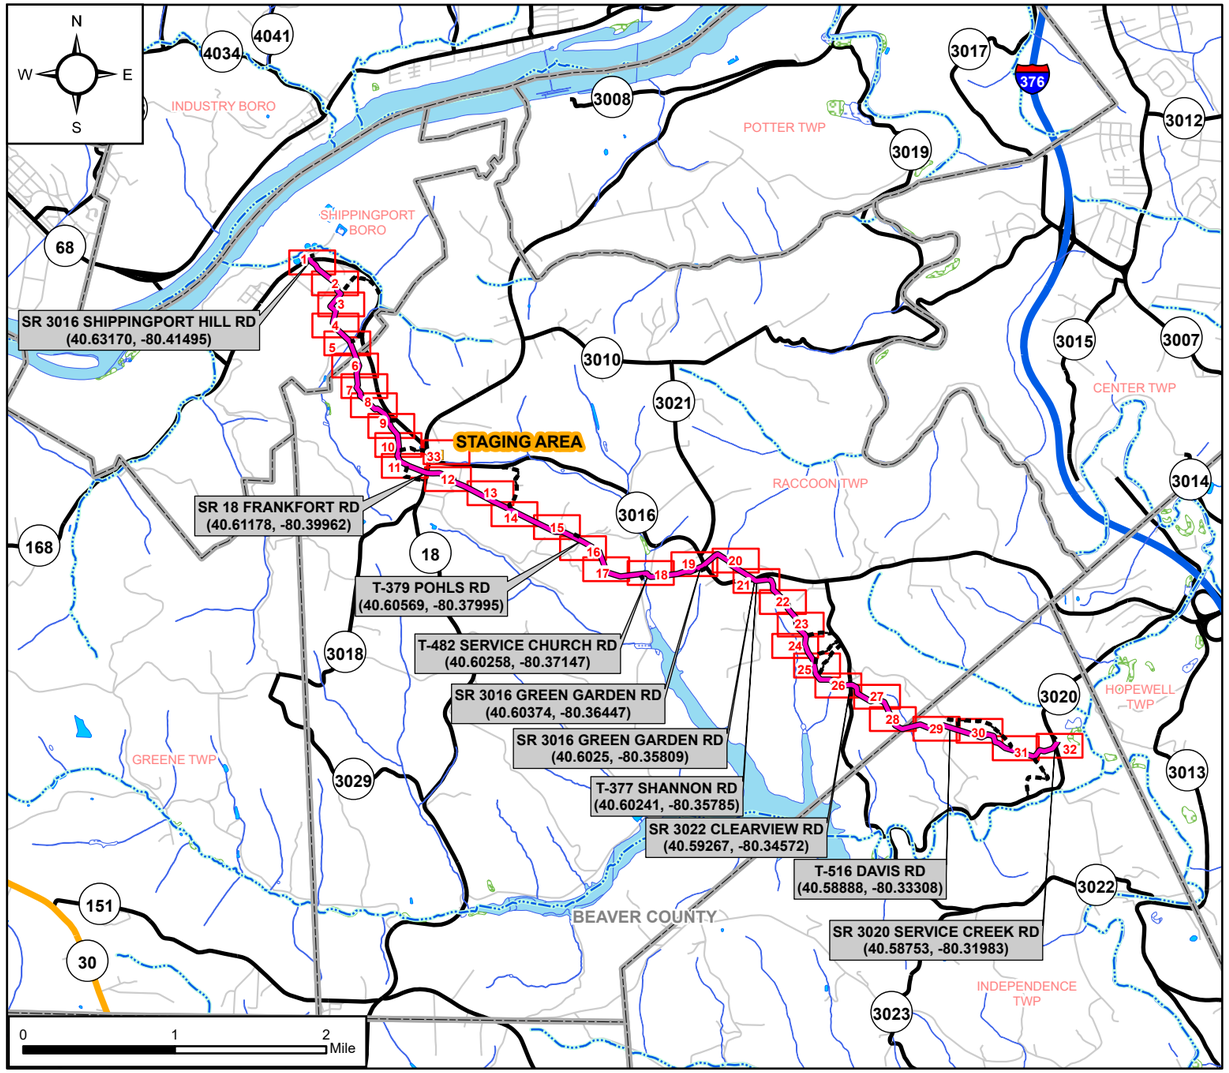

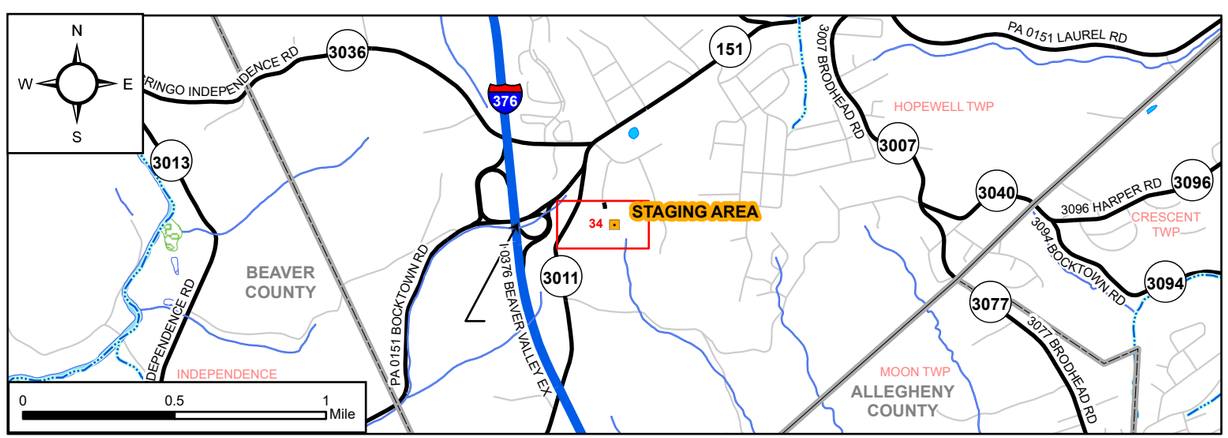

National Fuel Supply Corporation
1100 State St
Erie, PA 16501
814-871-8000
www.nationalfuelgas.com

KEYSTONE
A CLS COMPANY
680 Andersen Drive, Suite 400
Pittsburgh, PA 15220
412.278.2100
www.keystoneconsultants.net

INDEX MAP LEGEND

- Routing Map Grid
- Existing Pipelines
- State Route
- U.S Route
- Interstate Road
- Local Roads
- Streams
- Freshwater Emergent Wetland
- Freshwater Forested/Shrub Wetland
- Freshwater Pond
- River
- Municipal Boundary
- Proposed Pipeline

FERC MAP LEGEND

- Telephone Box
- Bush/ Shrub
- Cleanout
- Utility Line Marker
- Electric Meter
- Water Meter
- Gas Vault
- Wood Post
- Rectifier Pole
- Utility Pole
- Sign
- Bollard
- Manhole
- Fence Post
- Property Monument
- Gas Test Station
- Deciduous Tree
- Pine Tree
- Fence Line
- Unpaved Driveway
- Paved Driveway
- Road Edges
- Guiderail
- Existing Pipelines (Survey)
- Rip Rap
- Planter
- Treeline
- Brushline
- Field Edge
- Contours (20ft)
- Stations Even 200ft
- Milepost (0.5 Mile)
- Gas Riser
- Mailbox
- Hydrant
- Water Well
- Water Valve
- Water Box
- Telephone Manhole
- Storm and Sanitary Manhole
- Electric Manhole
- Gas Meter
- Gas Box
- Gas Well
- Electric Box
- Ground Light
- Light Standard
- Catch Basin
- Waterline
- Sanitary Sewer Line
- Storm Drain - Culvert
- Overhead Wire
- Underground Telephone Cable Line
- Underground Electric Line
- Guy Wire
- Top Wall
- Steps
- Parcel Boundary
- Matchline
- Electrical Transmission Easement
- Limit of Disturbance
- Permanent Right-of-Way
- Temporary Workspace
- Additional Temporary Workspace

Data Provided by Others

- Proposed Pipeline
- Staging Area
- Water Conveyance
- PEM Delineated Wetlands
- PFO Wetlands Delineated
- PSS Wetlands Delineated
- Pond
- Delineated Streams
- Environmental AOI
- FEMA Floodplain (Zone A)
- Waterline (GPR)
- Electric Utility (GPR)
- Gasline (GPR)

Note:
Utilities Shown on these Maps are from Various Sources and have not been Field Verified for Accuracy or Location.

SOURCES:

Parcels
Parcels were Supplied by NFG.

Delineated Streams and Wetlands
Streams and Wetlands Delineated by Tetra Tech

Mapped Streams
National Hydrography Dataset (NHD)
U.S. Geological Survey in cooperation with U.S. Environmental Protection Agency, USDA Forest Service, and other Federal, State and local partners
http://www.nhd.usgs.gov

Wetlands
U. S. Fish and Wildlife Service. October 01, 2014. National Wetlands Inventory website. U.S. Department of the Interior, Fish and Wildlife Service, Washington, D.C.
http://www.fws.gov/wetlands/

Contours (20' Interval)
PAMAP Program, PA Department of Conservation and Natural Resources, Bureau of Topographic and Geologic Survey
http://www.dcnr.state.pa.us/topogeo/pamap

Roads
PAMAP Program, PA Department of Conservation and Natural Resources, Bureau of Topographic and Geologic Survey
http://www.dcnr.state.pa.us/topogeo/pamap

Aerial Imagery
Kucera Aerial Imagery July 2025, and PEMA 2018 Aerial Imagery.

811 Know what's below. Call before you dig.

These maps have been provided as a tool to assist the contractor in building the pipeline. National Fuel/Keystone Consultants, LLC has made reasonable efforts to provide this information and verify its accuracy; however, the contractor shall not rely solely on the information provided. National Fuel/Keystone Consultants, LLC recommends that the contractor perform their own due diligence to determine the location of underground facilities, including the appropriate state One Call, etc. National Fuel/Keystone Consultants, LLC makes no warranty regarding the completeness or accuracy of the information provided.

ISSUED FOR FERC

National Fuel Supply Corporation
National Fuel Supply Corporation
Shippingport Lateral Project

REV	DRAWN BY : KEYSTONE CONSULTANTS. LLC	INDEX SHEET
P	CHECKED BY : D. MCINTIRE	
	SCALE : 1 = 1 MI	
	DATE : 8/21/2025	

T:\Projects\2025\00180.25.25\GIS\Maps\Line N Lateral Project\Line N Lateral Project.aprx

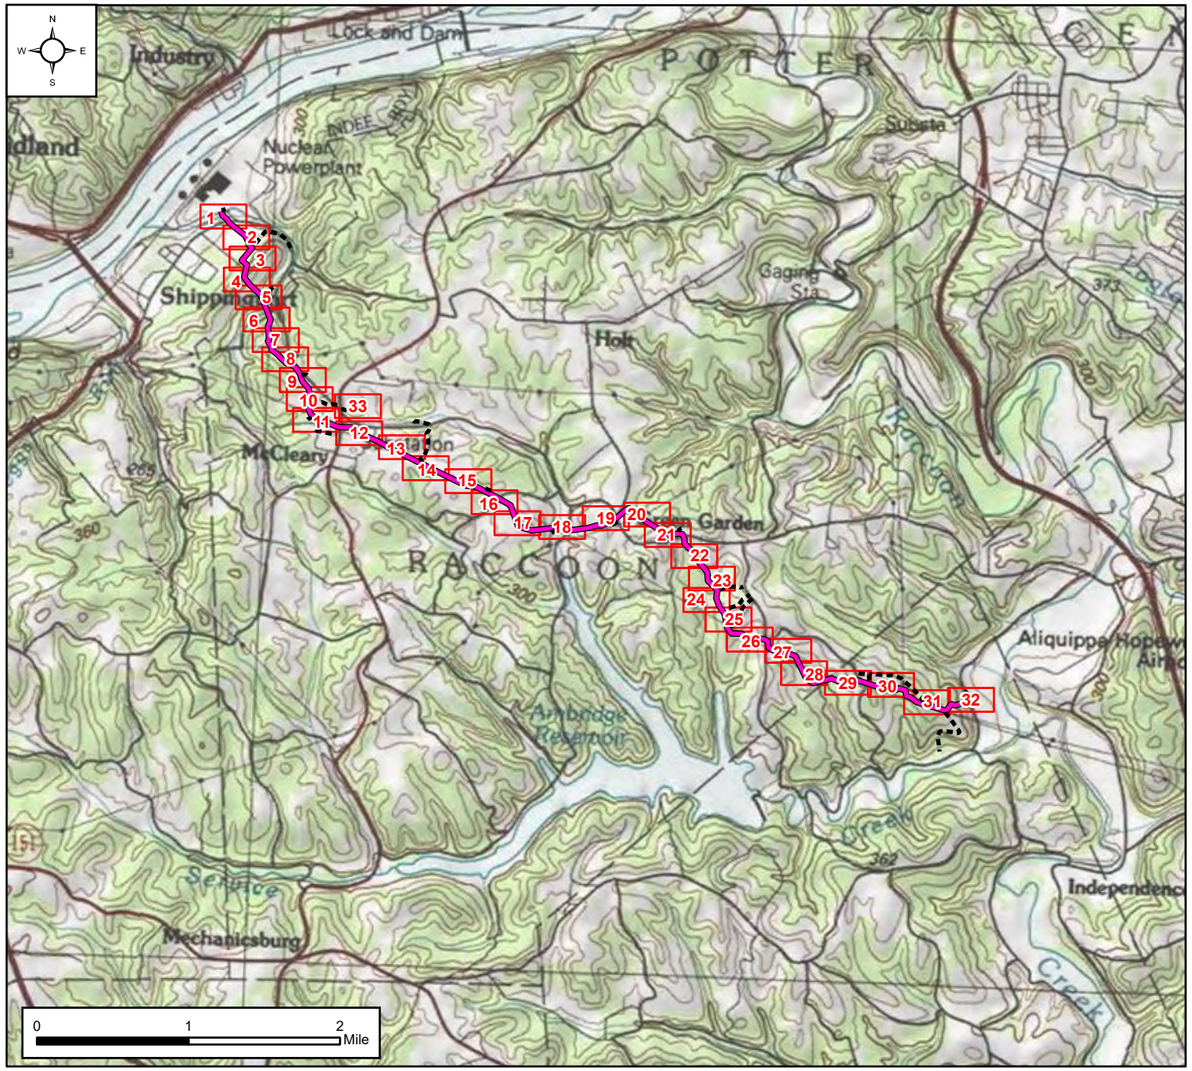

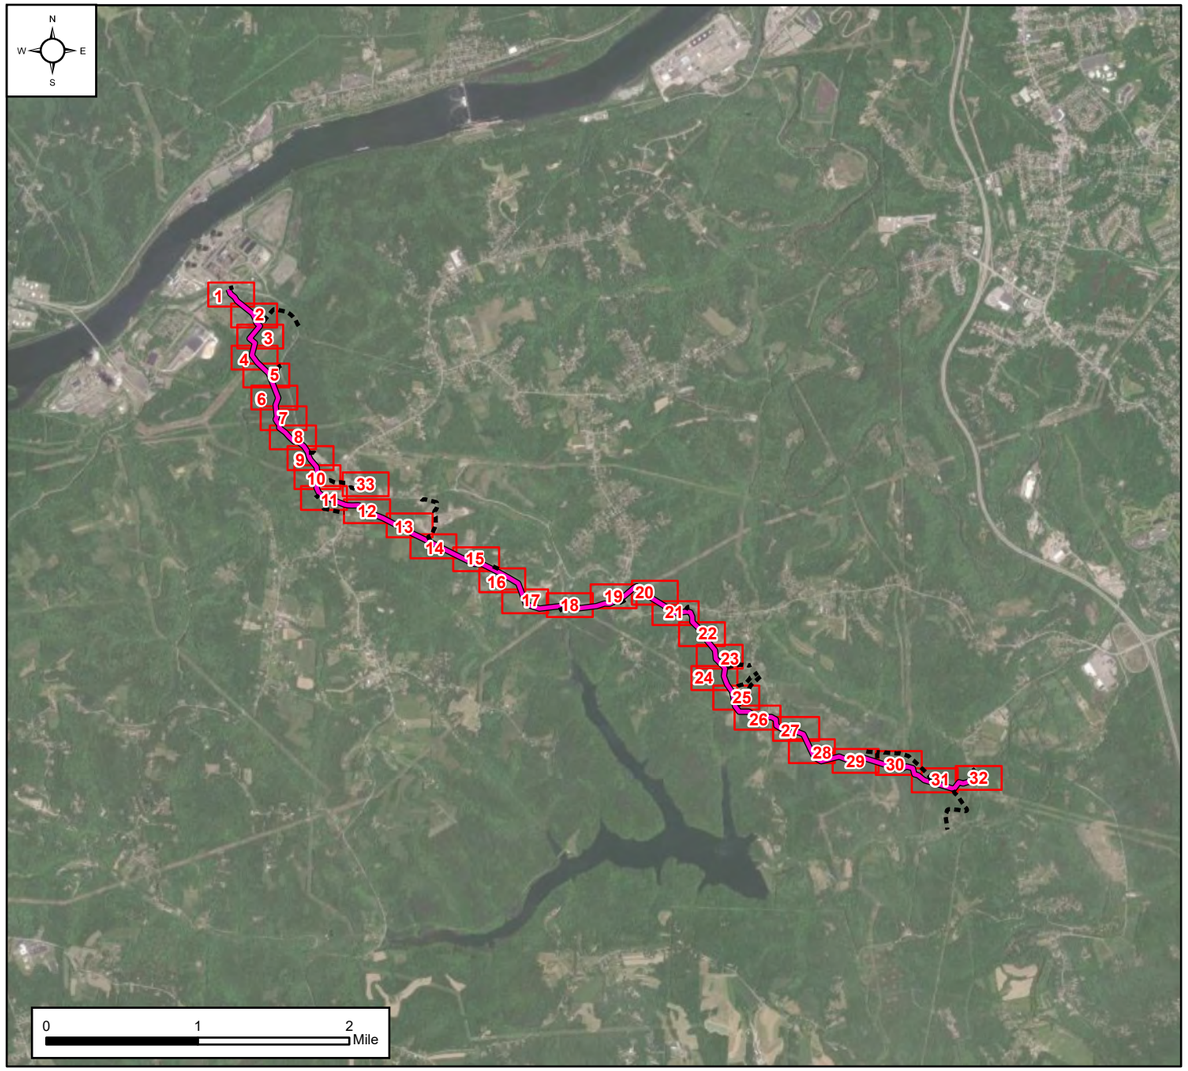

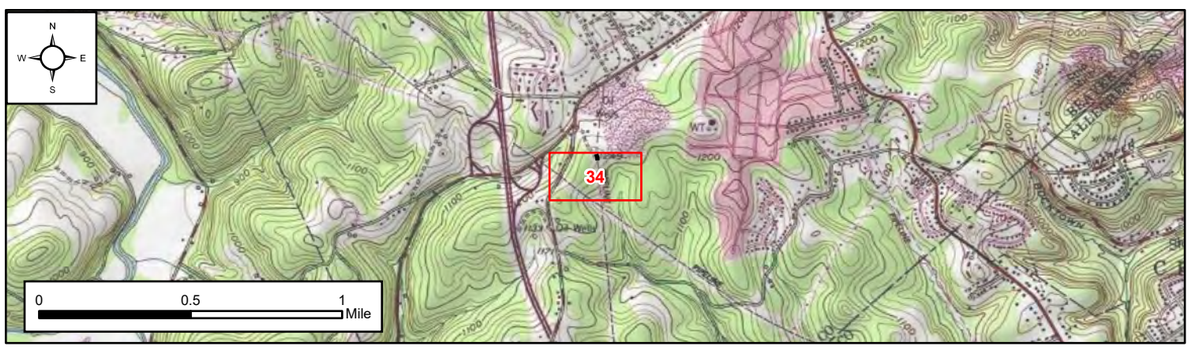

ISSUED FOR FERC

National Fuel®
Supply Corporation
National Fuel Supply Corporation
Shippingport Lateral Project

REV		
P	DRAWN BY :	KEYSTONE CONSULTANTS. LLC
	CHECKED BY :	D. MCINTIRE
	SCALE :	1 =1 mi
	DATE :	8/21/2025

SECTION
TOPO
SHEET

T:\Projects\2025\00180.25.25\GIS\Maps\Line N Lateral Project\Line N Lateral Project.aprx

REV	STATUS	DESCRIPTION	DATE
A	IFR	COMPILIED GIS BASEMAP AND ADDED WORSPACE FEATURES	2/10/2025
B	IFR	REVISED ROUTES + ADDED SURVEY DATA	3/24/2025
C	IFR	ADDED FIELD ROUTED PIPELINES	3/26/2025
D	IFR	REVISED ROUTES + ADDED SURVEY DATA	4/7/2025
E	IFR	REVISED ROUTES, ADDED LOD + ADDED SURVEY DATA	4/14/2025
F	IFR	REVISED ROUTES, ADDED LOD + ADDED SURVEY DATA	4/21/2025
G	IFR	REVISED LOD, REVISED ACCESS ROADS, + ADDED ENVIRONMENTAL DATA	5/5/2025
H	IFR	REVISED LOD, REVISED ACCESS ROADS, + ADDED ENVIRONMENTAL DATA	5/14/2025
J	IFR	REVISED LOD, REVISED ACCESS ROADS, + ADDED ENVIRONMENTAL DATA	6/5/2025
K	IFR	REVISED LOD AND TWS	6/9/2025
L	IFF	REVISED PAR AND TAR + STATION AREAS	6/12/2025
M	IFB	ADDED SINGLE LINE DIAGRAM + ISSUED MAPSET FOR BID	7/25/2025
N	IFF	ISSUED MAPSET FOR FERC	8/12/2025
P	IFF	SMYBOLOGY ADJUSTMENTS ON MAPSET	8/21/2025

IFR = ISSUED FOR REVIEW
IFB = ISSUED FOR BID
IFC = ISSUED FOR CONSTRUCTION
IFF = ISSUED FOR FERC

Know what's below. Call before you dig.

STOP! CALL BEFORE YOU DIG! 811 OR 1-800-242-1776

PENNSYLVANIA ACT 287 REQUIRES:

A DESIGN ONE CALL TO BE PLACED NOT LESS THAN 10 OR MORE THAN 90 BUSINESS DAYS BEFORE FINAL DESIGN IS TO BE COMPLETED.

DESIGN ONE CALL DATE: 2/3/2025

DESIGN ONE CALL NUMBERS: 20250342083-000

SHIPPINGPORT BOROUGH, BEAVER COUNTY

BUCKEYE PARTNERS
- ENGINEERING COMPLETED.
COMCAST CABLE COMMUNICATIONS INC
-NO RESPONSE
DUQUESNE LIGHT COMPANY
- CLEAR NO FACILITIES
MARATHON PIPELINE LLC
- Conflict, KMZs sent
PEOPLES GAS COMPANY LLC
- CLEAR NO FACILITIES
SHIPPINGPORT BOROUGH
- CLEAR NO FACILITIES

PENNSYLVANIA ACT 287 REQUIRES:

A DESIGN ONE CALL TO BE PLACED NOT LESS THAN 10 OR MORE THAN 90 BUSINESS DAYS BEFORE FINAL DESIGN IS TO BE COMPLETED.

DESIGN ONE CALL DATE: 2/3/2025

DESIGN ONE CALL NUMBERS: 20250342084-000

RACCOON TOWNSHIP, BEAVER COUNTY

ALIQUIPPA MUNICIPAL WATER AUTHORITY
- FIELD MARKED.
BUCKEYE PARTNERS
-PDF SENT
DUQUESNE LIGHT COMPANY
CLEAR NO FACILITIES
MARATHON PIPELINE LLC
-CONFLICT, KMZs SENT
MESSER/LINDE LLC/BOC GAS
- FIELD MARKED.
PEOPLES GAS COMPANY LLC
- CLEAR NO FACILITIES
RACCOON TOWNSHIP
-CLEAR NO FACILITIES
SHELL PIPELINE COMPANY
- PDF SENT

PENNSYLVANIA ACT 287 REQUIRES:

A DESIGN ONE CALL TO BE PLACED NOT LESS THAN 10 OR MORE THAN 90 BUSINESS DAYS BEFORE FINAL DESIGN IS TO BE COMPLETED.

DESIGN ONE CALL DATE: 2/3/2025

DESIGN ONE CALL NUMBERS: 20250342101-000

RACCOON TOWNSHIP, BEAVER COUNTY

ALIQUIPPA MUNICIPAL WATER AUTHORITY
- FIELD MARKED.
BUCKEYE PARTNERS
-PDF SENT
COMCAST CABLE
-NO RESPONSE
DUQUESNE LIGHT COMPANY
CLEAR NO FACILITIES
MARATHON PIPELINE LLC
-CONFLICT, KMZs SENT
RACCOON TOWNSHIP
-CLEAR NO FACILITIES
SHELL PIPELINE COMPANY
- PDF SENT

PENNSYLVANIA ACT 287 REQUIRES:

A DESIGN ONE CALL TO BE PLACED NOT LESS THAN 10 OR MORE THAN 90 BUSINESS DAYS BEFORE FINAL DESIGN IS TO BE COMPLETED.

DESIGN ONE CALL DATE: 2/3/2025

DESIGN ONE CALL NUMBERS: 20250342115-000

RACCOON TOWNSHIP, BEAVER COUNTY

BUCKEYE PARTNERS
-PDF SENT
COMCAST CABLE
-NO RESPONSE
DUQUESNE LIGHT COMPANY
CLEAR NO FACILITIES
MARATHON PIPELINE LLC
-CONFLICT, KMZs SENT
RACCOON TOWNSHIP
-CLEAR NO FACILITIES
VERIZON PENNSYLVANIA INC
-CLEAR NO FACILITIES

PENNSYLVANIA ACT 287 REQUIRES:

A DESIGN ONE CALL TO BE PLACED NOT LESS THAN 10 OR MORE THAN 90 BUSINESS DAYS BEFORE FINAL DESIGN IS TO BE COMPLETED.

DESIGN ONE CALL DATE: 2/3/2025

DESIGN ONE CALL NUMBERS: 20250342128-000

RACCOON TOWNSHIP, BEAVER COUNTY

BUCKEYE PARTNERS
-PDF SENT
COMCAST CABLE
-NO RESPONSE
DUQUESNE LIGHT COMPANY
-CLEAR NO FACILITIES
RACCOON TOWNSHIP
-CLEAR NO FACILITIES
VERIZON PENNSYLVANIA INC
-CLEAR NO FACILITIES

PENNSYLVANIA ACT 287 REQUIRES:

A DESIGN ONE CALL TO BE PLACED NOT LESS THAN 10 OR MORE THAN 90 BUSINESS DAYS BEFORE FINAL DESIGN IS TO BE COMPLETED.

DESIGN ONE CALL DATE: 2/3/2025

DESIGN ONE CALL NUMBERS: 20250342148-000

RACCOON TOWNSHIP, BEAVER COUNTY

ALIQUIPPA MUNICIPAL WATER AUTHORITY
- FIELD MARKED.
BUCKEYE PARTNERS
-CLEAR NO FACILITIES
COMCAST CABLE
-NO RESPONSE
DUQUESNE LIGHT COMPANY
-CLEAR NO FACILITIES
MARKWEST LIBERTY MIDSTREAM AND RESOURCES
-CLEAR NO FACILITIES
RACCOON TOWNSHIP
-CLEAR NO FACILITIES
VERIZON PENNSYLVANIA INC
-CLEAR NO FACILITIES

PENNSYLVANIA ACT 287 REQUIRES:

A DESIGN ONE CALL TO BE PLACED NOT LESS THAN 10 OR MORE THAN 90 BUSINESS DAYS BEFORE FINAL DESIGN IS TO BE COMPLETED.

DESIGN ONE CALL DATE: 2/3/2025

DESIGN ONE CALL NUMBERS: 20250342223-000

RACCOON TOWNSHIP, BEAVER COUNTY

BUCKEYE PARTNERS
-PDF SENT
COMCAST CABLE
-NO RESPONSE
DUQUESNE LIGHT COMPANY
-CLEAR NO FACILITIES
MARKWEST LIBERTY MIDSTREAM AND RESOURCES
-CLEAR NO FACILITIES
RACCOON TOWNSHIP
-CLEAR NO FACILITIES
SUNOCO PIPELINE LP
-CLEAR NO FACILITIES
VERIZON PENNSYLVANIA INC
-CLEAR NO FACILITIES

PENNSYLVANIA ACT 287 REQUIRES:

A DESIGN ONE CALL TO BE PLACED NOT LESS THAN 10 OR MORE THAN 90 BUSINESS DAYS BEFORE FINAL DESIGN IS TO BE COMPLETED.

DESIGN ONE CALL DATE: 2/3/2025

DESIGN ONE CALL NUMBERS: 20250342224-000

INDEPENDENCE TOWNSHIP, BEAVER COUNTY

BUCKEYE PARTNERS
-PDF SENT
DUQUESNE LIGHT COMPANY
-CLEAR NO FACILITIES
ENERGY TRANSFER
-CONFLICT – PDFS SENT
INDEPENDENCE TOWNSHIP BEAVER COUNTY
-CLEAR NO FACILITIES
MARKWEST LIBERTY MIDSTREAM AND RESOURCES
-CLEAR NO FACILITIES
SUNOCO PIPELINE LP
-CLEAR NO FACILITIES
VERIZON PENNSYLVANIA INC
-CLEAR NO FACILITIES

PENNSYLVANIA ACT 287 REQUIRES:

A DESIGN ONE CALL TO BE PLACED NOT LESS THAN 10 OR MORE THAN 90 BUSINESS DAYS BEFORE FINAL DESIGN IS TO BE COMPLETED.

DESIGN ONE CALL DATE: 2/3/2025

DESIGN ONE CALL NUMBERS: 20250342239-000

INDEPENDENCE TOWNSHIP, BEAVER COUNTY

AMBRIDGE WATER AUTHORITY
-FIELD MARKED
BUCKEYE PARTNERS
-PDF SENT
DUQUESNE LIGHT COMPANY
-CLEAR NO FACILITIES
ENERGY TRANSFER
-CONFLICT – PDFS SENT
INDEPENDENCE TOWNSHIP BEAVER COUNTY
-CLEAR NO FACILITIES
MARKWEST LIBERTY MIDSTREAM AND RESOURCES
-CLEAR NO FACILITIES
NATIONAL FUEL GAS SUPPLY
-CONFLICT MAPS SENT
SHELL PIPELINE
-PDF SENT
SUNOCO PIPELINE LP
-CLEAR NO FACILITIES
VERIZON PENNSYLVANIA INC
-CLEAR NO FACILITIES

PENNSYLVANIA ACT 287 REQUIRES:

A DESIGN ONE CALL TO BE PLACED NOT LESS THAN 10 OR MORE THAN 90 BUSINESS DAYS BEFORE FINAL DESIGN IS TO BE COMPLETED.

DESIGN ONE CALL DATE: 2/3/2025

DESIGN ONE CALL NUMBERS: 20250371301-000

SHIPPINGPORT BOROUGH, BEAVER COUNTY

DUQUESNE LIGHT COMPANY
-CLEAR NO FACILITIES
PEOPLES GAS
-PDFS SENT
SHIPPINGPORT BOROUGH
-CONFLICT, KMZs SENT

ISSUED FOR FERC

National Fuel Supply Corporation
National Fuel Supply Corporation
Shippingport Lateral Project

REV		
P	DRAWN BY :	KEYSTONE CONSULTANTS. LLC
	CHECKED BY :	D. MCINTIRE
	SCALE :	1 INCH = 0 FEET
	DATE :	8/21/2025

SECTION
PA ONE CALL

PIPELINE

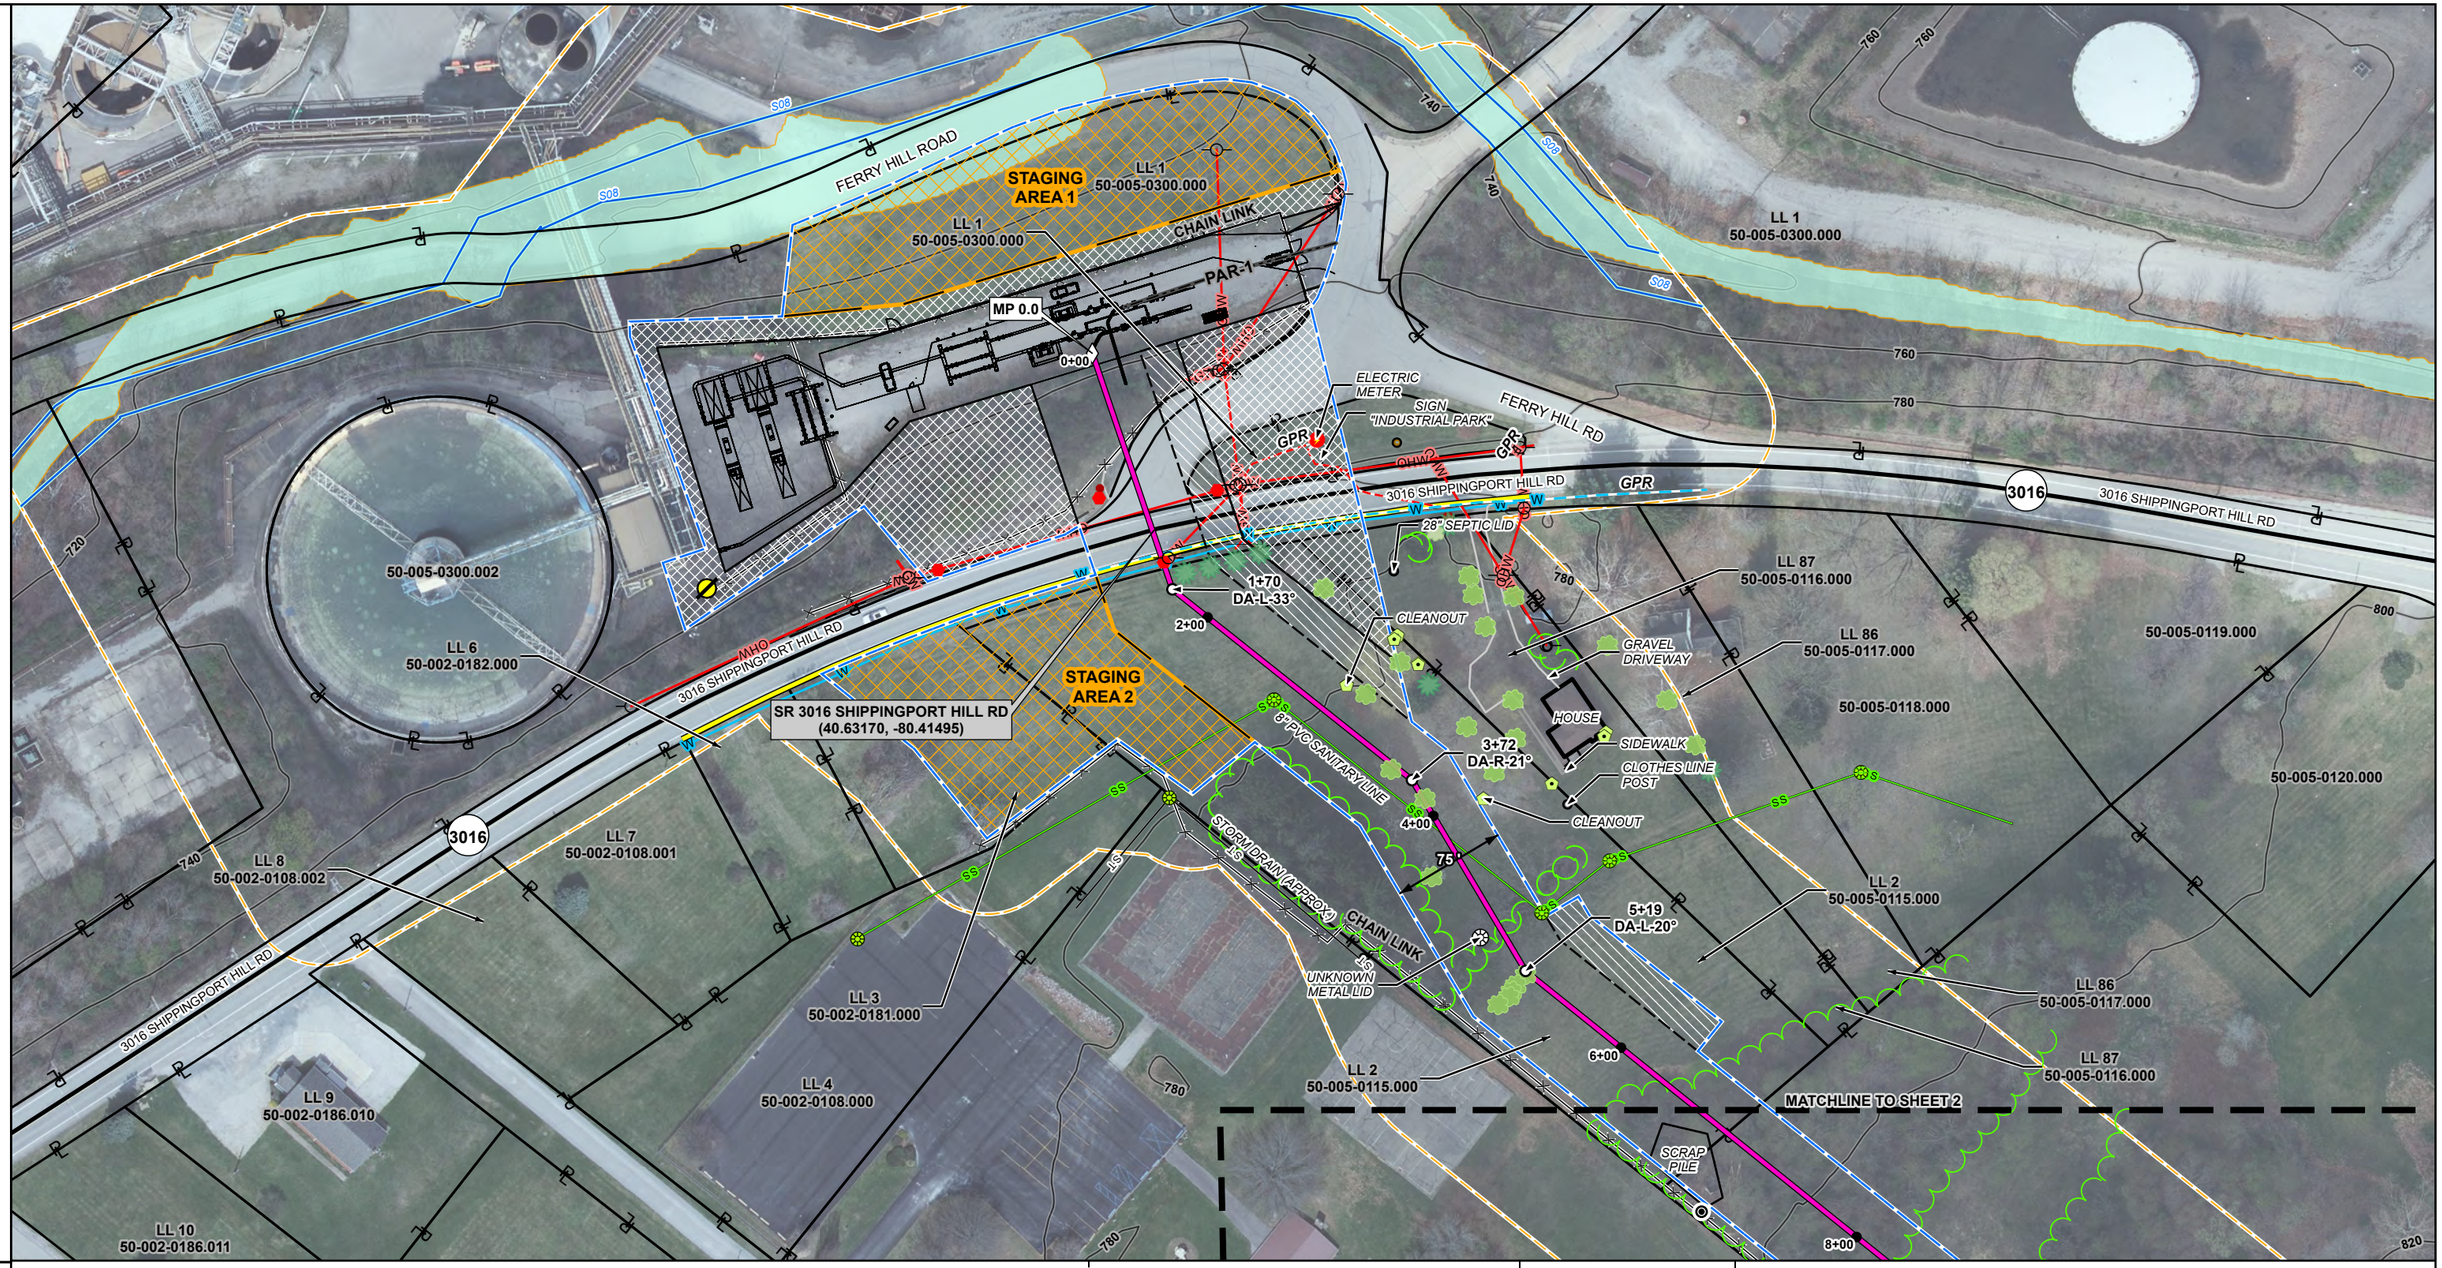

	0+00 BEGIN PROPOSED PIPELINE		1+70		6+66 MATCHLINE
FOOTAGE		170'		496'	
WALL THICKNESS		24"-0.562WT		24"-0.562WT	
GRADE		X-65		X-65	
COATING		PWR		FBE	

N W E S

ISSUED FOR FERC

National Fuel® Supply Corporation

0 100 200 Feet

National Fuel Supply Corporation
Shippingport Lateral Project

Shippingport Borough
Beaver County
Pennsylvania

REV
P

DRAWN BY : KEYSTONE CONSULTANTS. LLC
CHECKED BY : D. MCINTIRE
SCALE : 1 =100 feet
DATE : 8/21/2025

1
34

PIPELINE

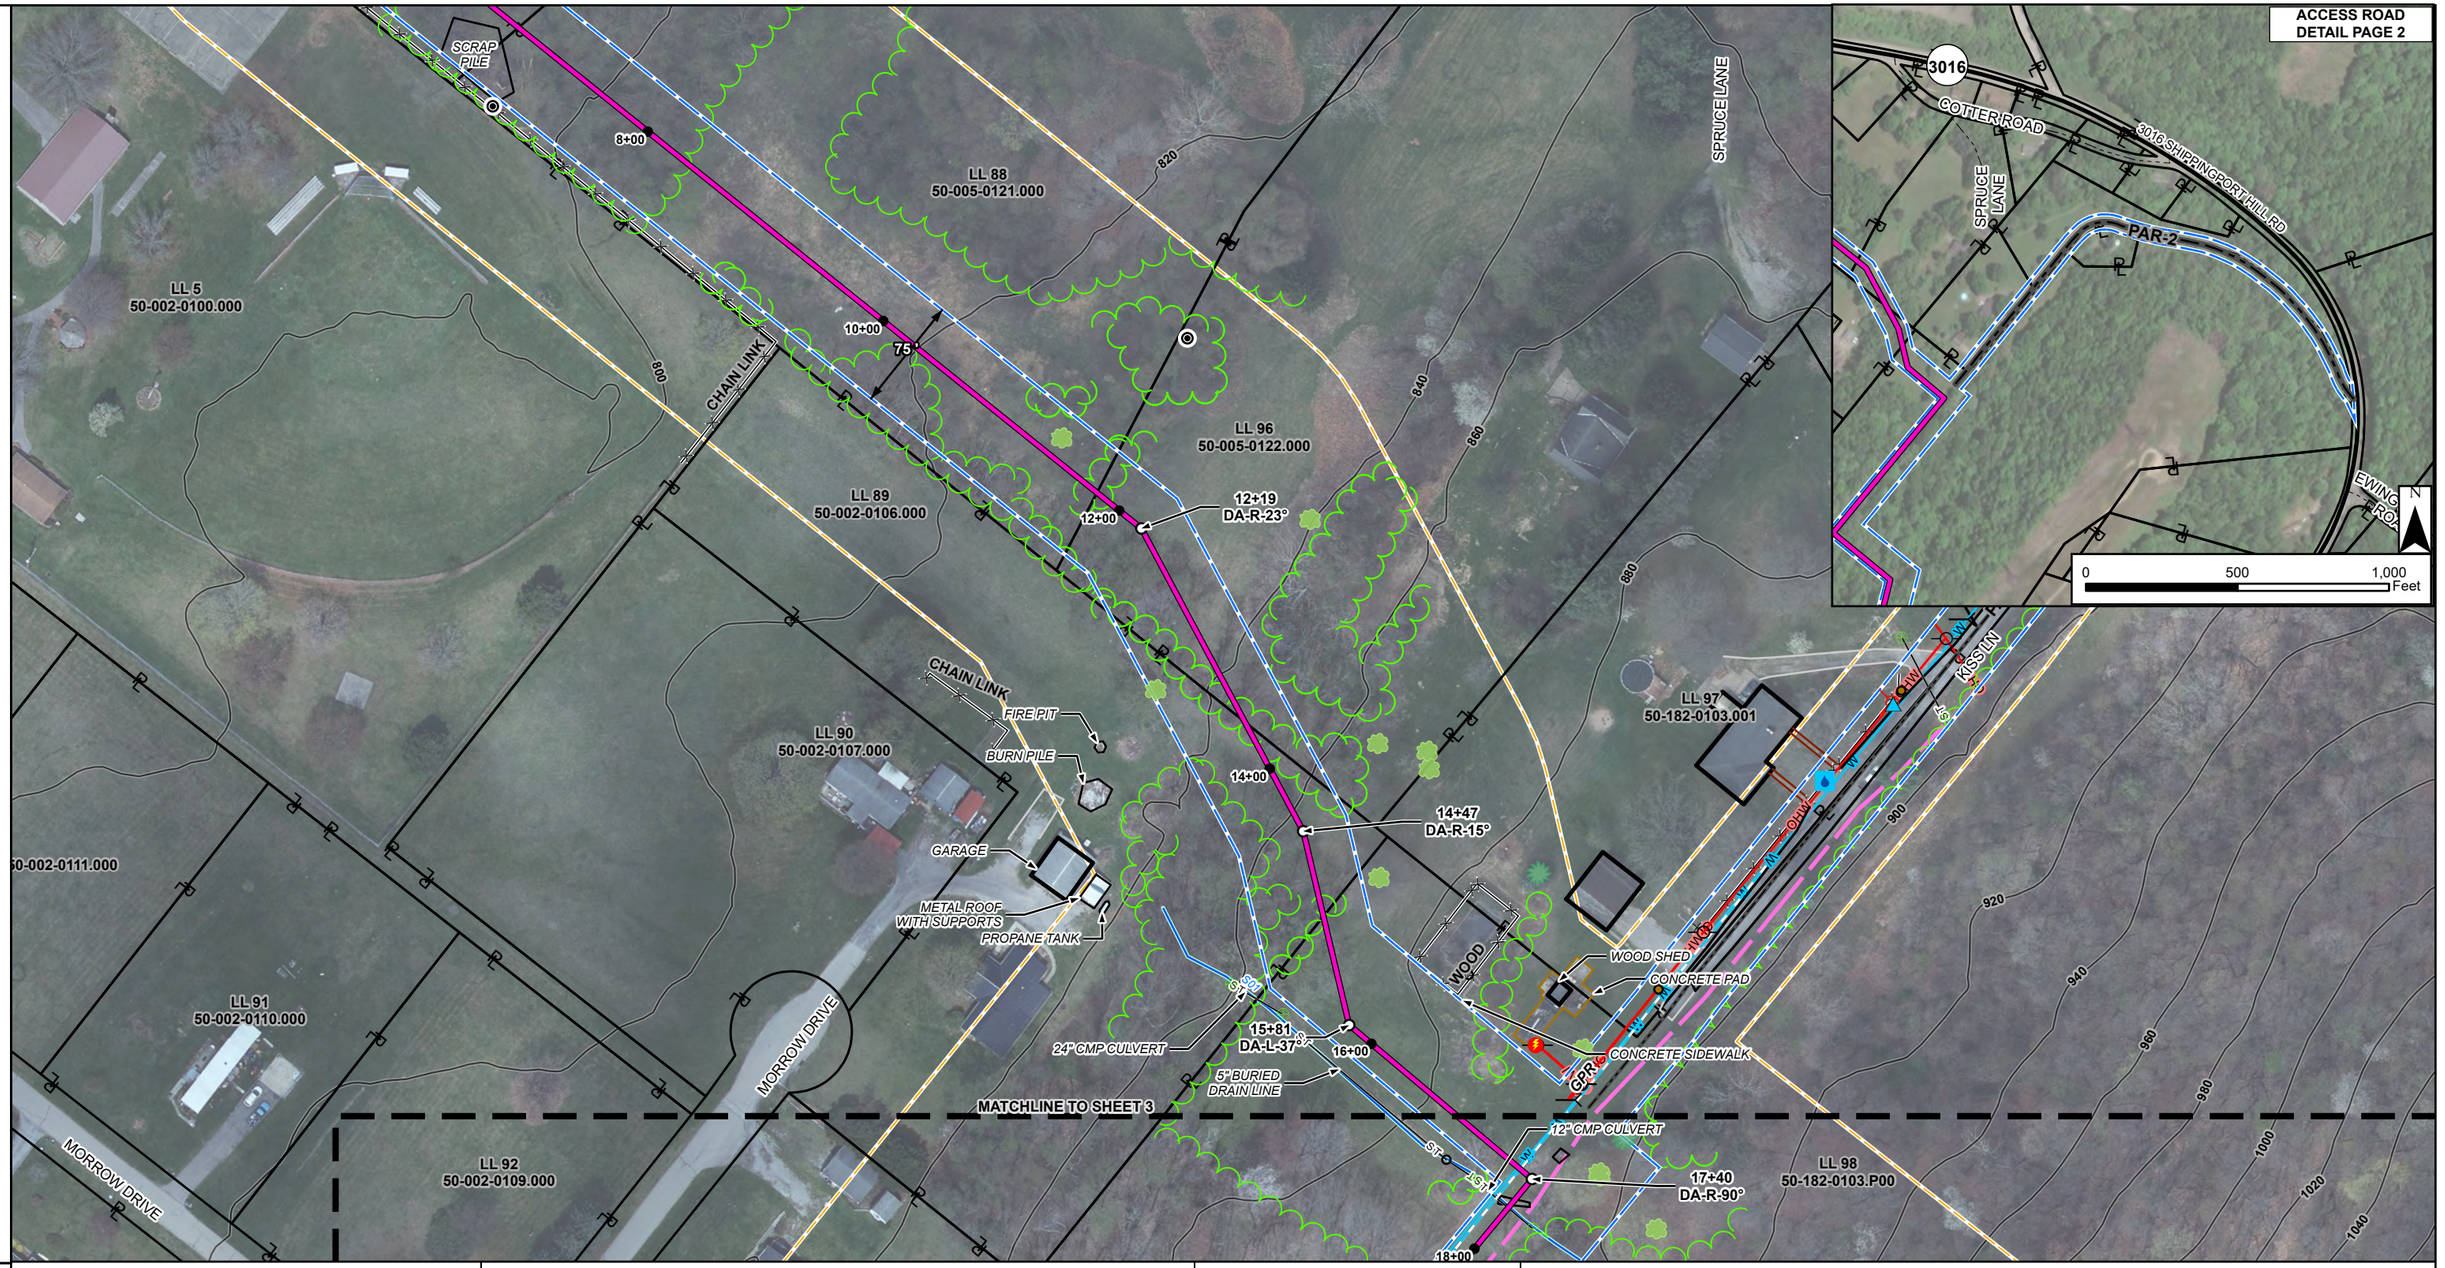

FOOTAGE		614'	395'	
WALL THICKNESS	6+66 MATCHLINE	24"-0.562WT	24"-0.500WT	16+75 MATCHLINE
GRADE	12+80	X-65	X-65	
COATING		FBE	FBE	

N W E S

ISSUED FOR FERC

National Fuel® Supply Corporation

0 100 200 Feet

National Fuel Supply Corporation
Shippingport Lateral Project

Shippingport Borough
Beaver County
Pennsylvania

REV	DRAWN BY : KEYSTONE CONSULTANTS. LLC	2
	CHECKED BY : D. MCINTIRE	
P	SCALE : 1 =100 feet	34
	DATE : 8/21/2025	

PIPELINE

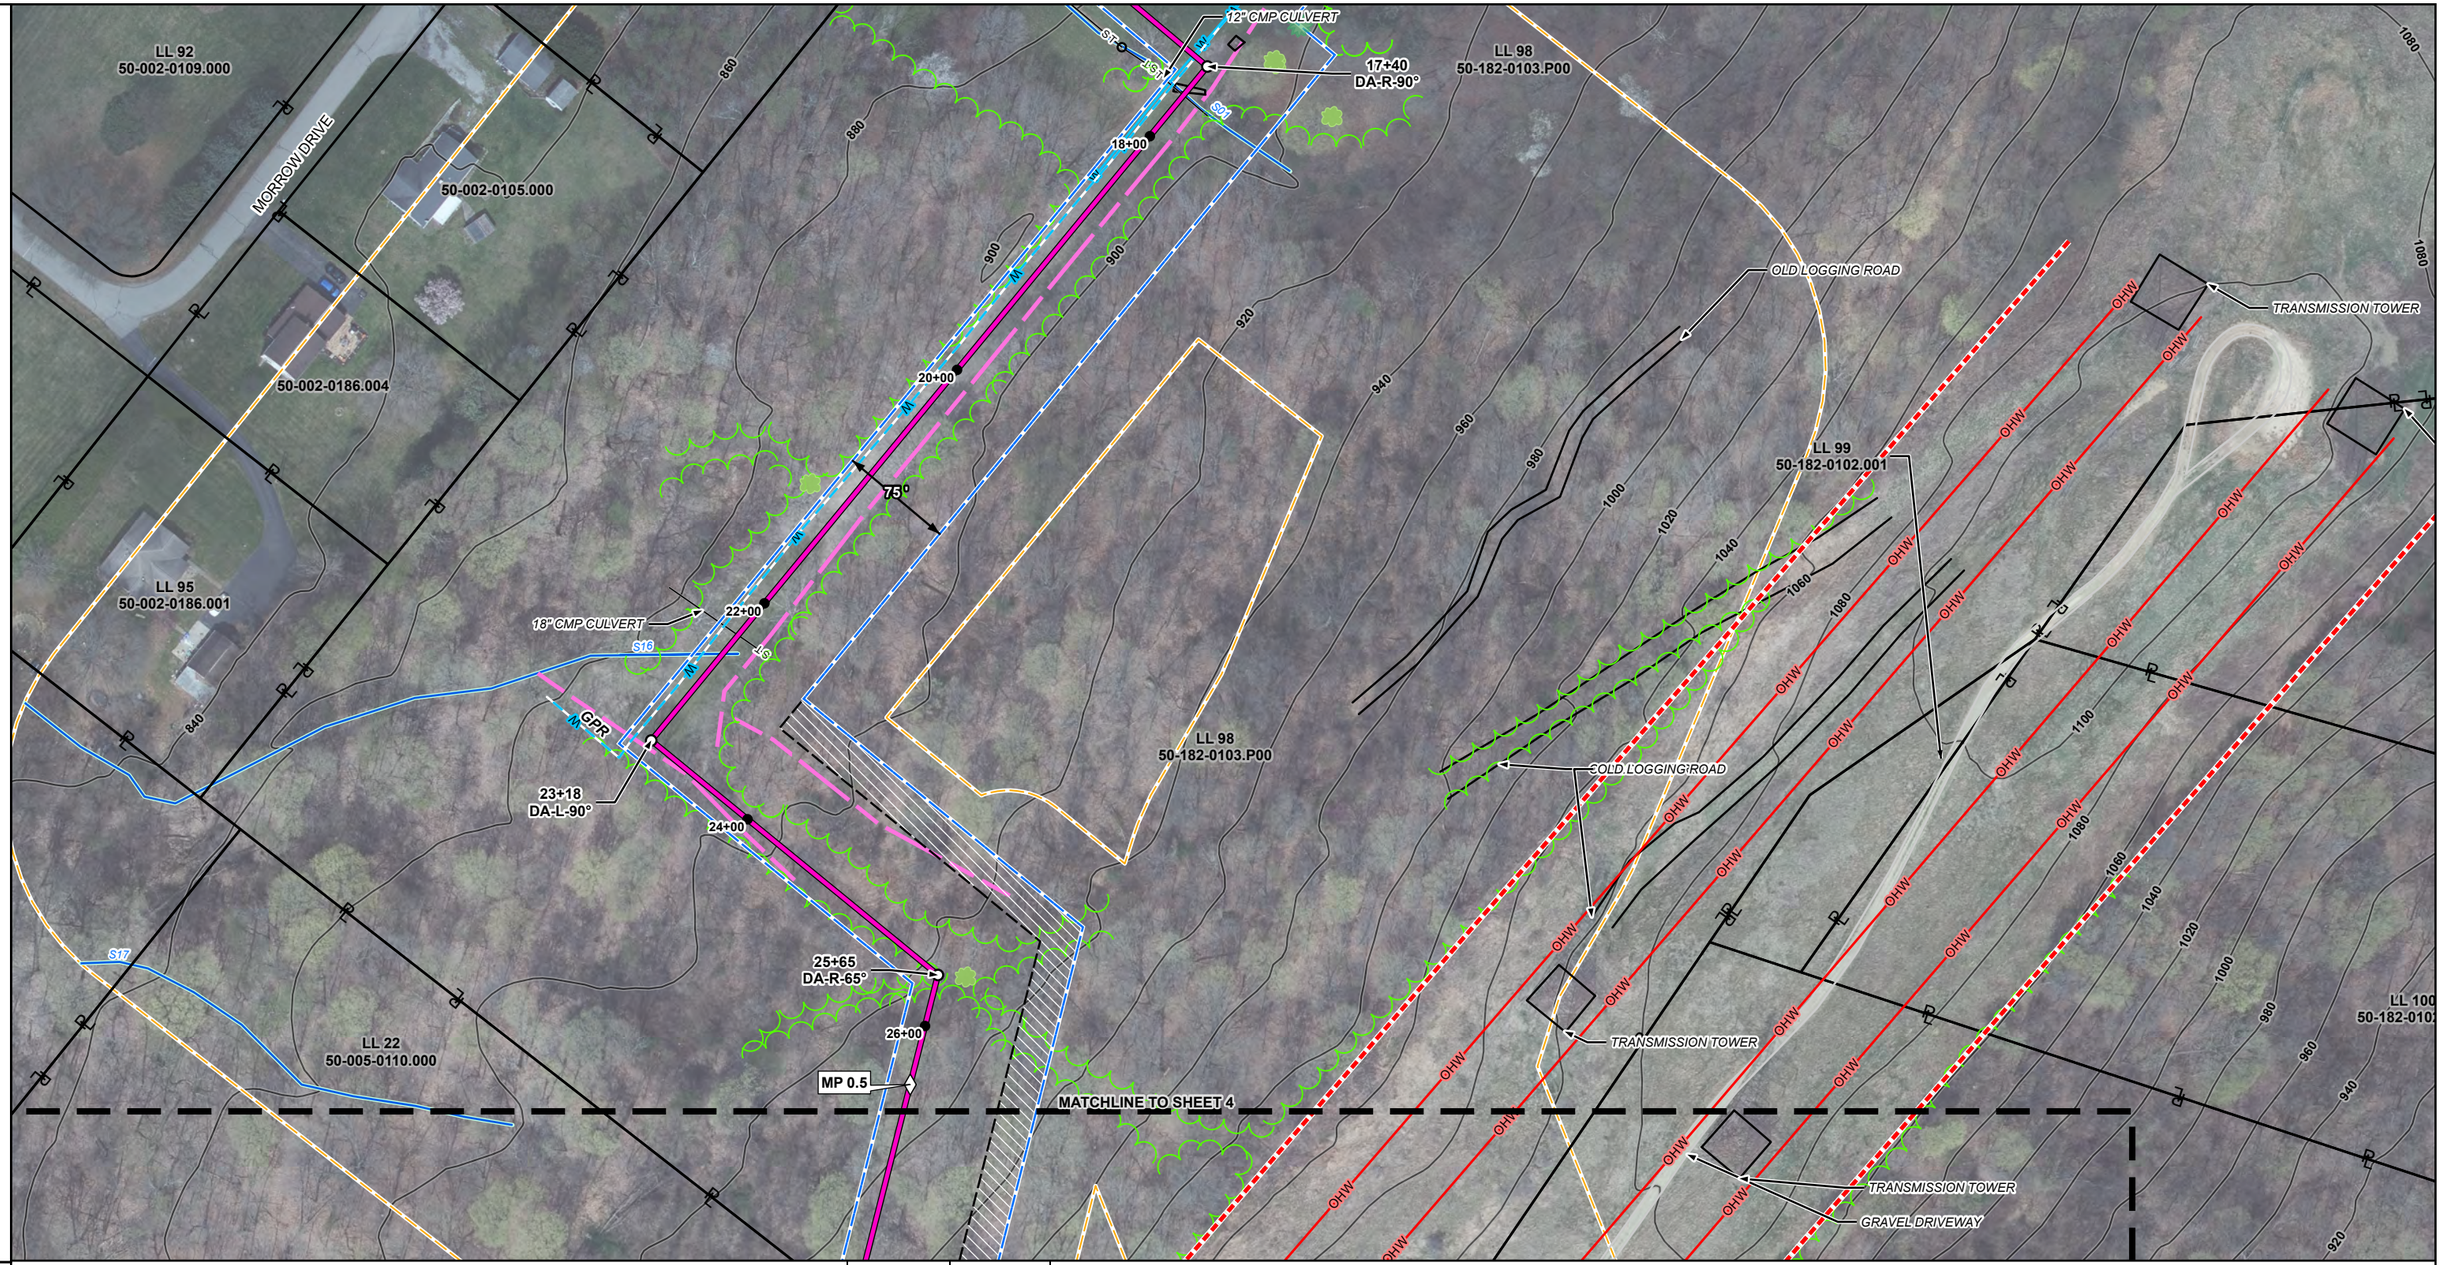

FOOTAGE	25'	700'	259'
WALL THICKNESS	24"-0.500WT	24"-0.562WT	24"-0.500WT
GRADE	X-65	X-65	X-65
COATING	FBE	PWR	FBE

16+75 MATCHLINE | 17+00 MATCHLINE | 24+00 MATCHLINE | 26+59 MATCHLINE

N W E S

ISSUED FOR FERC

National Fuel® Supply Corporation

0 100 200 Feet

National Fuel Supply Corporation
Shippingport Lateral Project

Shippingport Borough
Beaver County
Pennsylvania

REV
P

DRAWN BY : KEYSTONE CONSULTANTS. LLC
CHECKED BY : D. MCINTIRE
SCALE : 1 =100 feet
DATE : 8/21/2025

3
34

PIPELINE

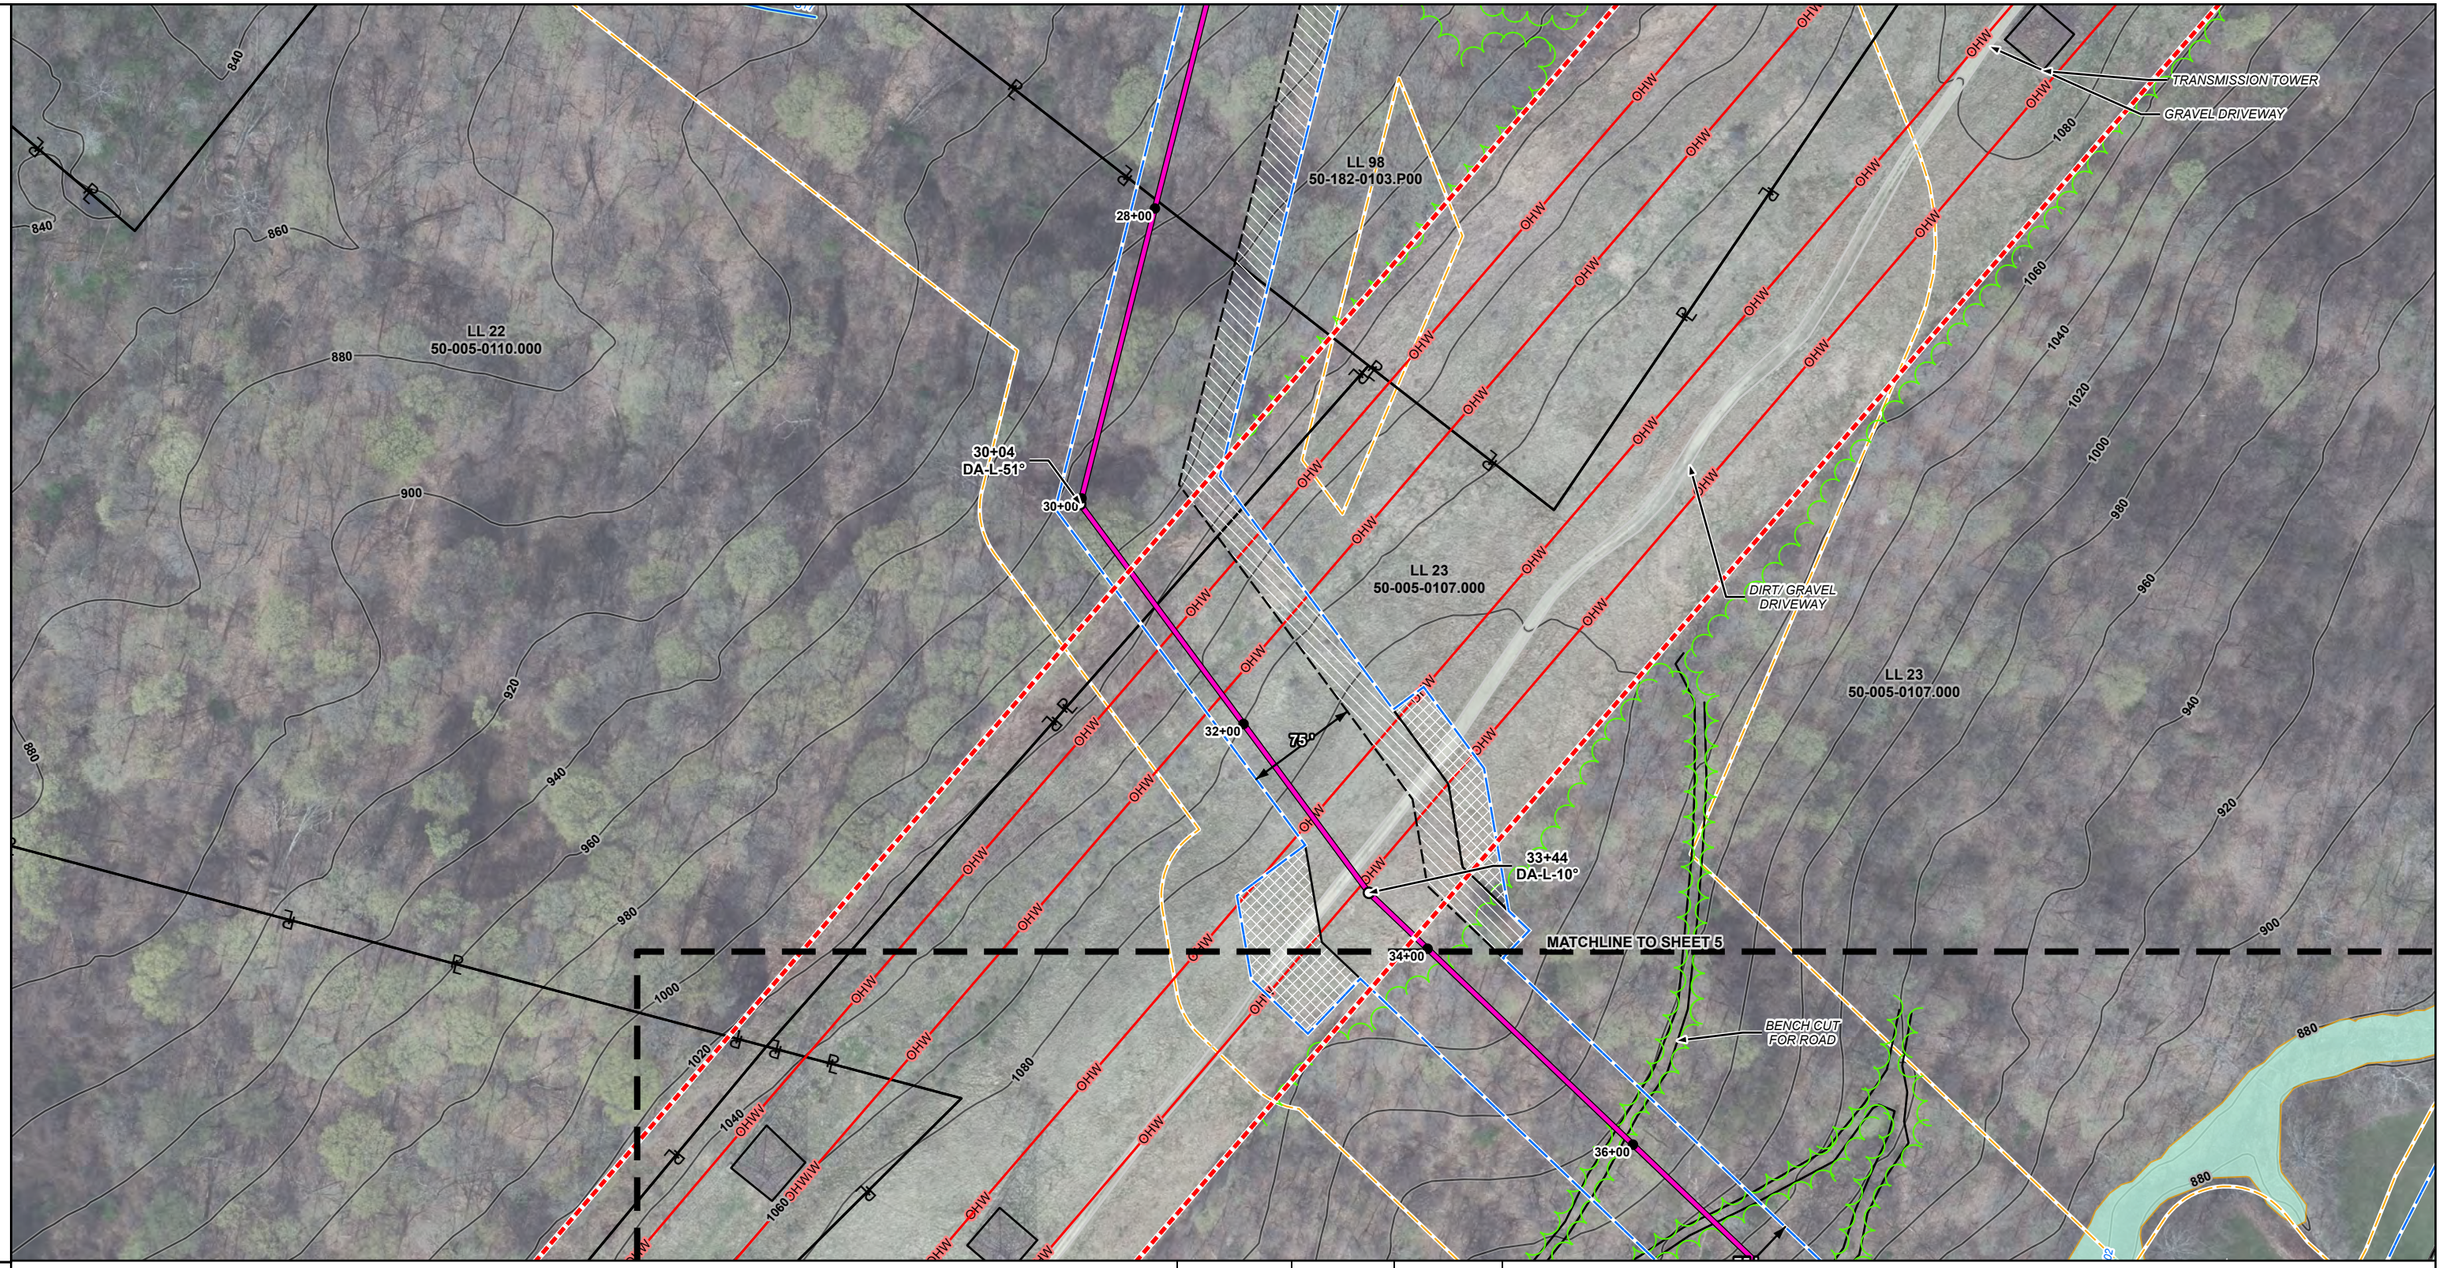

FOOTAGE		656'	20'	68'	
WALL THICKNESS		24"-0.500WT	24"-0.562WT	24"-0.500WT	
GRADE		X-65	X-65	X-65	
COATING		FBE	PWR	FBE	

26+59 MATCHLINE | 33+15 | 33+35 | 34+03 MATCHLINE

N W E S

ISSUED FOR FERC

National Fuel® Supply Corporation

0 100 200 Feet

National Fuel Supply Corporation
Shippingport Lateral Project

Shippingport Borough
Beaver County
Pennsylvania

REV
P

DRAWN BY : KEYSTONE CONSULTANTS. LLC
CHECKED BY : D. MCINTIRE
SCALE : 1 =100 feet
DATE : 8/21/2025

PIPELINE

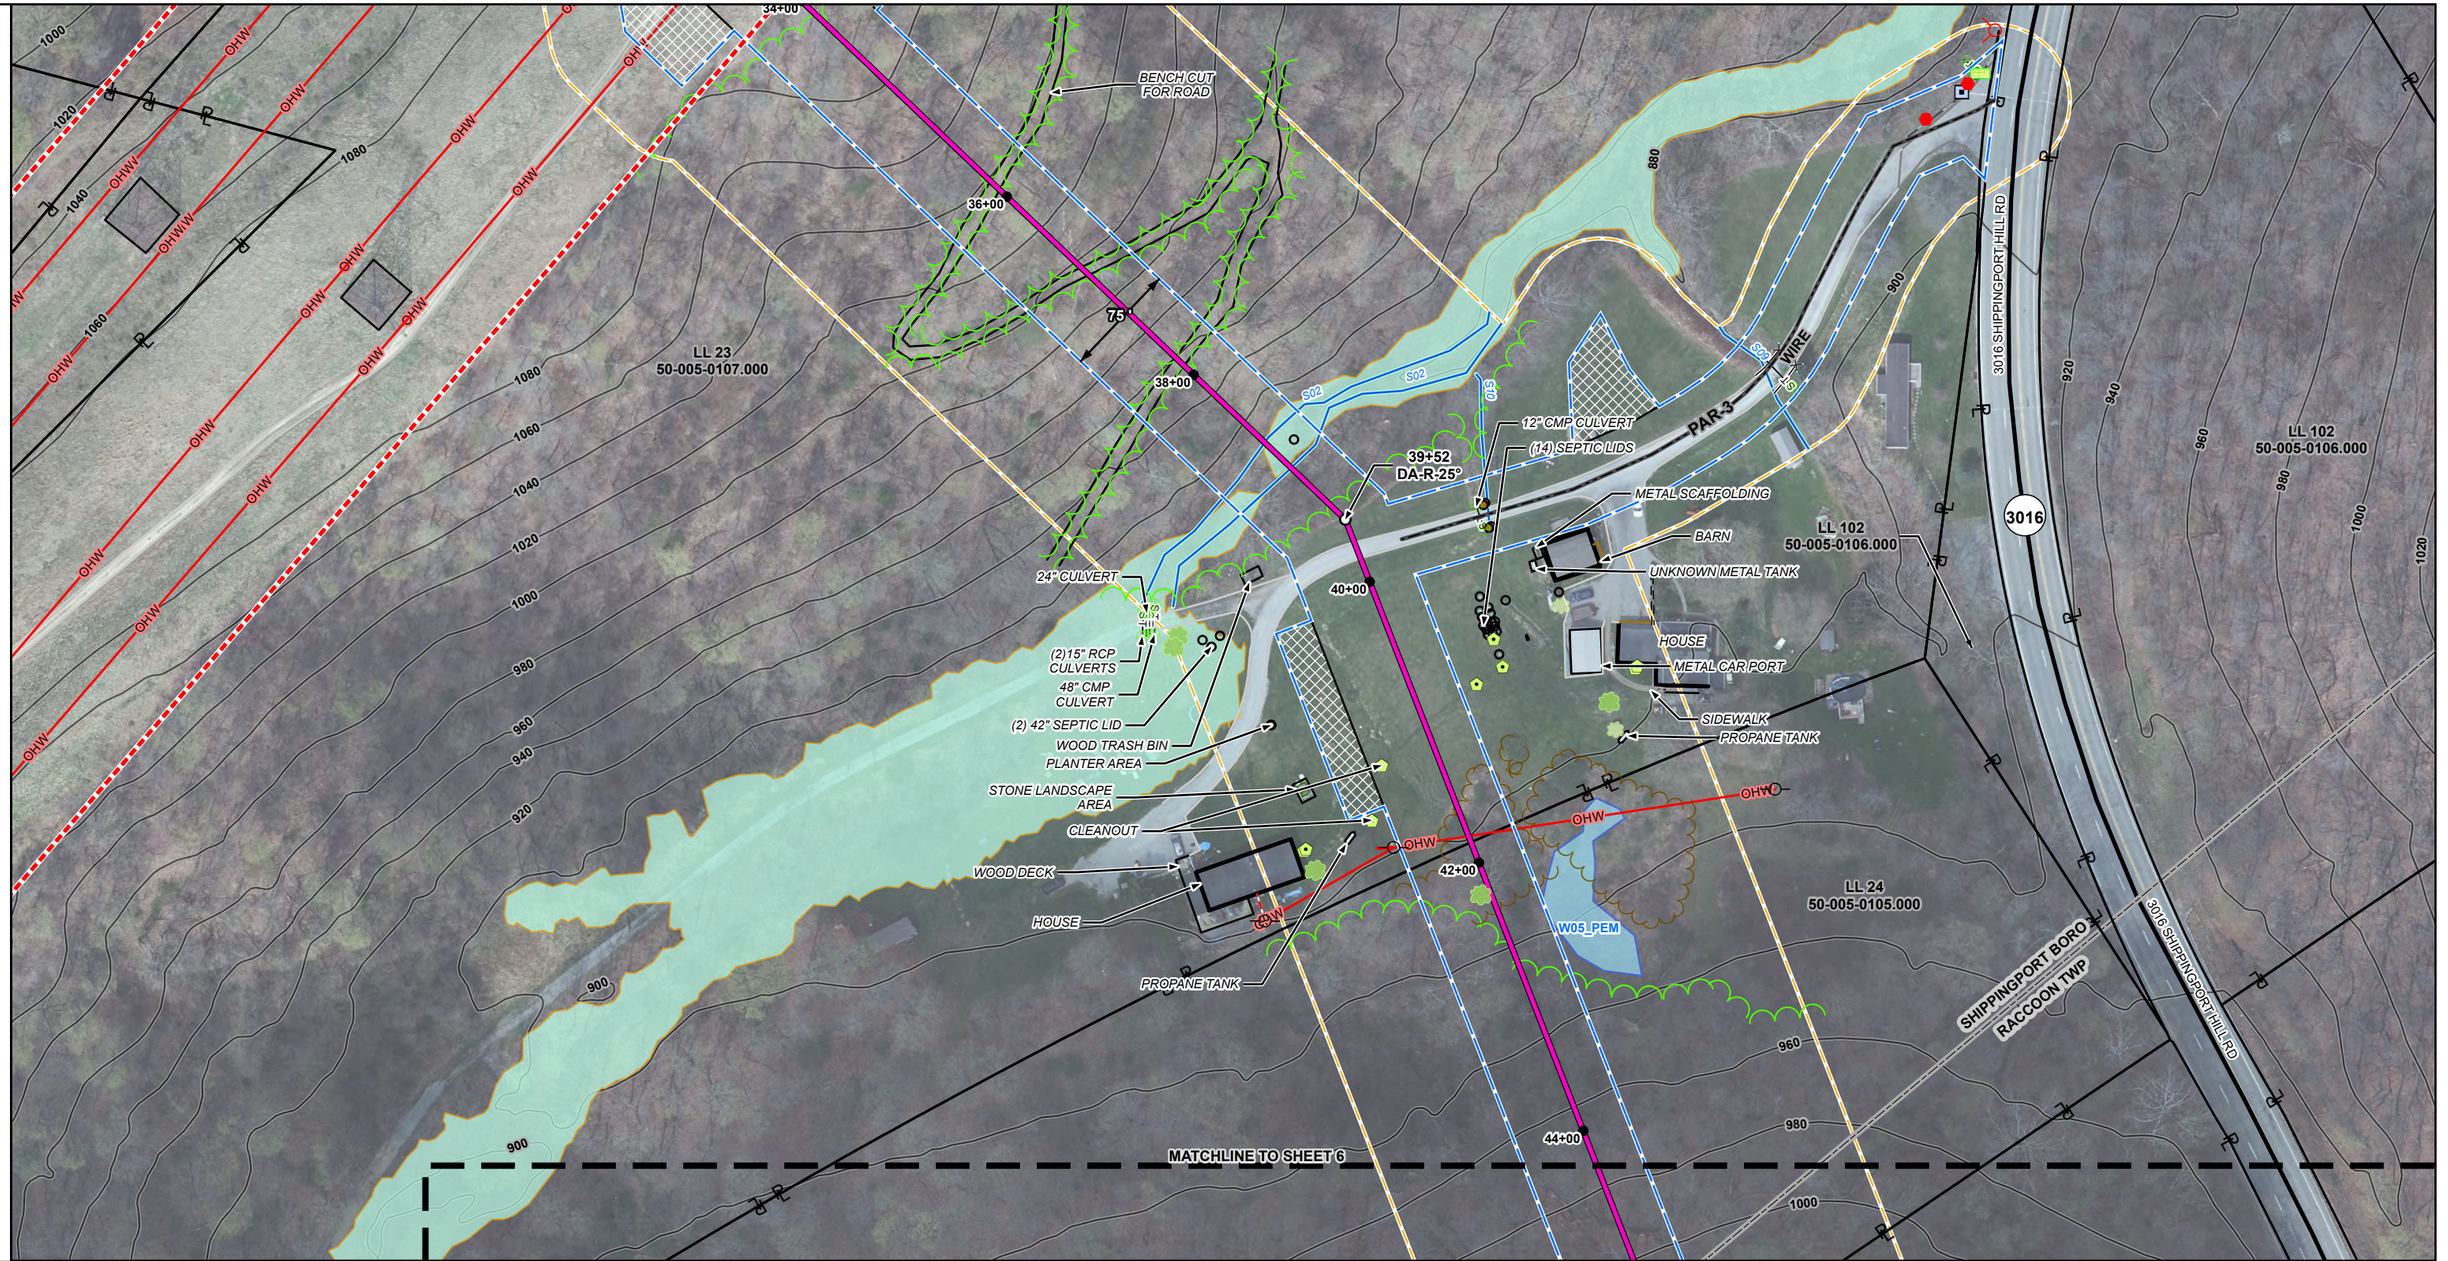

FOOTAGE		175'	20'	76'	20'	81'	20'	170'	20'	442'	
WALL THICKNESS	34+03 MATCHLINE	24"-0.500WT	24"-0.562WT	24"-0.500WT	24"-0.562WT	24"-0.500WT	24"-0.562WT	24"-0.500WT	24"-0.562WT	24"-0.500WT	44+27 MATCHLINE
GRADE		X-65	X-65	X-65	X-65	X-65	X-65	X-65	X-65	X-65	
COATING		FBE	PWR	FBE	PWR	FBE	PWR	FBE	PWR	FBE	

35+78 | 35+98 | 36+74 | 36+94 | 37+75 | 37+95 | 39+65 | 39+85

N W E S

ISSUED FOR FERC

National Fuel® Supply Corporation

0 100 200 Feet

National Fuel Supply Corporation
Shippingport Lateral Project
Shippingport Borough & Raccoon Township
Beaver County
Pennsylvania

REV
P

DRAWN BY : KEYSTONE CONSULTANTS, LLC
CHECKED BY : D. MCINTIRE
SCALE : 1 =100 feet
DATE : 8/21/2025

PIPELINE

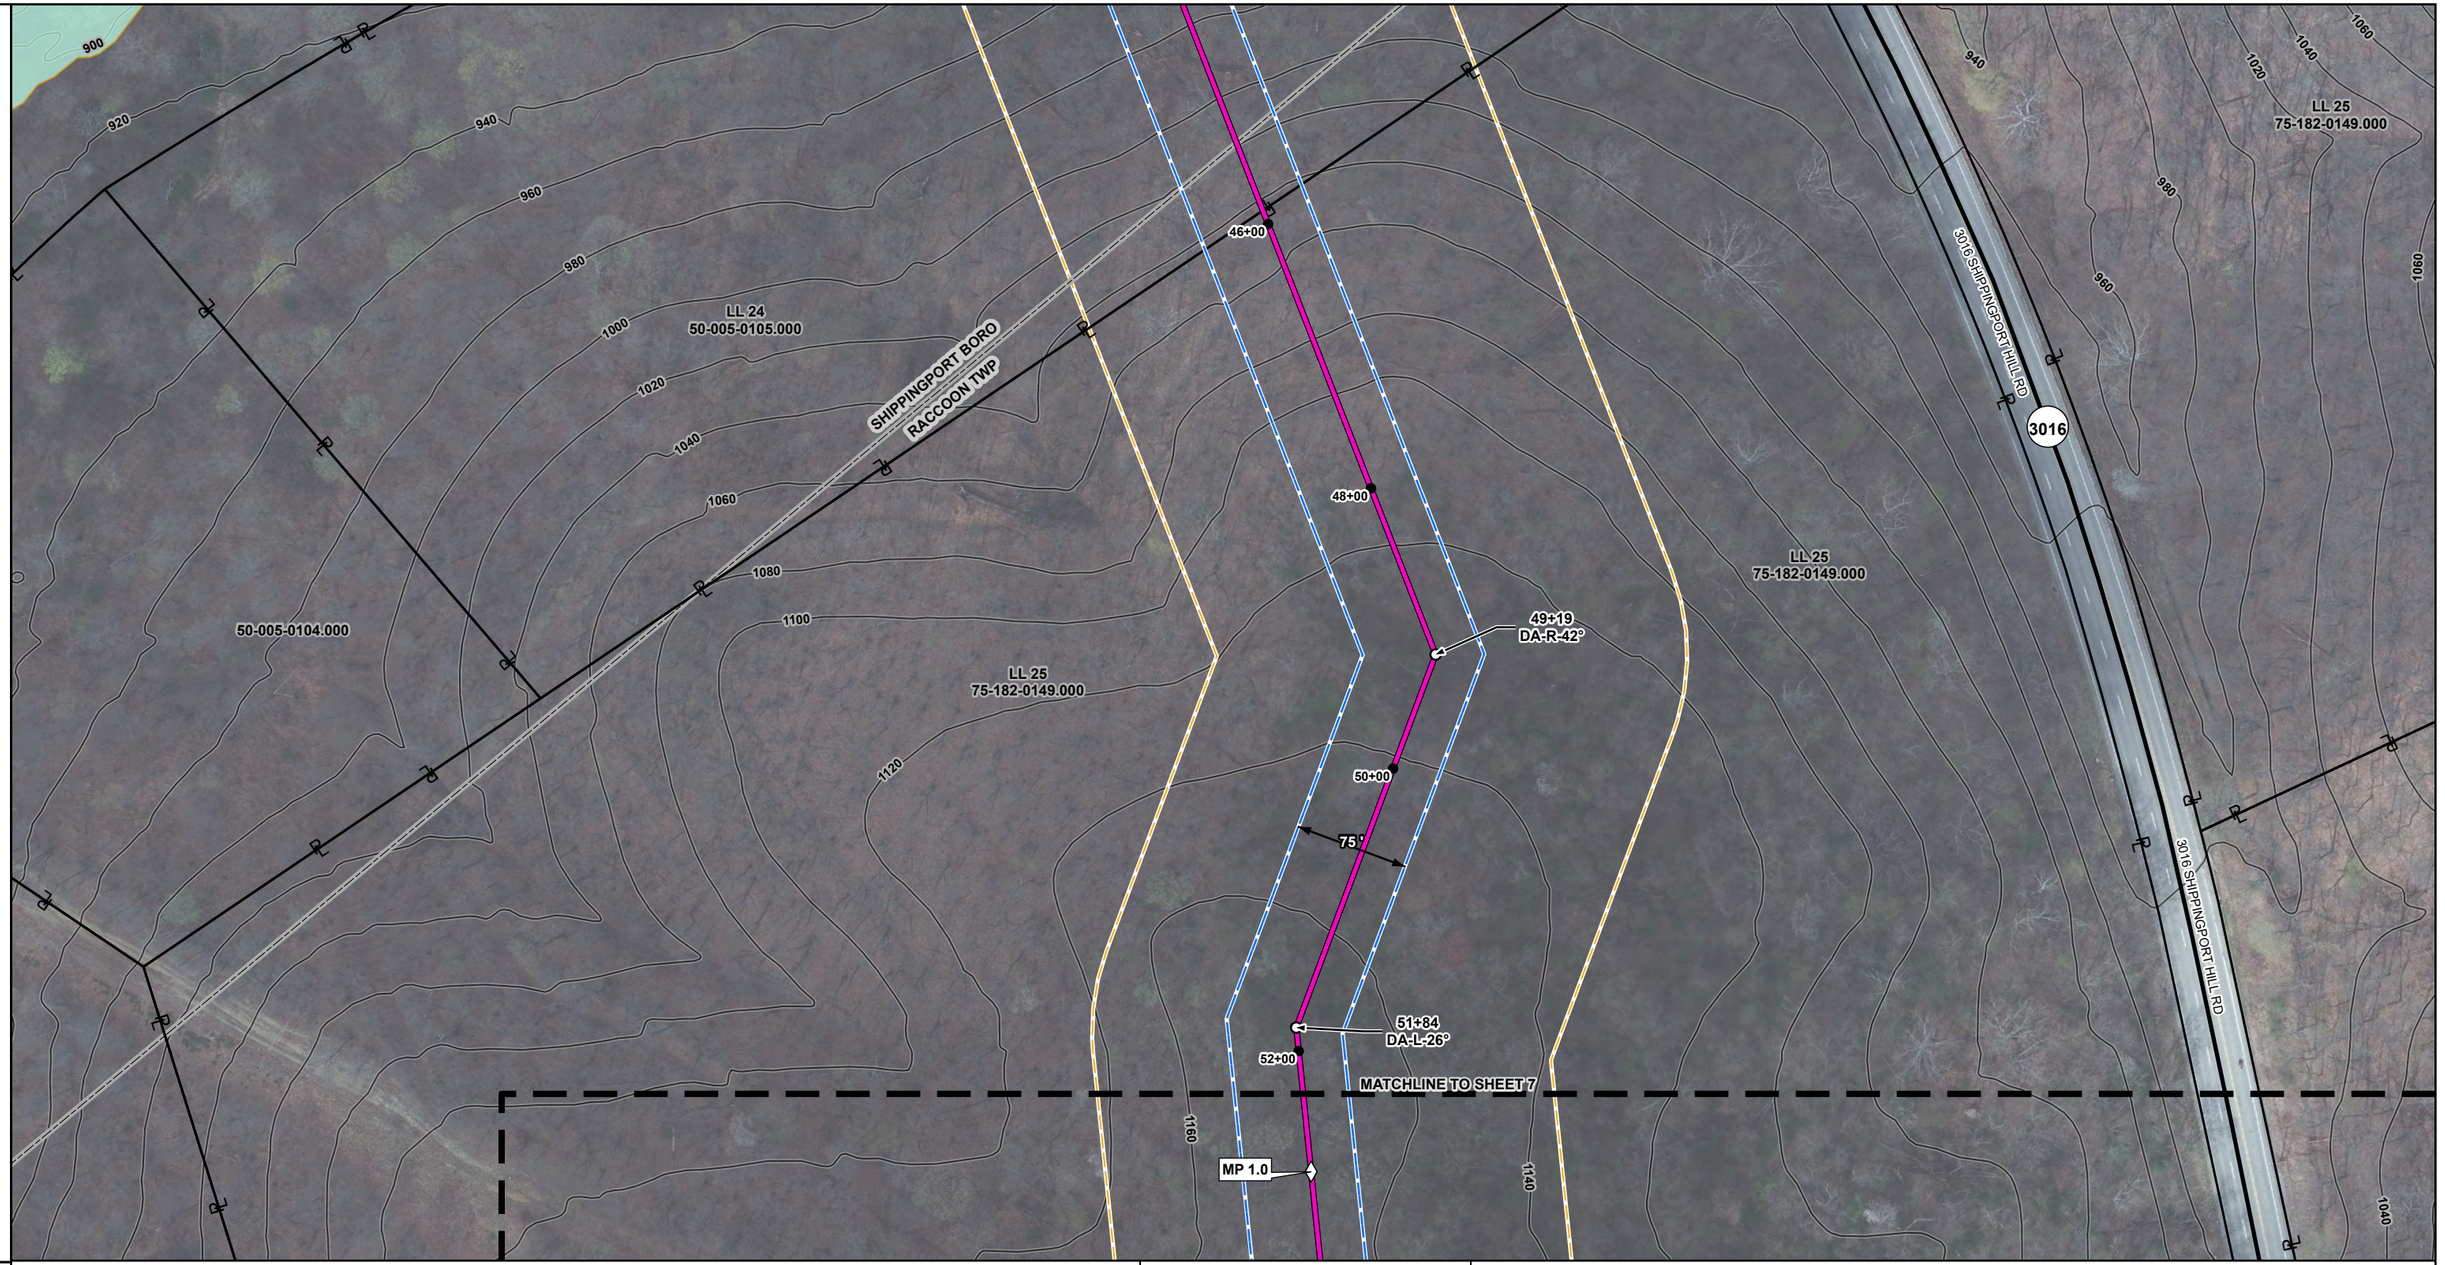

FOOTAGE		801'	
WALL THICKNESS	44+27 MATCHLINE	24"-0.500WT	52+28 MATCHLINE
GRADE		X-65	
COATING		FBE	

N W E S

ISSUED FOR FERC

National Fuel® Supply Corporation

0 100 200 Feet

National Fuel Supply Corporation
Shippingport Lateral Project

Raccoon Township
Beaver County
Pennsylvania

REV		
P	DRAWN BY :	KEYSTONE CONSULTANTS. LLC
	CHECKED BY :	D. MCINTIRE
	SCALE :	1 =100 feet
	DATE :	8/21/2025

PIPELINE

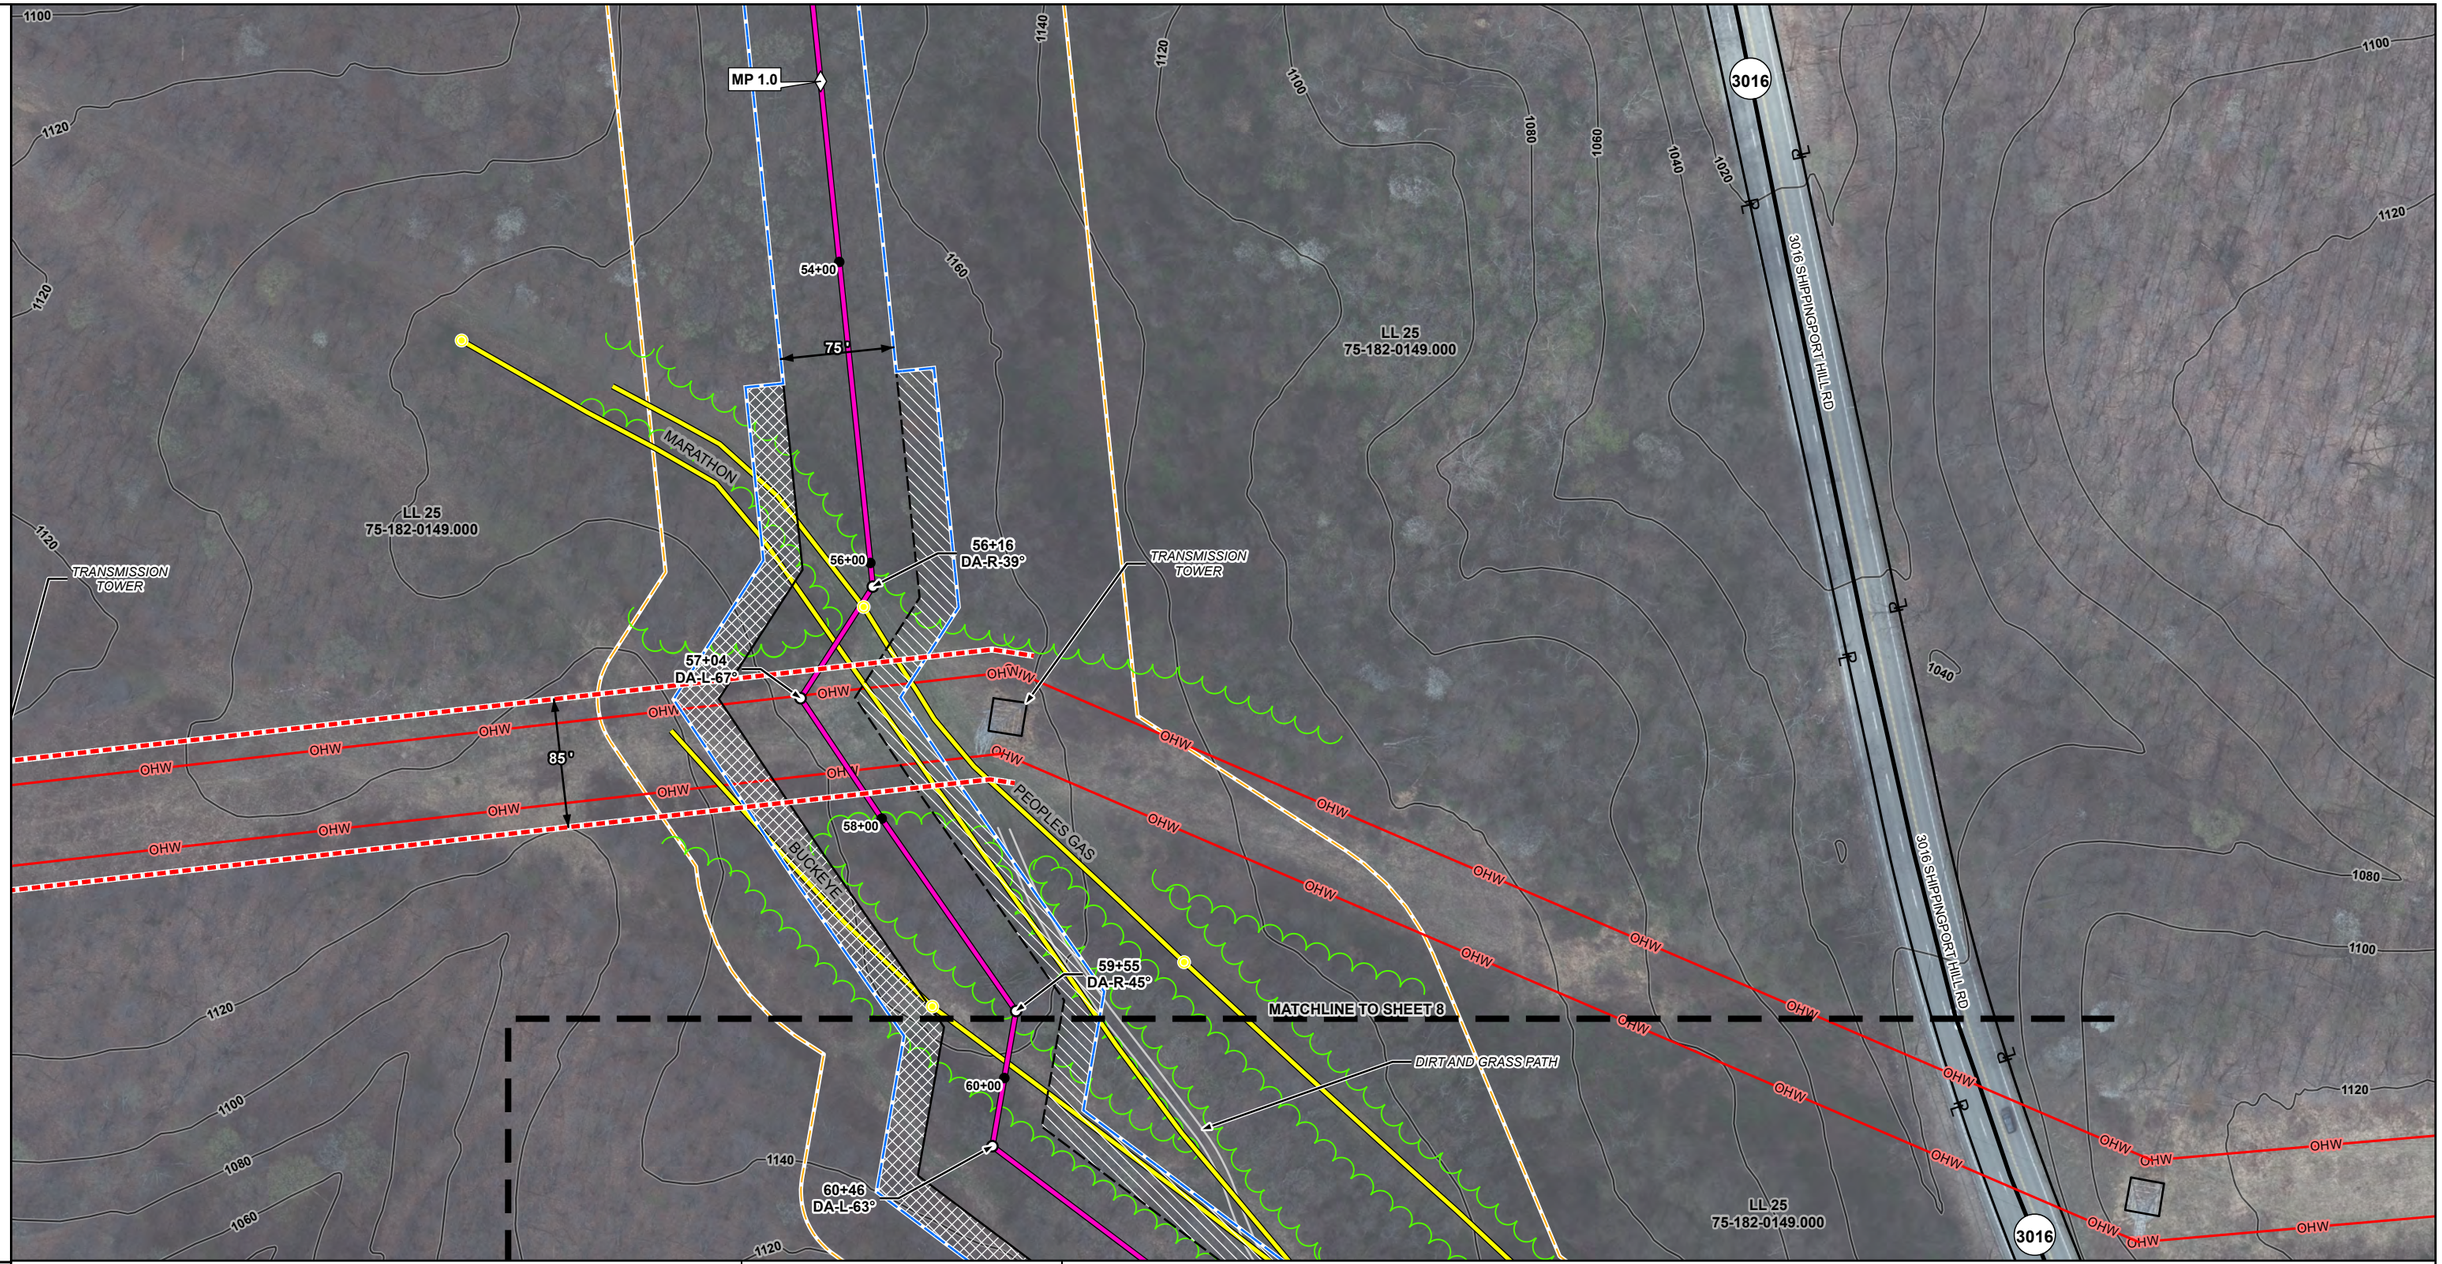

FOOTAGE		732'	
WALL THICKNESS	52+28 MATCHLINE	24"-0.500WT	59+60 MATCHLINE
GRADE		X-65	
COATING		FBE	

N W E S

ISSUED FOR FERC

National Fuel® Supply Corporation

0 100 200 Feet

National Fuel Supply Corporation
Shippingport Lateral Project

Raccoon Township
Beaver County
Pennsylvania

REV	DRAWN BY : KEYSTONE CONSULTANTS. LLC	7
	CHECKED BY : D. MCINTIRE	
P	SCALE : 1 =100 feet	34
	DATE : 8/21/2025	

PIPELINE

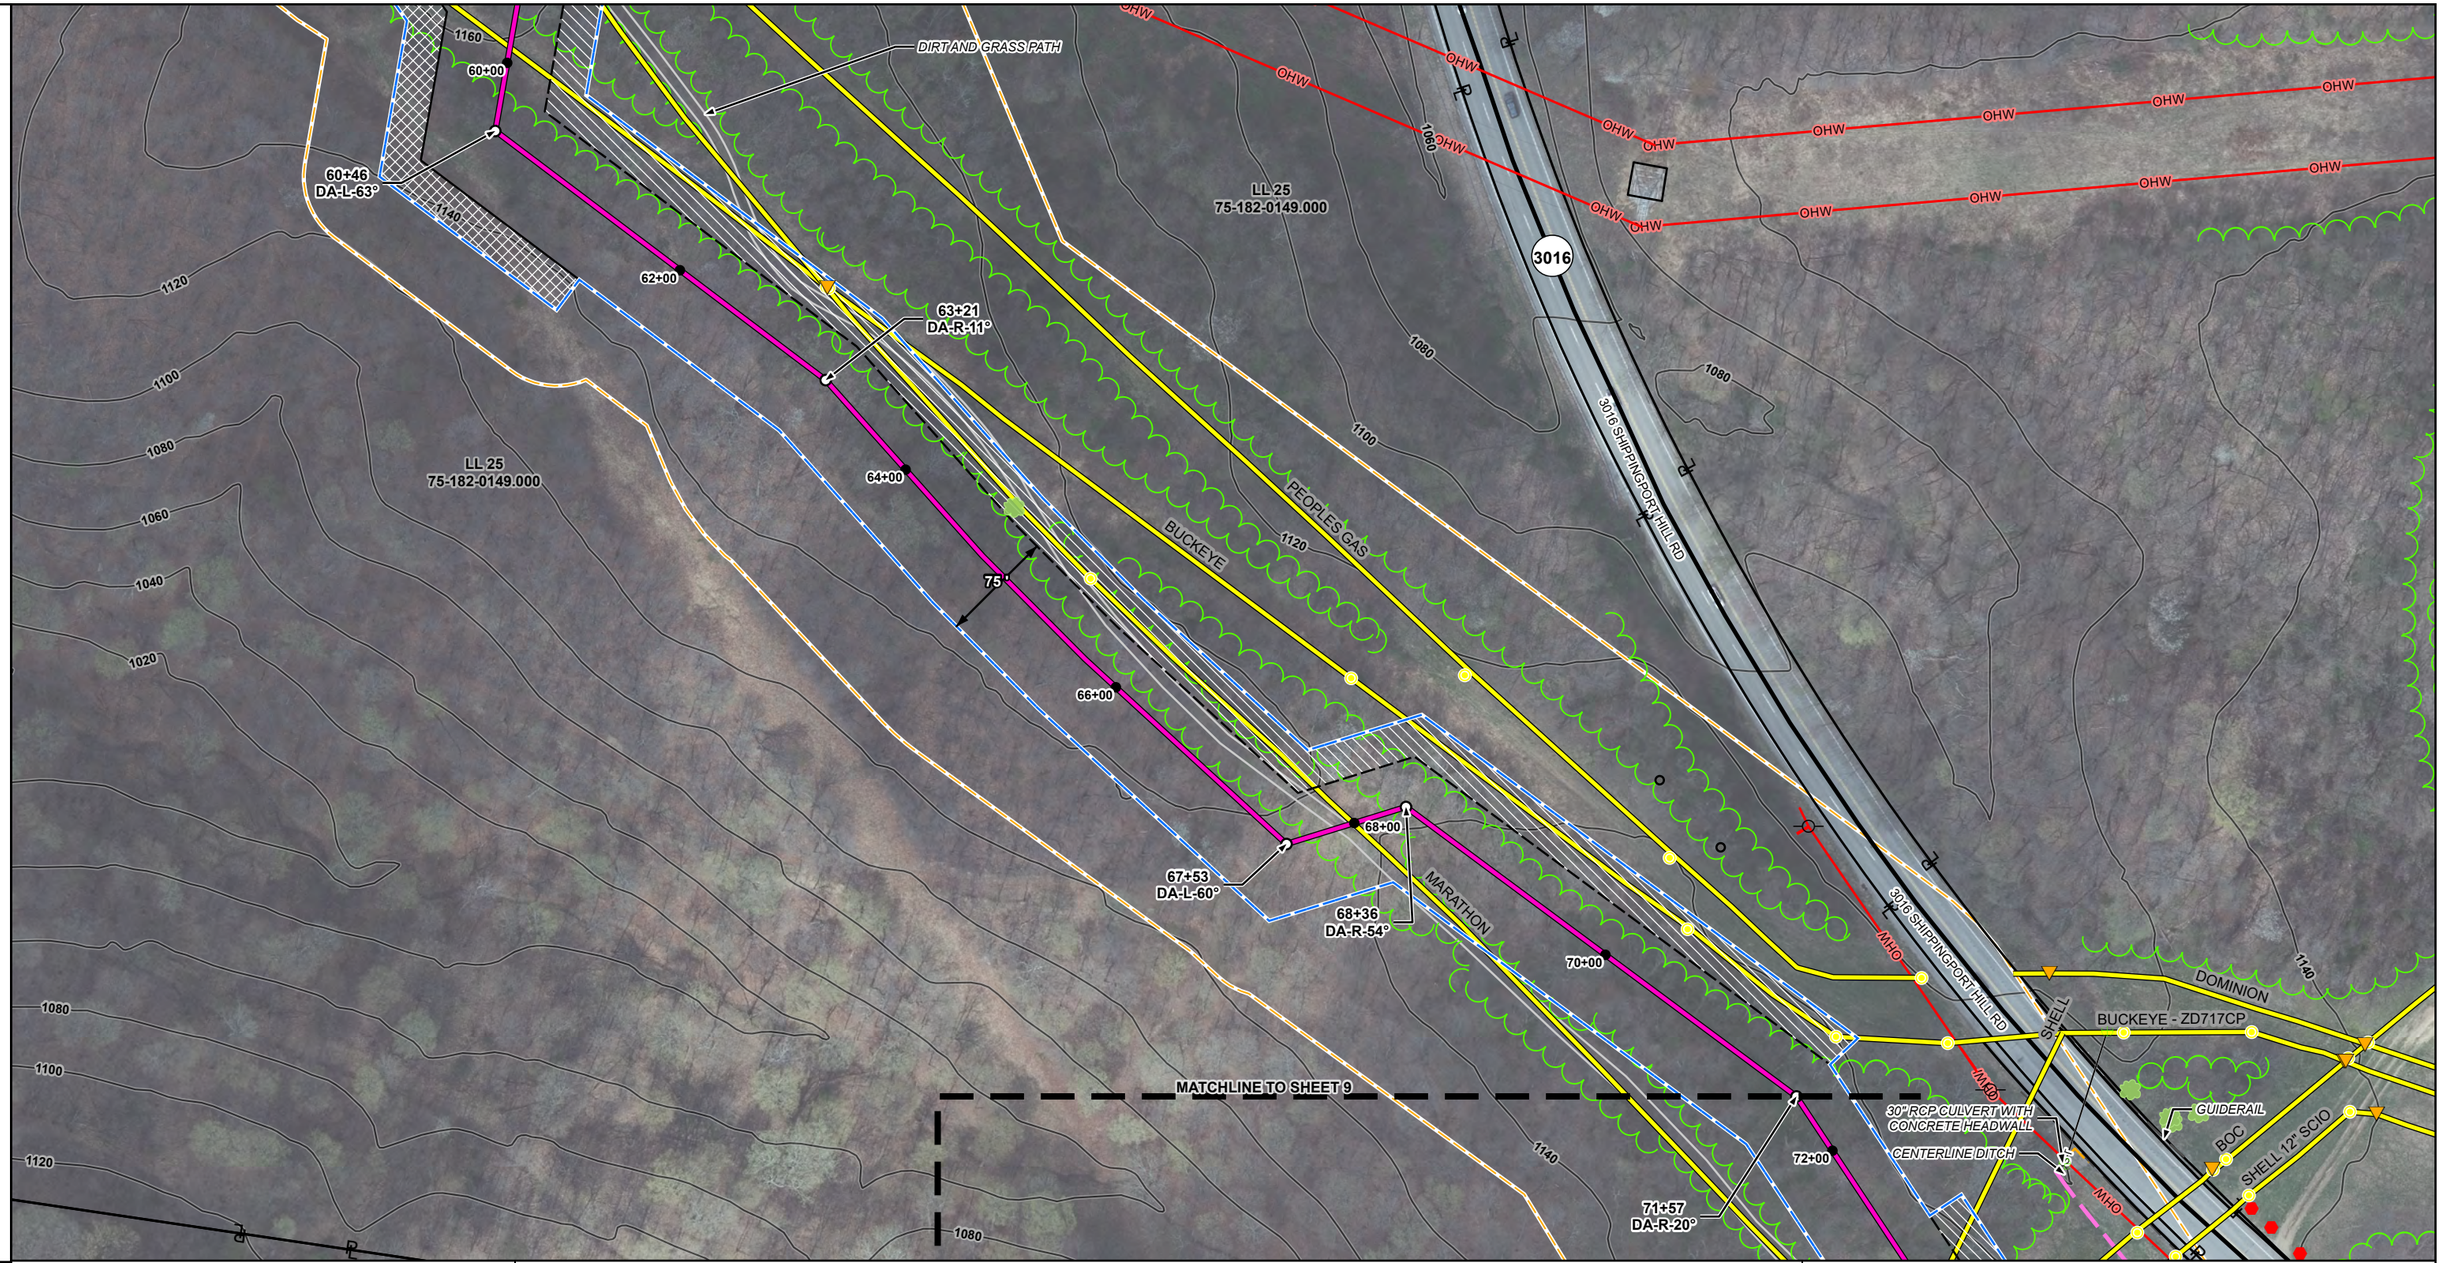

FOOTAGE		1197'	
WALL THICKNESS		24"-0.500WT	
GRADE	59+60 MATCHLINE	X-65	71+57 MATCHLINE
COATING		FBE	

N W E S

ISSUED FOR FERC

National Fuel® Supply Corporation

0 100 200 Feet

National Fuel Supply Corporation
Shippingport Lateral Project

Raccoon Township
Beaver County
Pennsylvania

REV		
P	DRAWN BY :	KEYSTONE CONSULTANTS. LLC
	CHECKED BY :	D. MCINTIRE
	SCALE :	1 =100 feet
	DATE :	8/21/2025

PIPELINE

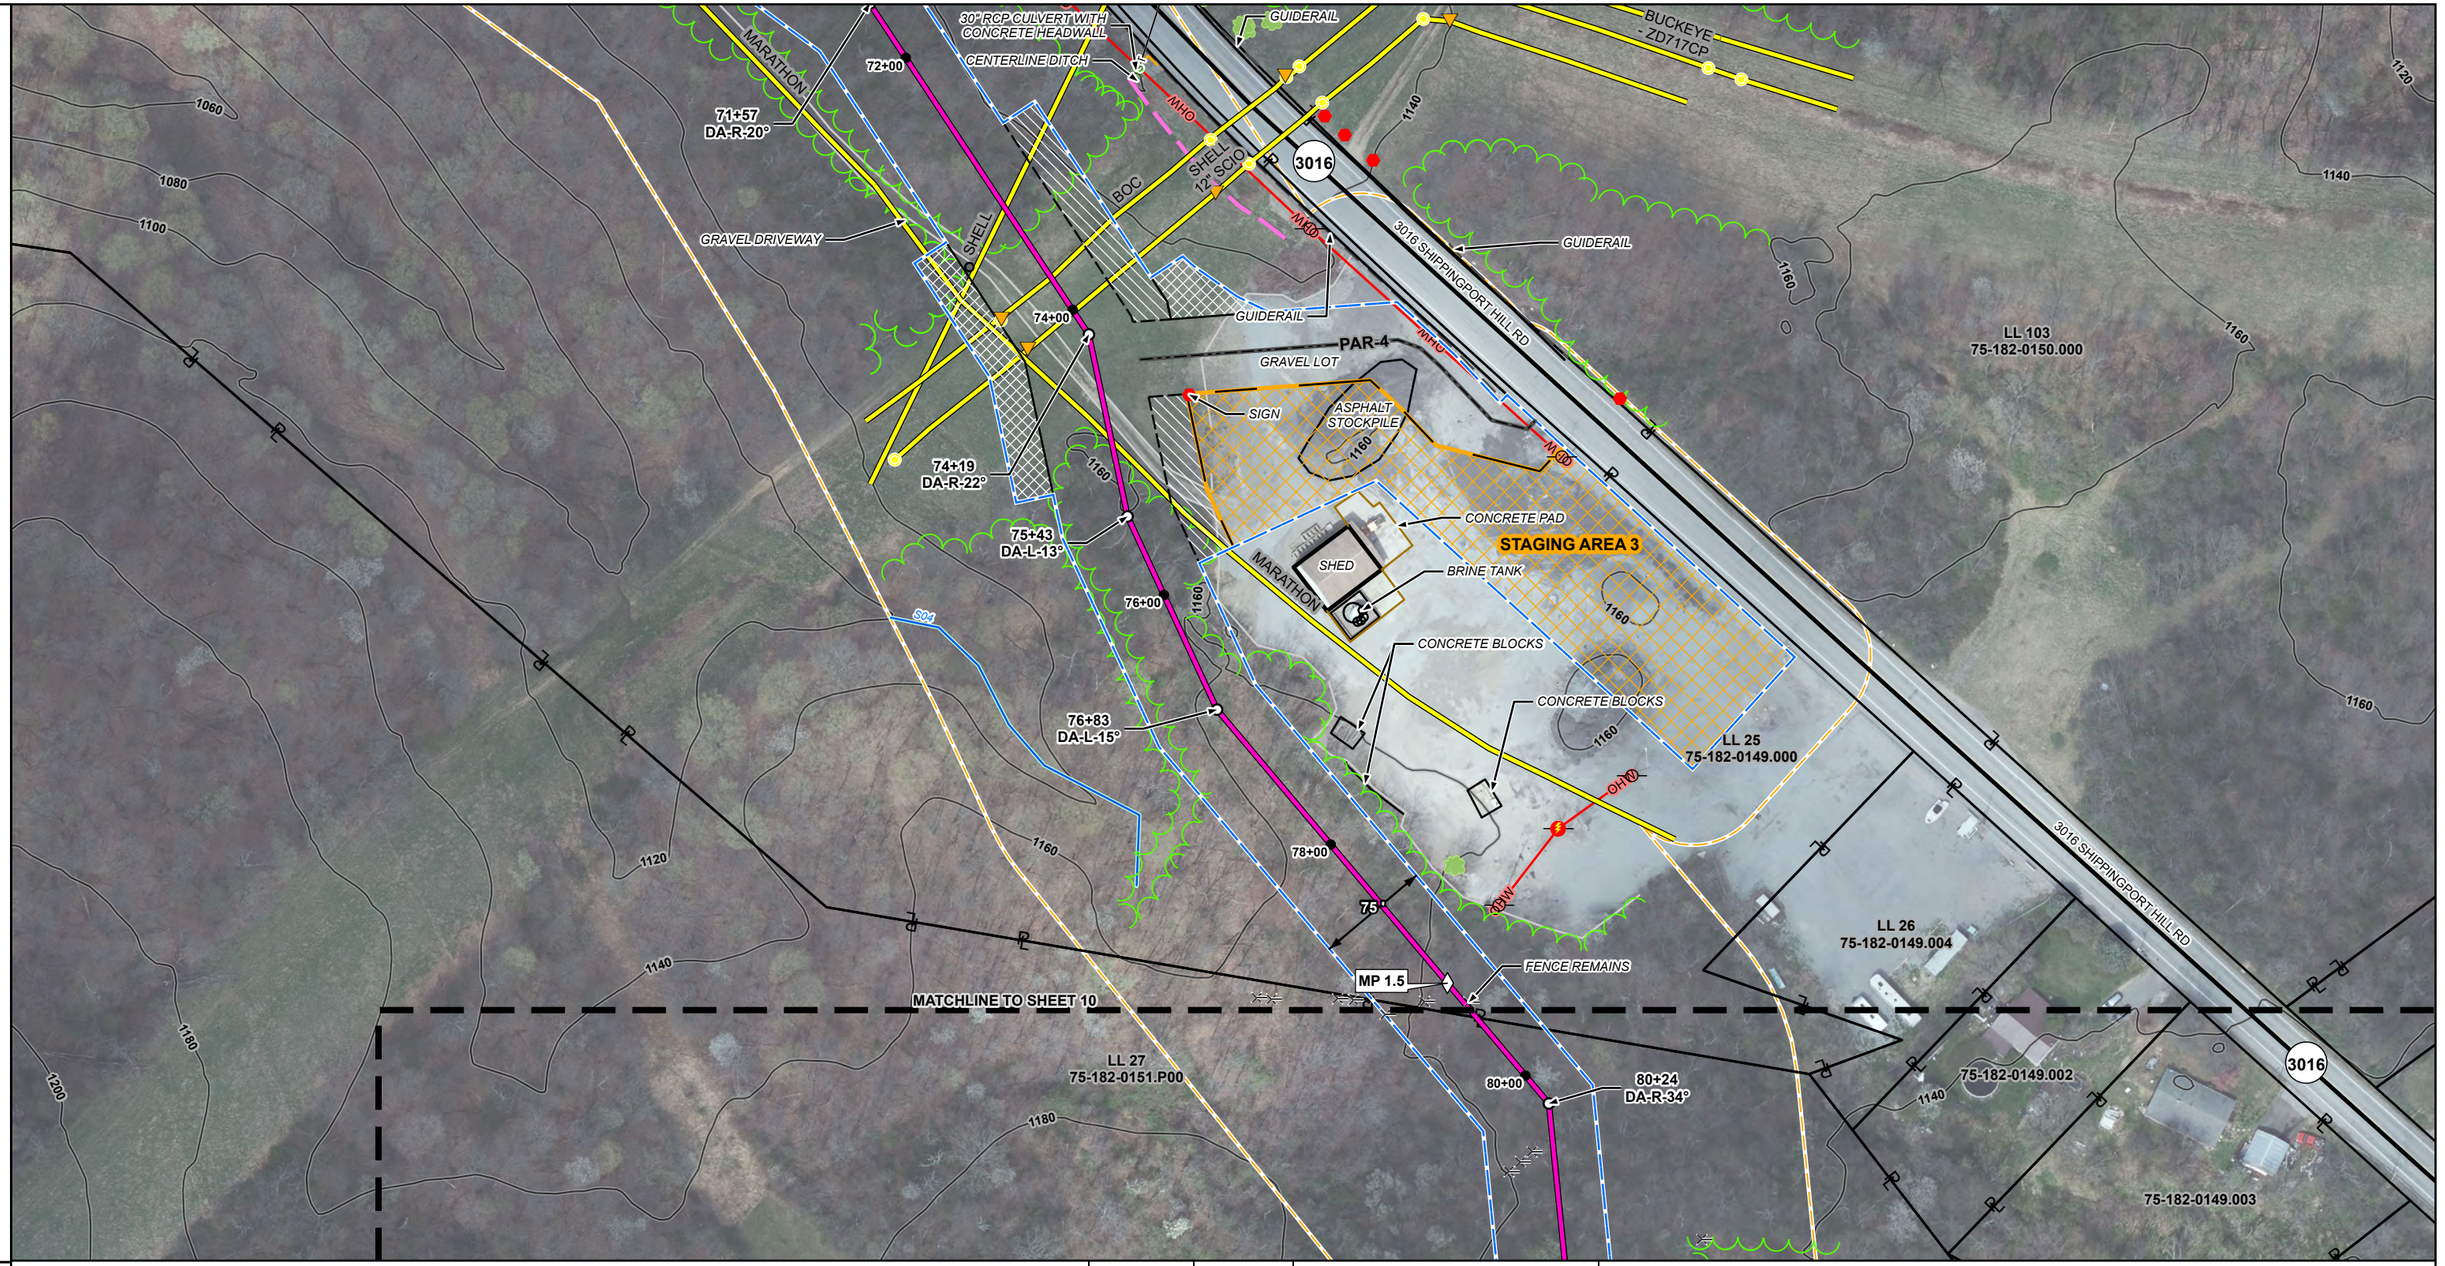

	71+57 MATCHLINE		74+56		74+76		79+43 MATCHLINE
FOOTAGE		299'		20'		467'	
WALL THICKNESS		24"-0.500WT		24"-0.562WT		24"-0.500WT	
GRADE		X-65		X-65		X-65	
COATING		FBE		PWR		FBE	

N W E S

ISSUED FOR FERC

National Fuel® Supply Corporation

0 100 200 Feet

National Fuel Supply Corporation
Shippingport Lateral Project

Raccoon Township
Beaver County
Pennsylvania

REV
P

DRAWN BY : KEYSTONE CONSULTANTS. LLC
CHECKED BY : D. MCINTIRE
SCALE : 1 =100 feet
DATE : 8/21/2025

9
34

PIPELINE

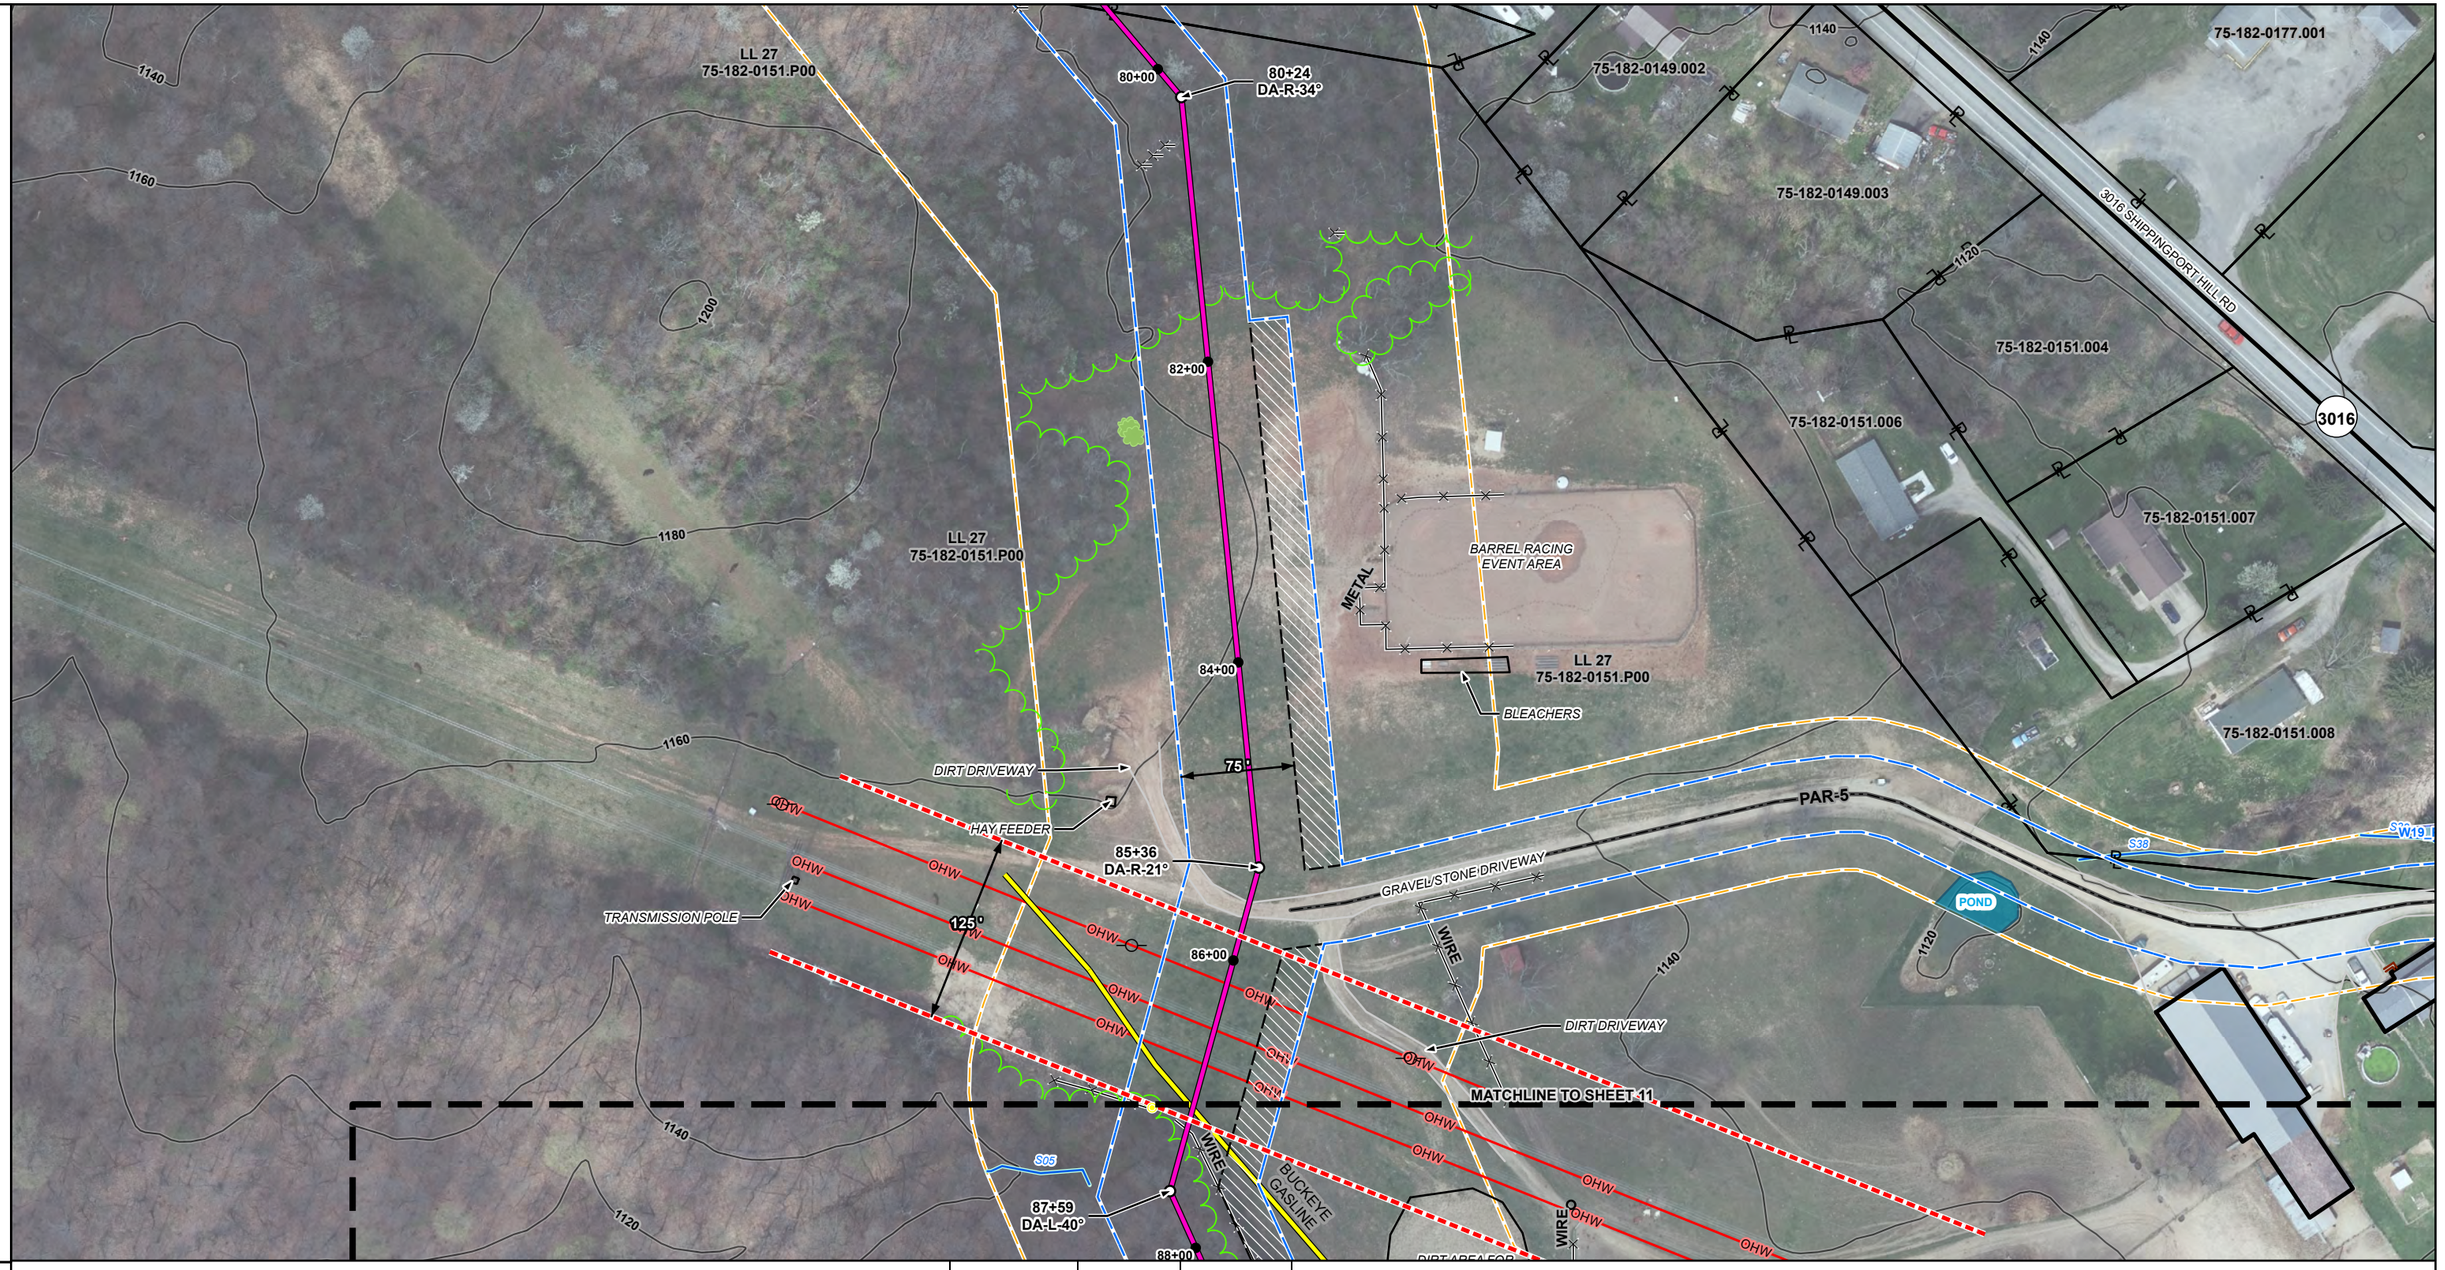

FOOTAGE		612'	20'	127'
WALL THICKNESS	79+43 MATCHLINE	24"-0.500WT	24"-0.562WT	24"-0.500WT
GRADE	85+55	X-65	X-65	X-65
COATING	85+75	FBE	PWR	FBE

87+02 MATCHLINE

N W E S

ISSUED FOR FERC

National Fuel® Supply Corporation

0 100 200 Feet

National Fuel Supply Corporation
Shippingport Lateral Project

Raccoon Township
Beaver County
Pennsylvania

REV P

DRAWN BY : KEYSTONE CONSULTANTS. LLC
CHECKED BY : D. MCINTIRE
SCALE : 1 =100 feet
DATE : 8/21/2025

10 / 34

PIPELINE

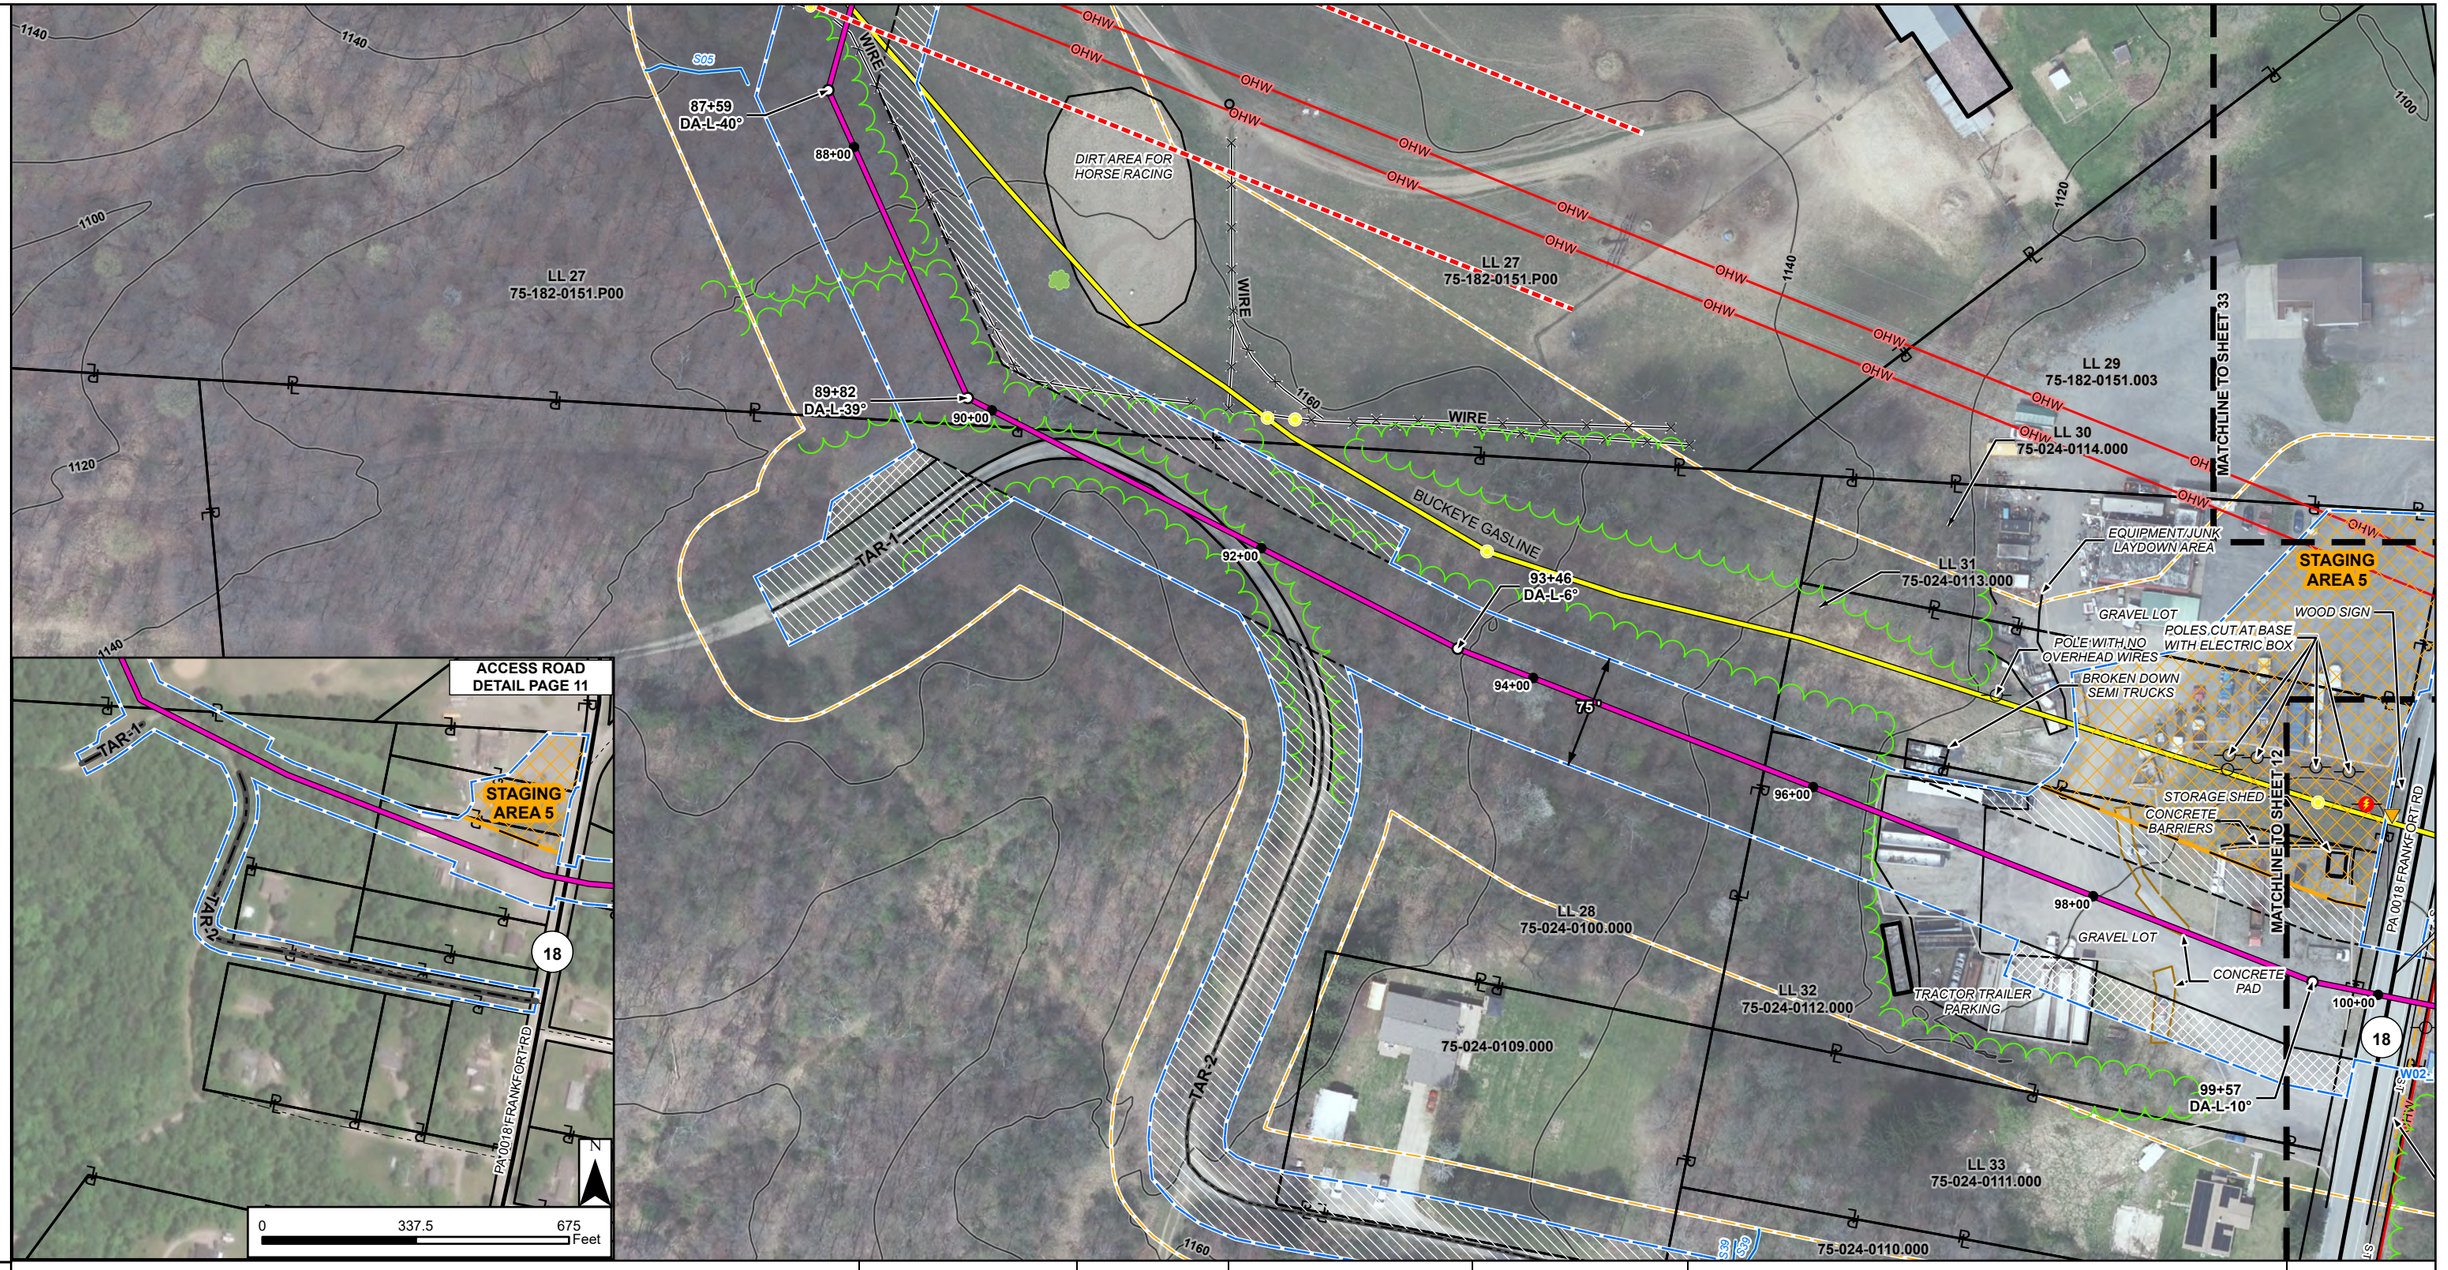

FOOTAGE		328'	170'	81'	363'	294'	
WALL THICKNESS	87+02 MATCHLINE	24"-0.500WT	24"-0.562WT	24"-0.500WT	24"-0.562WT	24"-0.562WT	99+38 MATCHLINE
GRADE		X-65	X-65	X-65	X-65	X-65	
COATING		FBE	PWR	FBE	FBE	PWR	

N W E S

ISSUED FOR FERC

National Fuel® Supply Corporation

0 100 200 Feet

National Fuel Supply Corporation
Shippingport Lateral Project
Raccoon Township
Beaver County
Pennsylvania

REV P

DRAWN BY : KEYSTONE CONSULTANTS. LLC
CHECKED BY : D. MCINTIRE
SCALE : 1 =100 feet
DATE : 8/21/2025

11 / 34

PIPELINE

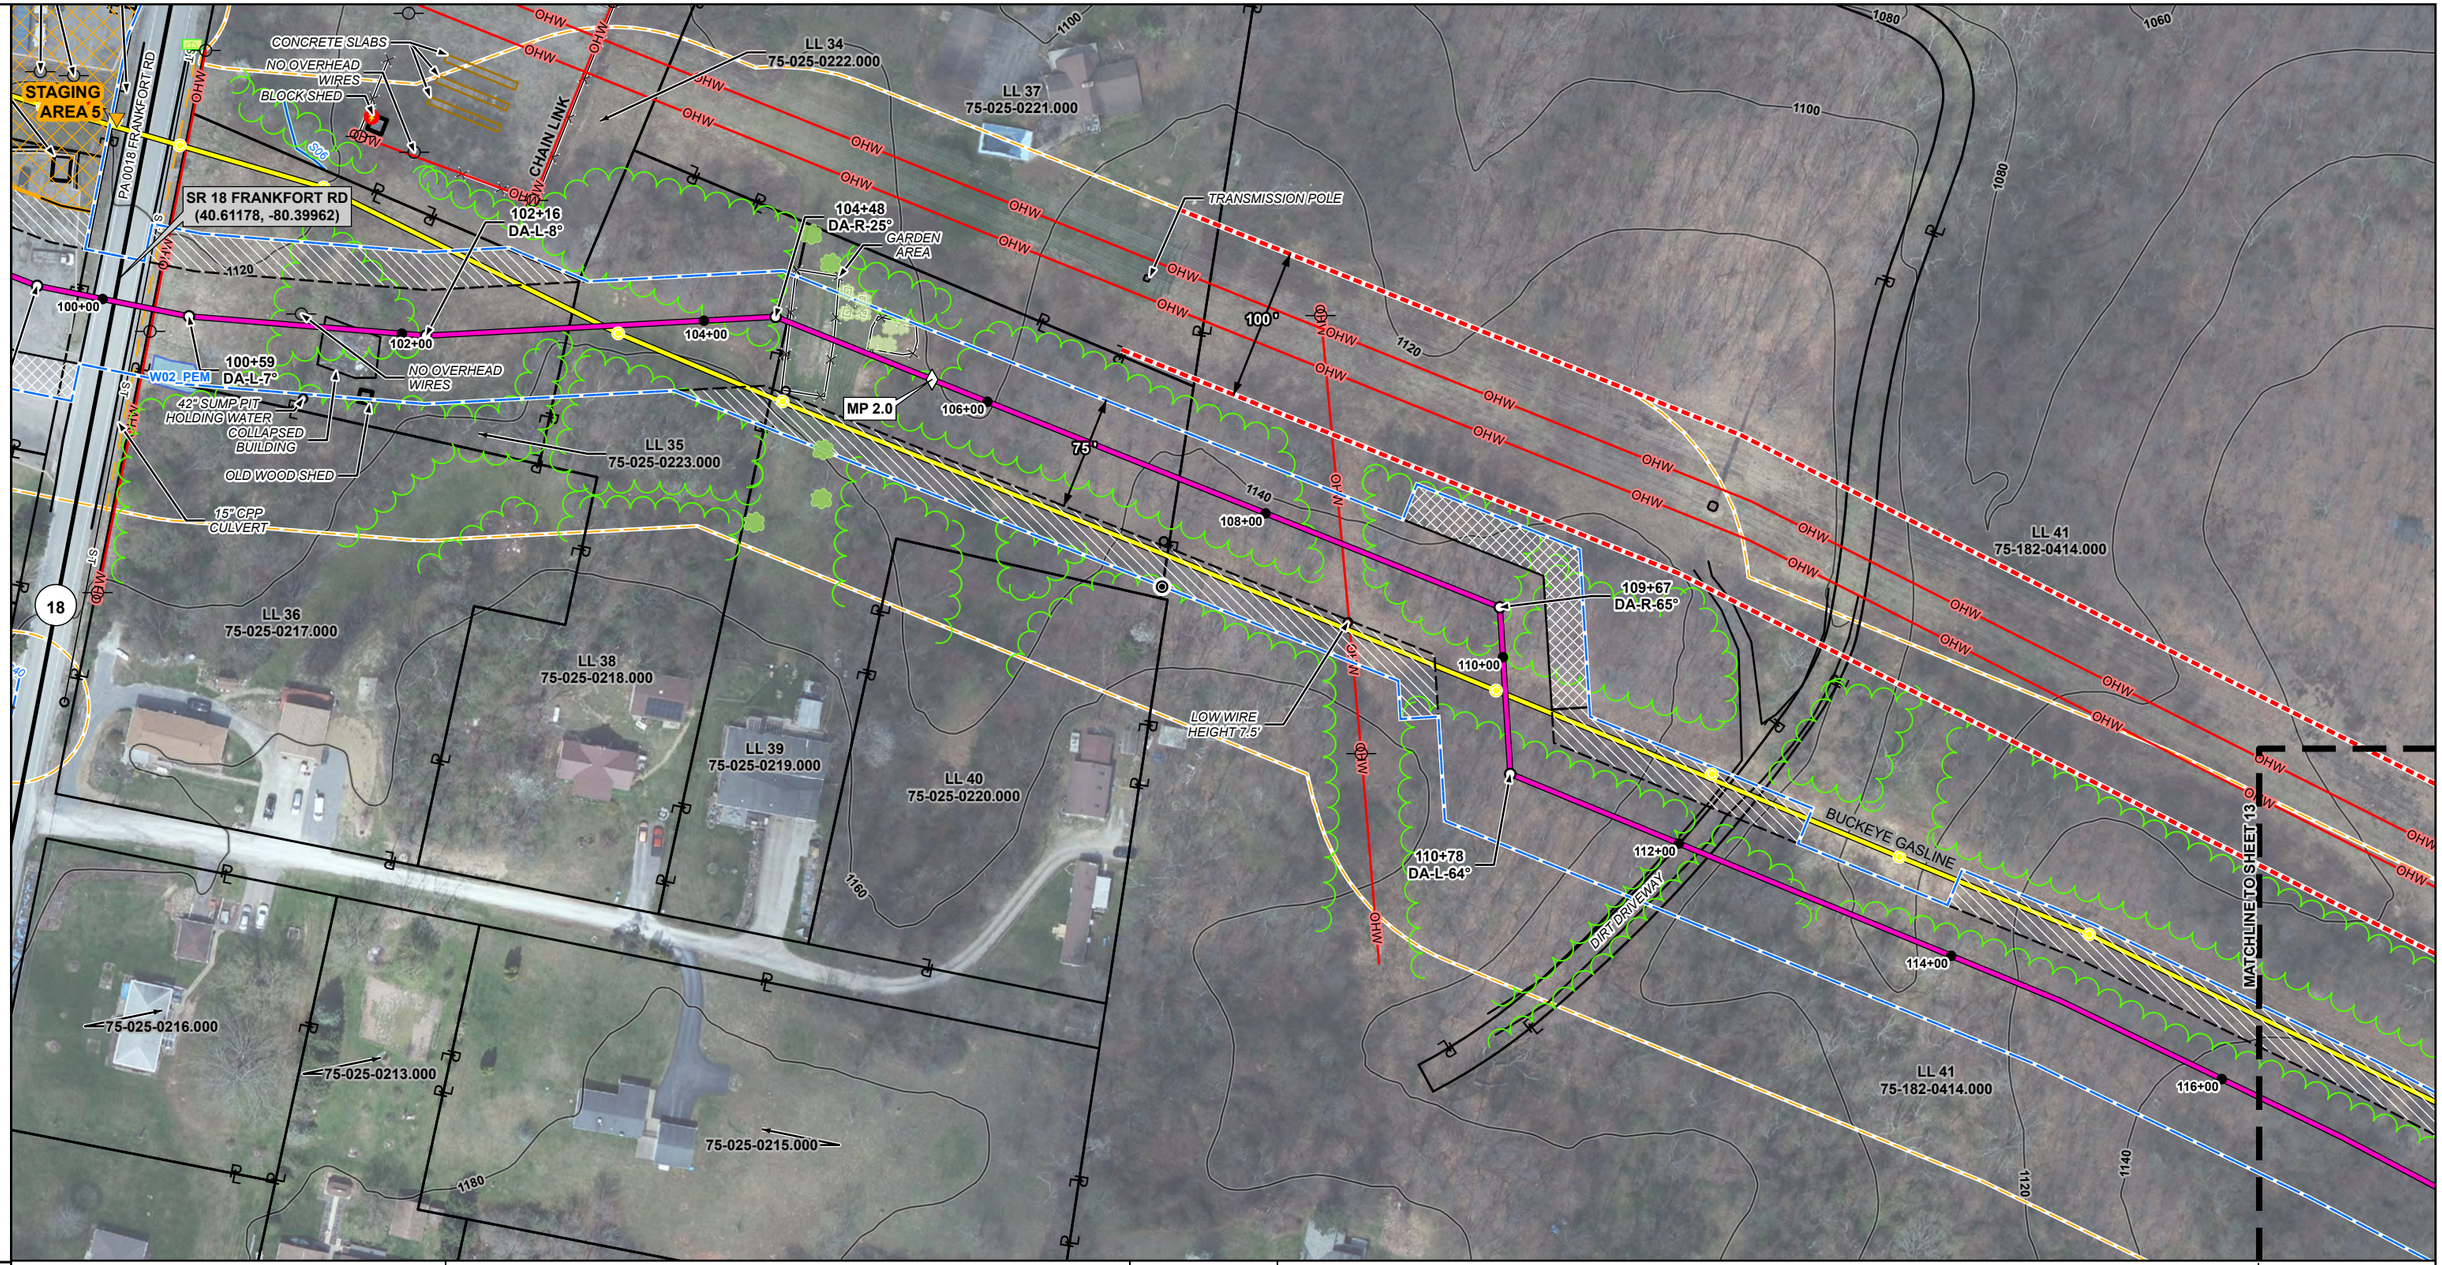

FOOTAGE	106'	1152'	20'	411'	
WALL THICKNESS	24"-0.562WT	24"-0.500WT	24"-0.562WT	24"-0.500WT	
GRADE	X-65	X-65	X-65	X-65	
COATING	PWR	FBE	PWR	FBE	
	99+38 MATCHLINE	100+44	111+96	112+16	116+27 MATCHLINE

N W E S

ISSUED FOR FERC

National Fuel® Supply Corporation

0 100 200 Feet

National Fuel Supply Corporation
Shippingport Lateral Project
Raccoon Township
Beaver County
Pennsylvania

REV
P

DRAWN BY : KEYSTONE CONSULTANTS, LLC
CHECKED BY : D. MCINTIRE
SCALE : 1 =100 feet
DATE : 8/21/2025

12
34

PIPELINE

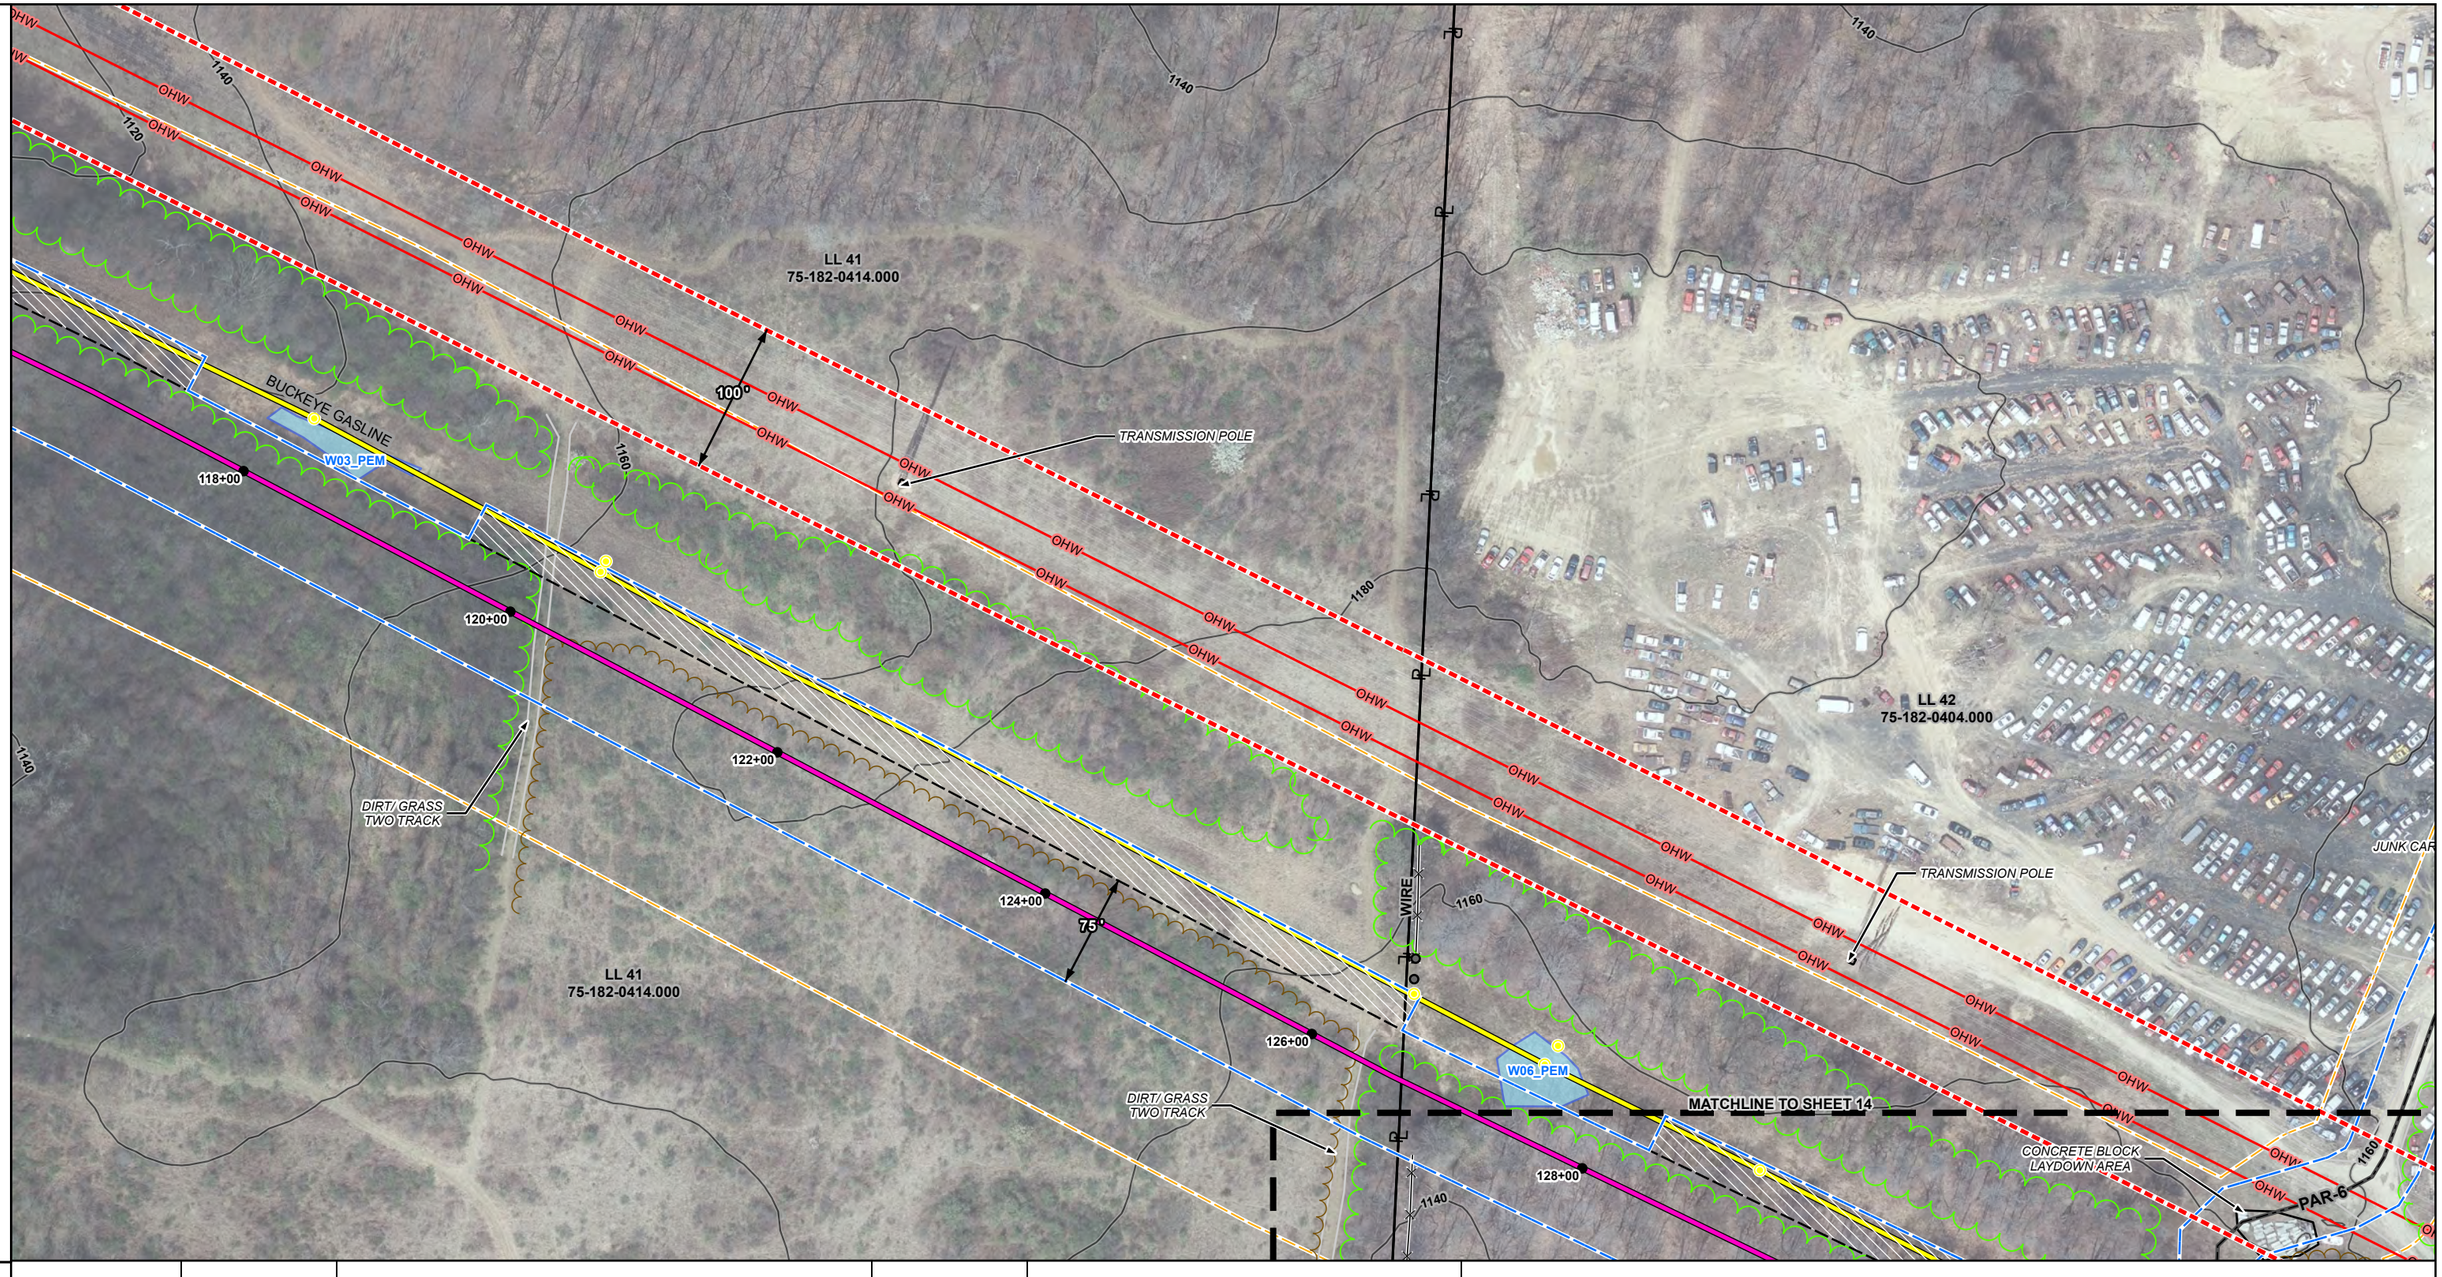

FOOTAGE	387'	20'	591'	20'	71'	
WALL THICKNESS	24"-0.500WT	24"-0.562WT	24"-0.500WT	24"-0.562WT	24"-0.500WT	
GRADE	X-65	X-65	X-65	X-65	X-65	
COATING	FBE	PWR	FBE	PWR	FBE	
	116+27 MATCHLINE	120+14	120+34	126+25	126+45	127+16 MATCHLINE

N W E S

ISSUED FOR FERC

National Fuel® Supply Corporation

0 100 200 Feet

National Fuel Supply Corporation
Shippingport Lateral Project

Raccoon Township
Beaver County
Pennsylvania

REV P

DRAWN BY : KEYSTONE CONSULTANTS, LLC
CHECKED BY : D. MCINTIRE
SCALE : 1 =100 feet
DATE : 8/21/2025

13
34

PIPELINE

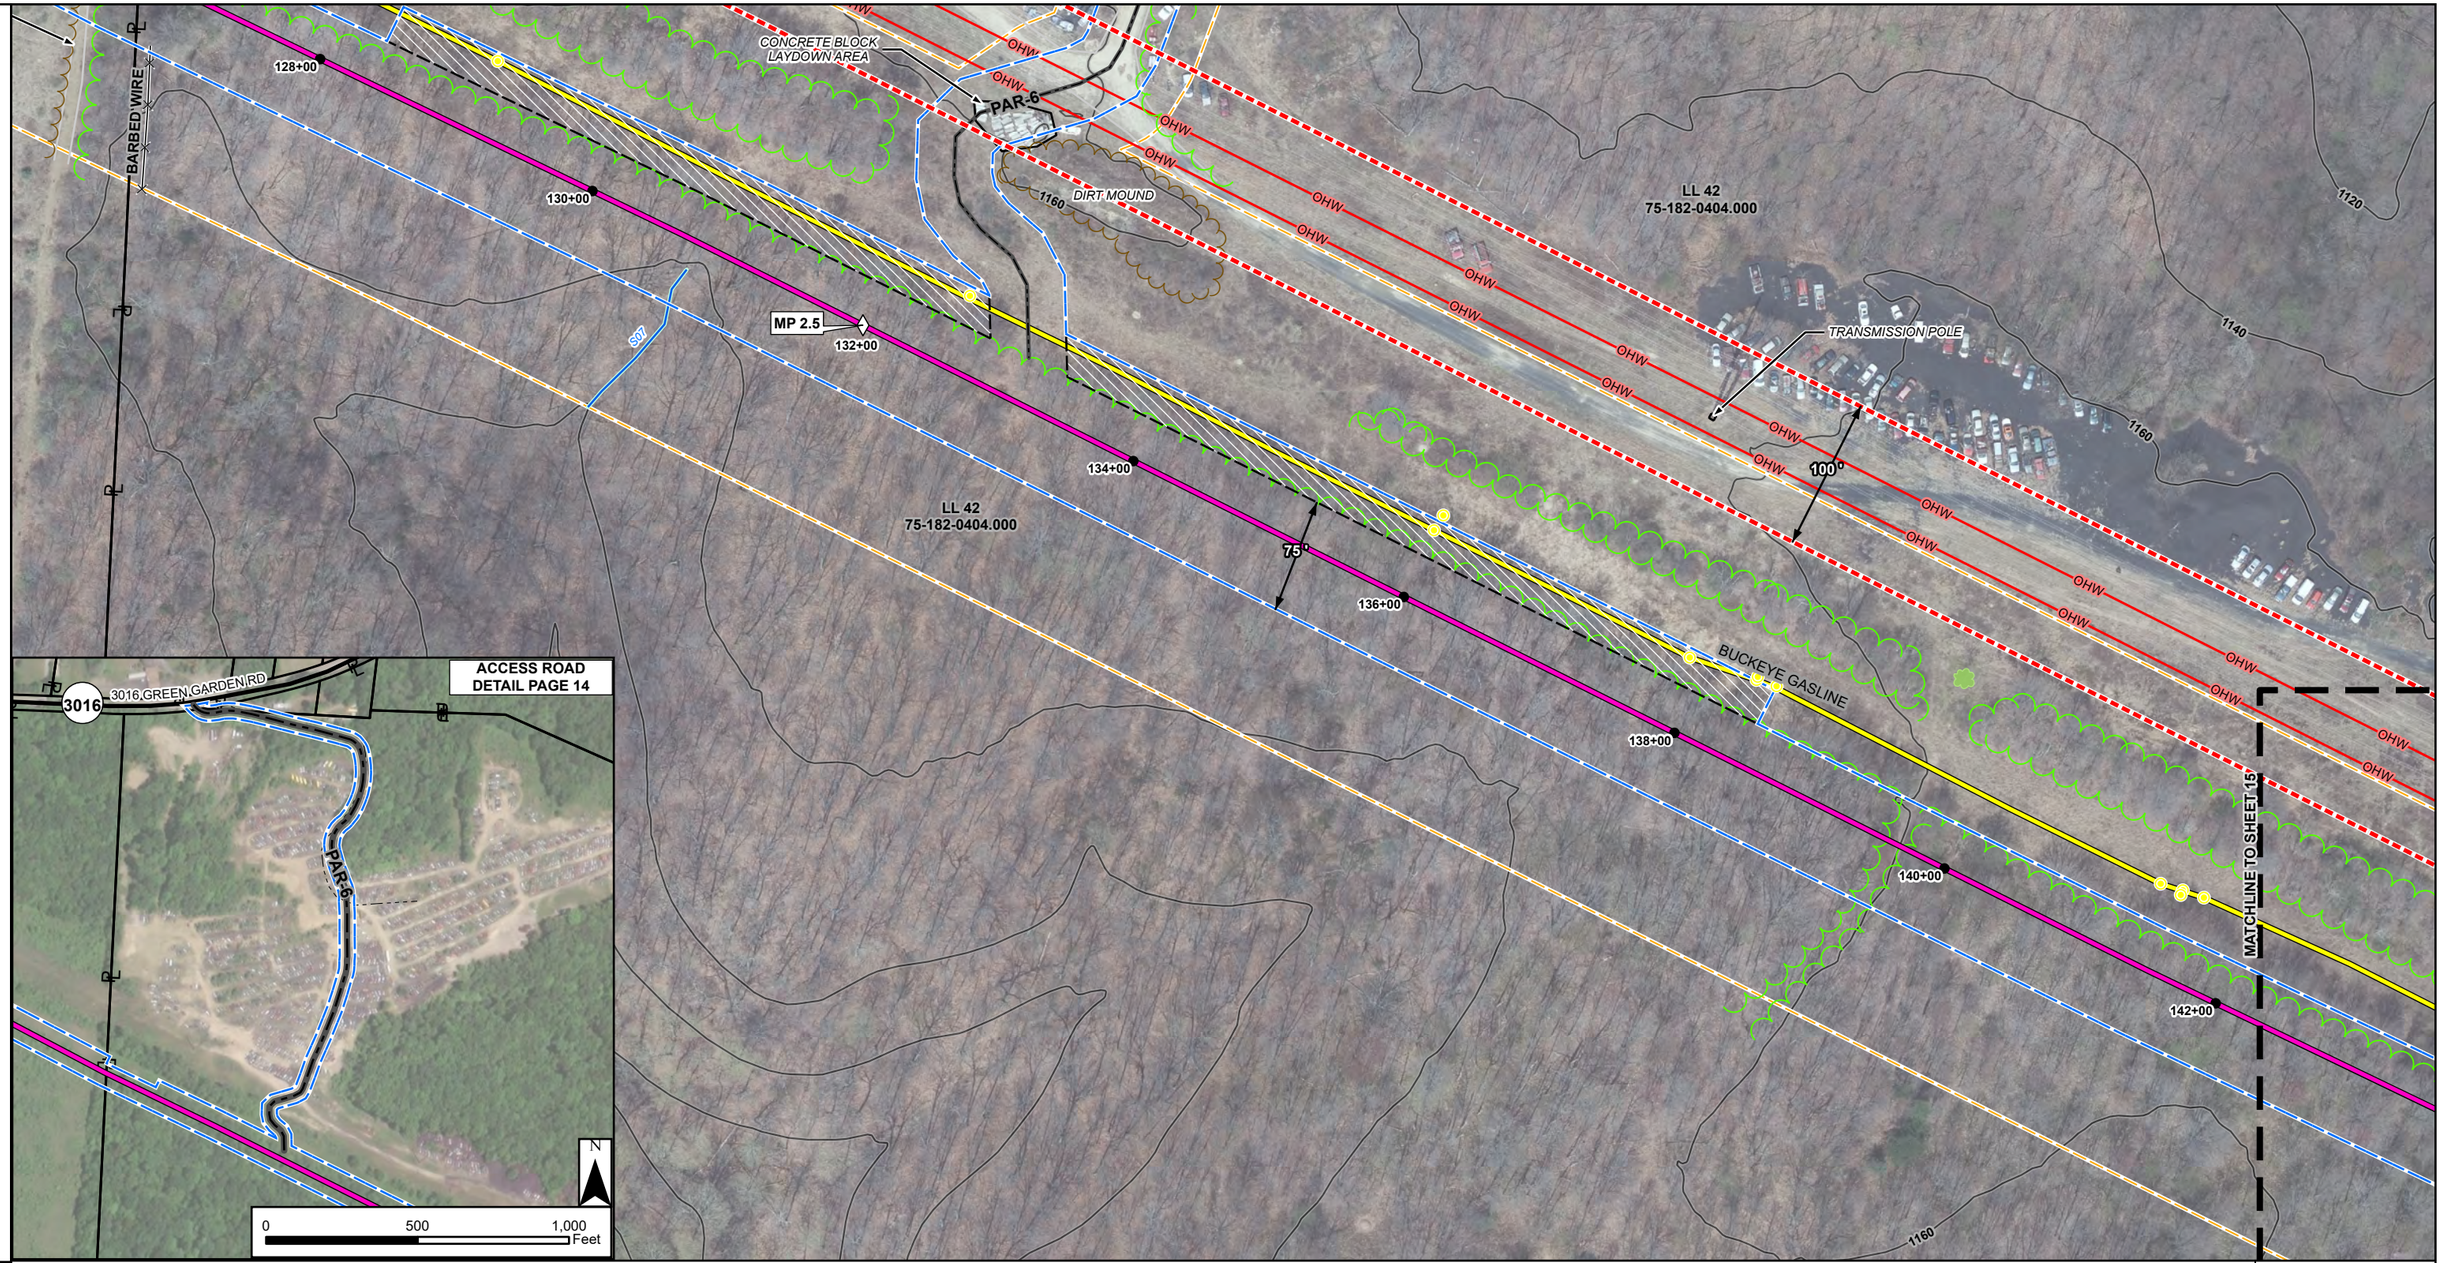

FOOTAGE	1516'
WALL THICKNESS	24"-0.500WT
GRADE	X-65
COATING	FBE

127+16 MATCHLINE

142+32 MATCHLINE

N W E S

ISSUED FOR FERC

National Fuel® Supply Corporation

0 100 200 Feet

National Fuel Supply Corporation
Shippingport Lateral Project

Raccoon Township
Beaver County
Pennsylvania

REV
P

DRAWN BY : KEYSTONE CONSULTANTS. LLC
CHECKED BY : D. MCINTIRE
SCALE : 1 =100 feet
DATE : 8/21/2025

14
34

PIPELINE

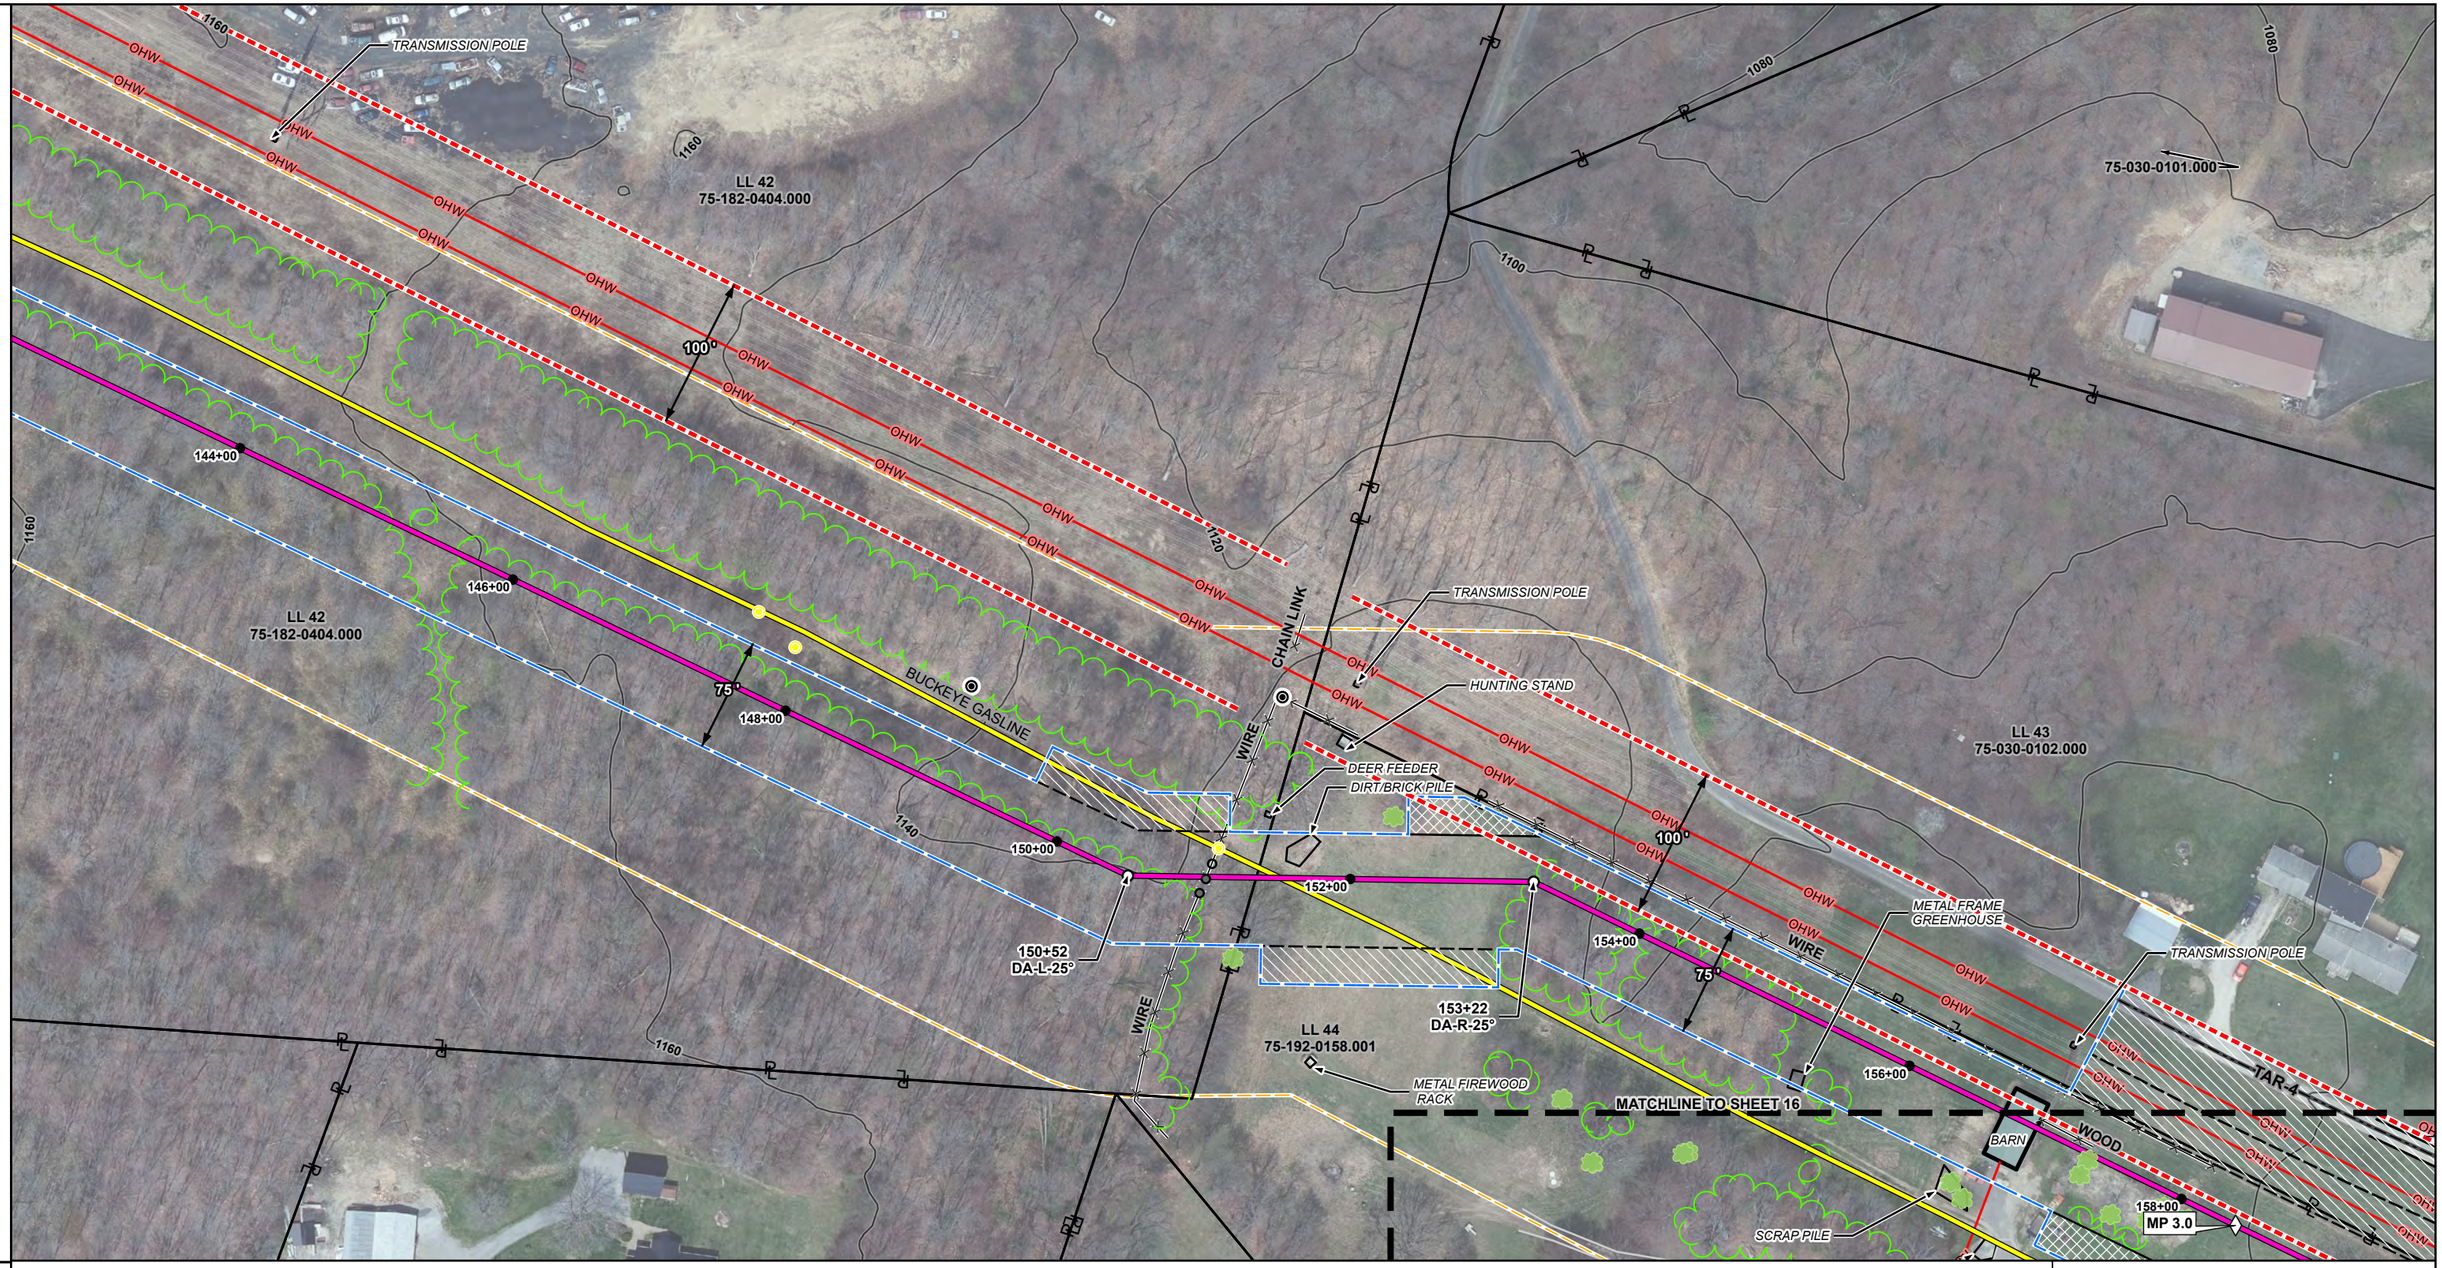

FOOTAGE	1439'
WALL THICKNESS	24"-0.500WT
GRADE	X-65
COATING	FBE

142+32 MATCHLINE

156+71 MATCHLINE

N W E S

ISSUED FOR FERC

National Fuel® Supply Corporation

0 100 200 Feet

National Fuel Supply Corporation
Shippingport Lateral Project

Raccoon Township
Beaver County
Pennsylvania

REV

P

DRAWN BY : KEYSTONE CONSULTANTS, LLC

CHECKED BY : D. MCINTIRE

SCALE : 1 =100 feet

DATE : 8/21/2025

15

34

PIPELINE

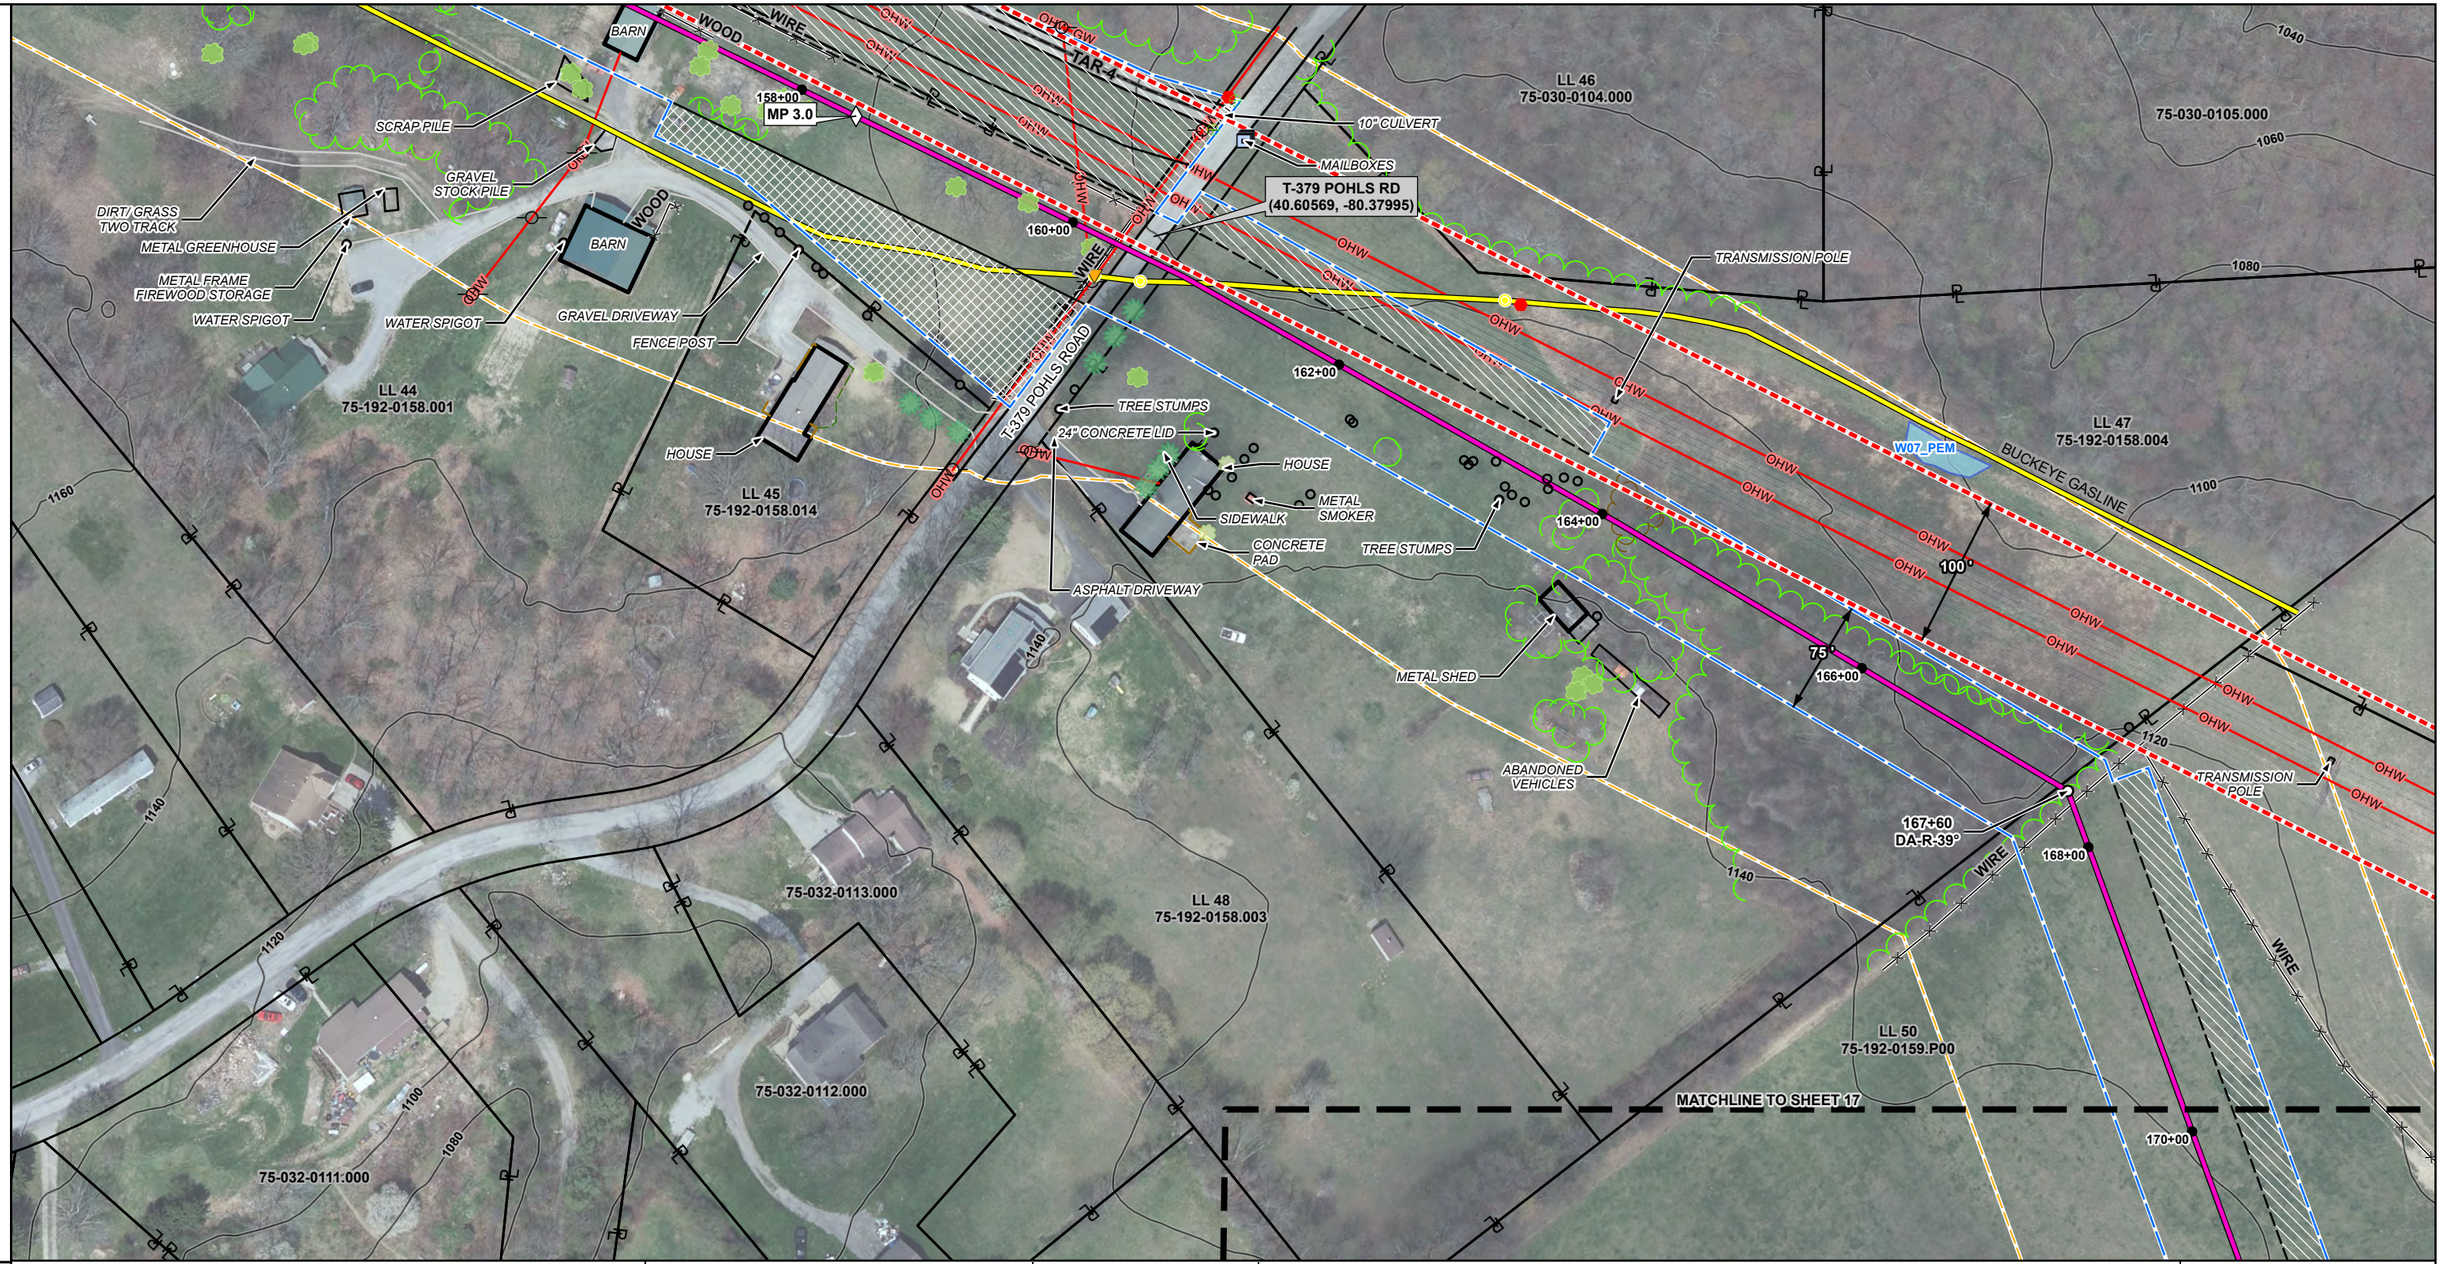

FOOTAGE		358'	40'	916'
WALL THICKNESS		24"-0.500WT	24"-0.562WT	24"-0.500WT
GRADE	156+71 MATCHLINE	X-65	X-65	X-65
COATING	160+29	FBE	PWR	FBE
	160+69			169+85 MATCHLINE

N W E S

ISSUED FOR FERC

National Fuel® Supply Corporation

0 100 200 Feet

National Fuel Supply Corporation
Shippingport Lateral Project

Raccoon Township
Beaver County
Pennsylvania

REV
P

DRAWN BY : KEYSTONE CONSULTANTS. LLC
CHECKED BY : D. MCINTIRE
SCALE : 1 =100 feet
DATE : 8/21/2025

16
34

PIPELINE

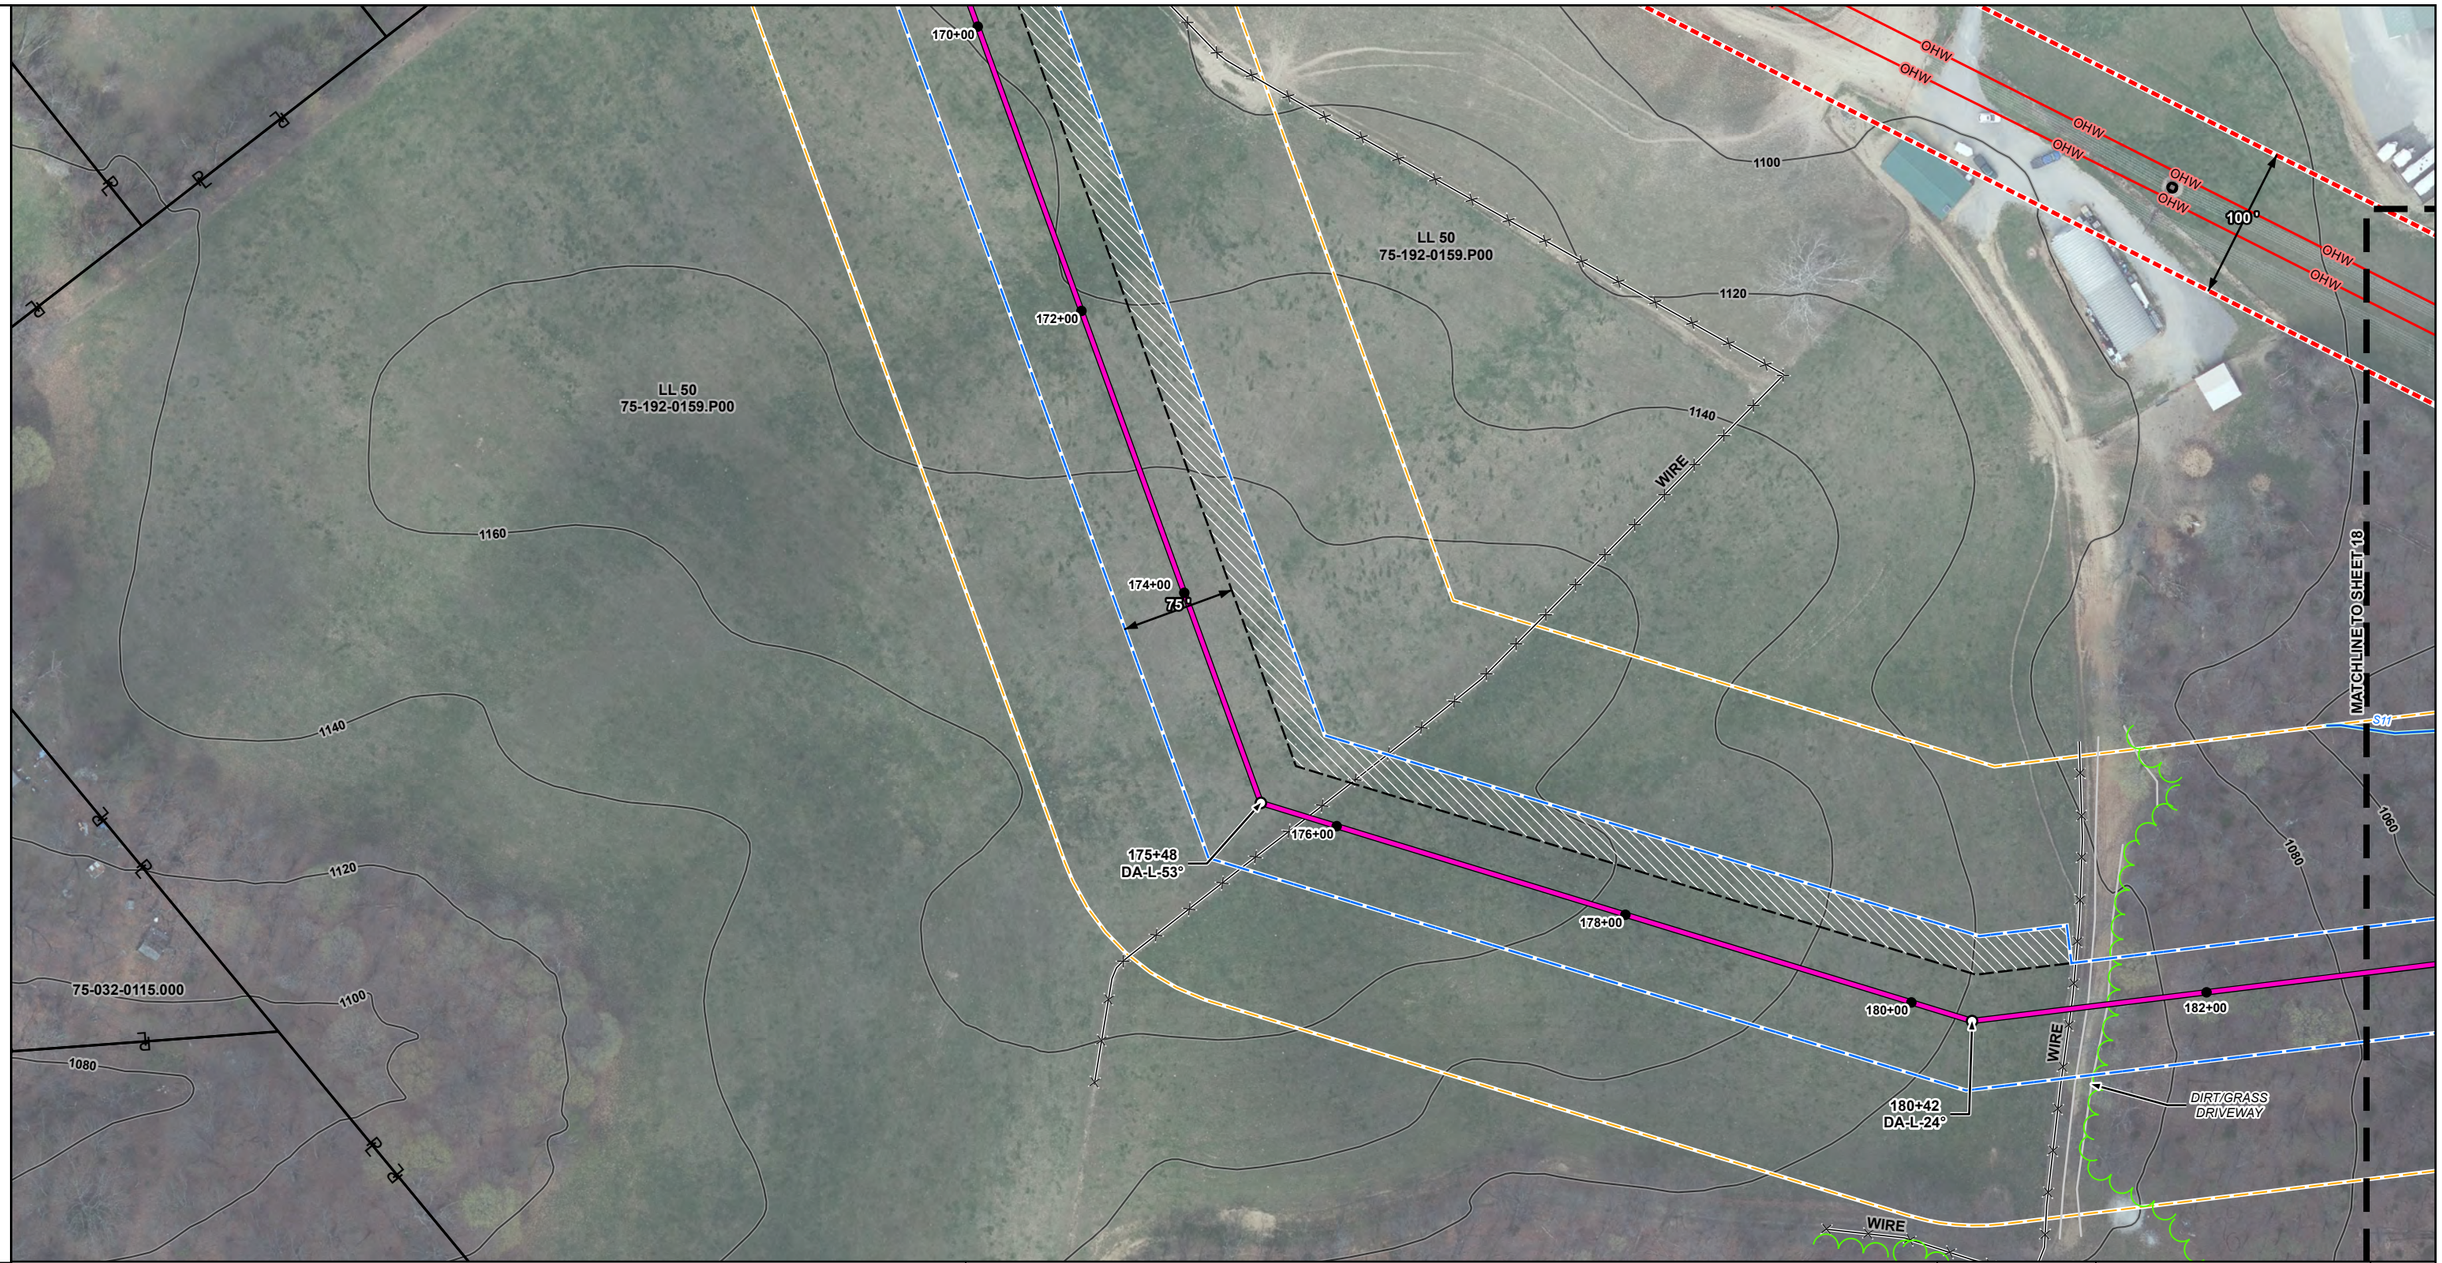

FOOTAGE	169+85 MATCHLINE	1132'	181+17	20'	181+37	172'	183+09 MATCHLINE
WALL THICKNESS		24"-0.500WT		24"-0.562WT		24"-0.500WT	
GRADE		X-65		X-65		X-65	
COATING		FBE		PWR		FBE	

N W E S

ISSUED FOR FERC

National Fuel® Supply Corporation

0 100 200 Feet

National Fuel Supply Corporation
Shippingport Lateral Project

Raccoon Township
Beaver County
Pennsylvania

REV P

DRAWN BY : KEYSTONE CONSULTANTS. LLC
CHECKED BY : D. MCINTIRE
SCALE : 1 =100 feet
DATE : 8/21/2025

17 / 34

PIPELINE

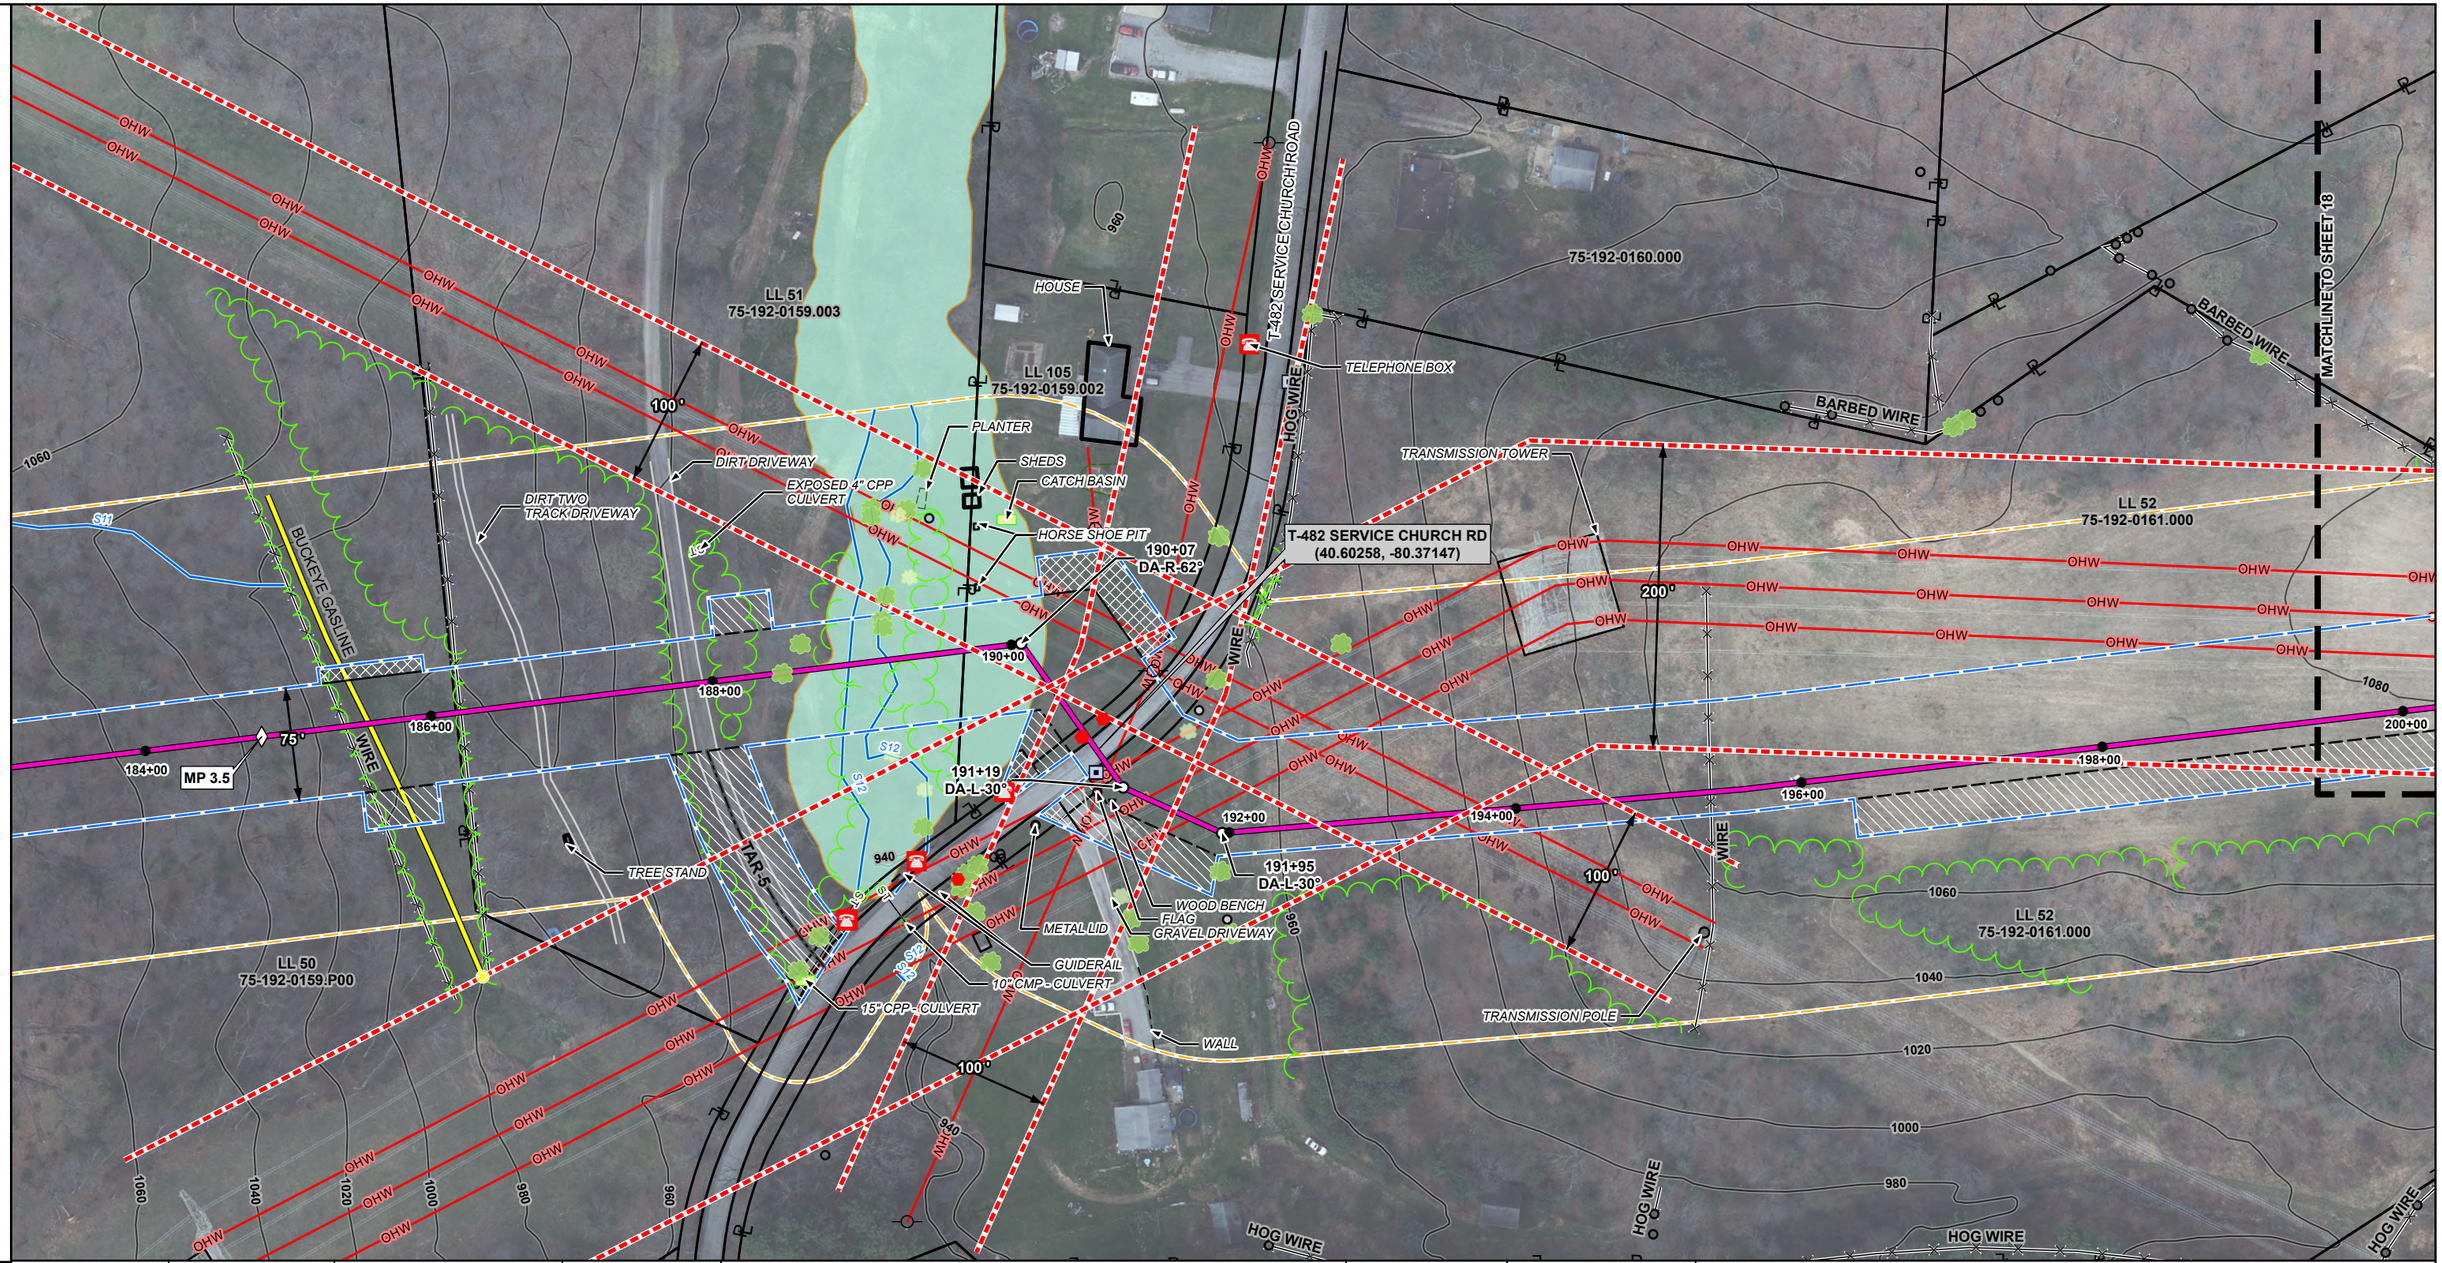

FOOTAGE	357'	20'	86'	30'	259'	65'	74'	40'	703'	
WALL THICKNESS	183+09 MATCHLINE	24"-0.500WT	186+66	24"-0.562WT	186+86	24"-0.500WT	187+72	24"-0.562WT	188+02	24"-0.500WT	190+61	24"-0.562WT	191+26	24"-0.500WT	192+00	24"-0.562WT	192+40	24"-0.500WT	199+43 MATCHLINE
GRADE	X-65	X-65	X-65	X-65	X-65	X-65	X-65	X-65	X-65	
COATING	FBE	PWR	FBE	PWR	FBE	PWR	FBE	PWR	FBE	

N W E S

ISSUED FOR FERC

National Fuel® Supply Corporation

0 100 200 Feet

National Fuel Supply Corporation
Shippingport Lateral Project

Raccoon Township
Beaver County
Pennsylvania

REV
P

DRAWN BY : KEYSTONE CONSULTANTS, LLC
CHECKED BY : D. MCINTIRE
SCALE : 1 =100 feet
DATE : 8/21/2025

18
34

PIPELINE

FOOTAGE	1196'		70'	349'
WALL THICKNESS	24"-0.500WT		24"-0.562WT	24"-0.500WT
GRADE	X-65		X-65	X-65
COATING	FBE		PWR	FBE

199+43 MATCHLINE

211+39

212+09

215+58 MATCHLINE

ISSUED FOR FERC

National Fuel® Supply Corporation

0 100 200 Feet

National Fuel Supply Corporation
Shippingport Lateral Project

Raccoon Township
Beaver County
Pennsylvania

REV P

DRAWN BY : KEYSTONE CONSULTANTS, LLC
CHECKED BY : D. MCINTIRE
SCALE : 1 =100 feet
DATE : 8/21/2025

19 / 34

PIPELINE

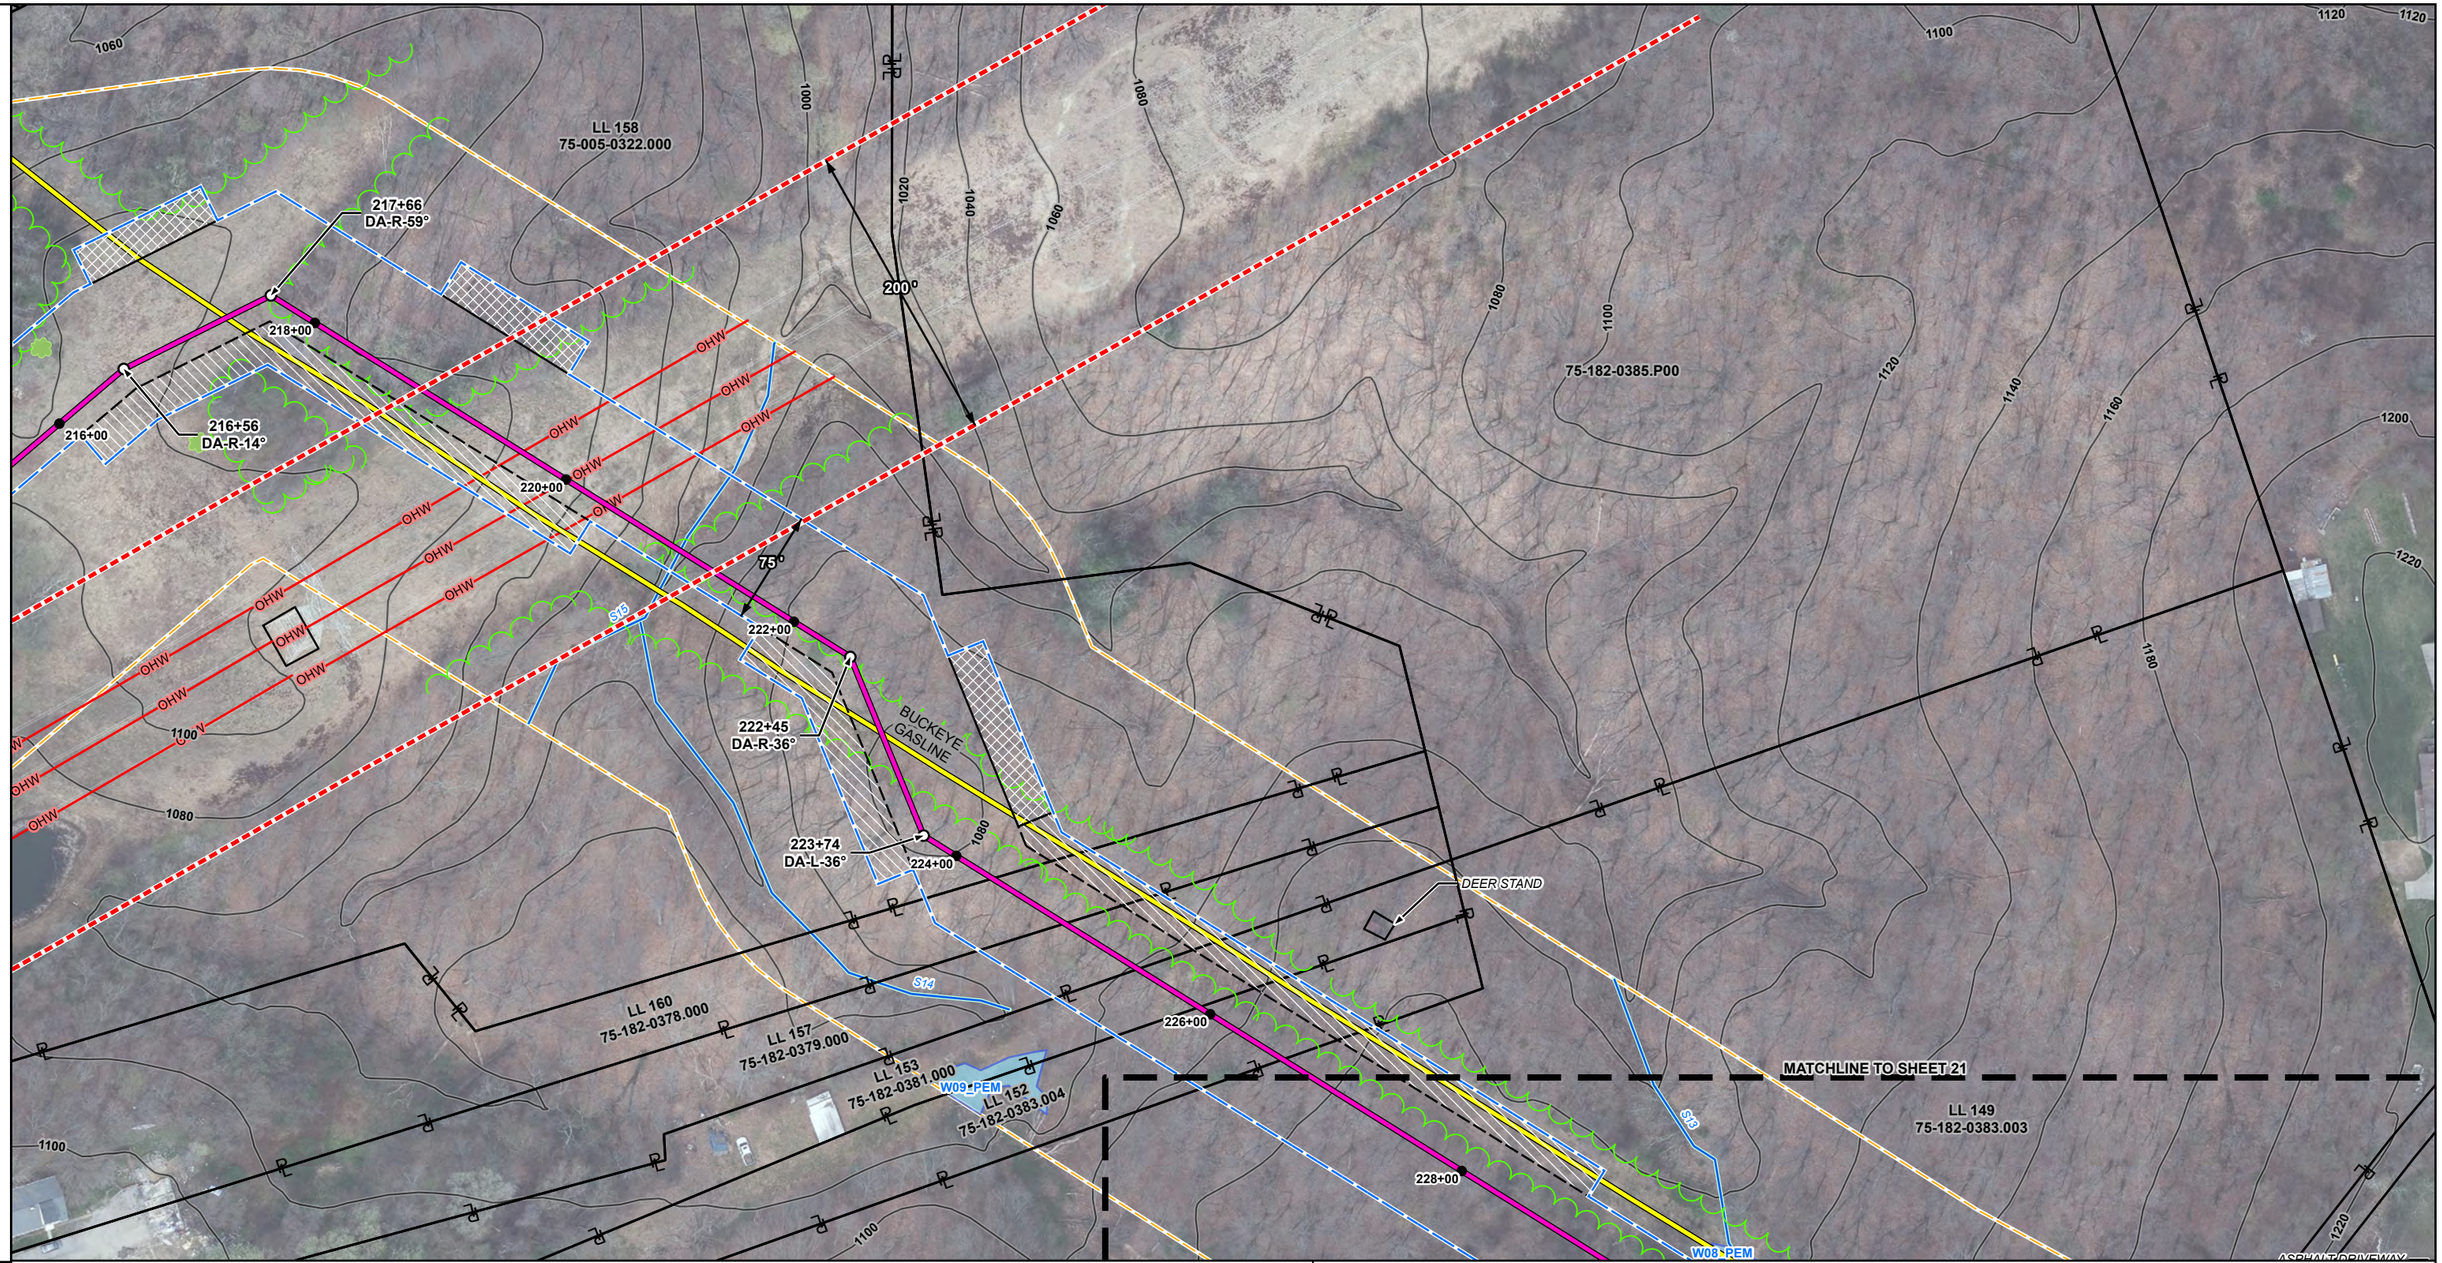

FOOTAGE	1123'	
WALL THICKNESS	24"-0.500WT	
GRADE	X-65	
COATING	FBE	

215+58 MATCHLINE

226+81 MATCHLINE

N W E S

ISSUED FOR FERC

National Fuel® Supply Corporation

0 100 200 Feet

National Fuel Supply Corporation
Shippingport Lateral Project

Raccoon Township
Beaver County
Pennsylvania

REV P

DRAWN BY : KEYSTONE CONSULTANTS. LLC
CHECKED BY : D. MCINTIRE
SCALE : 1 =100 feet
DATE : 8/21/2025

PIPELINE

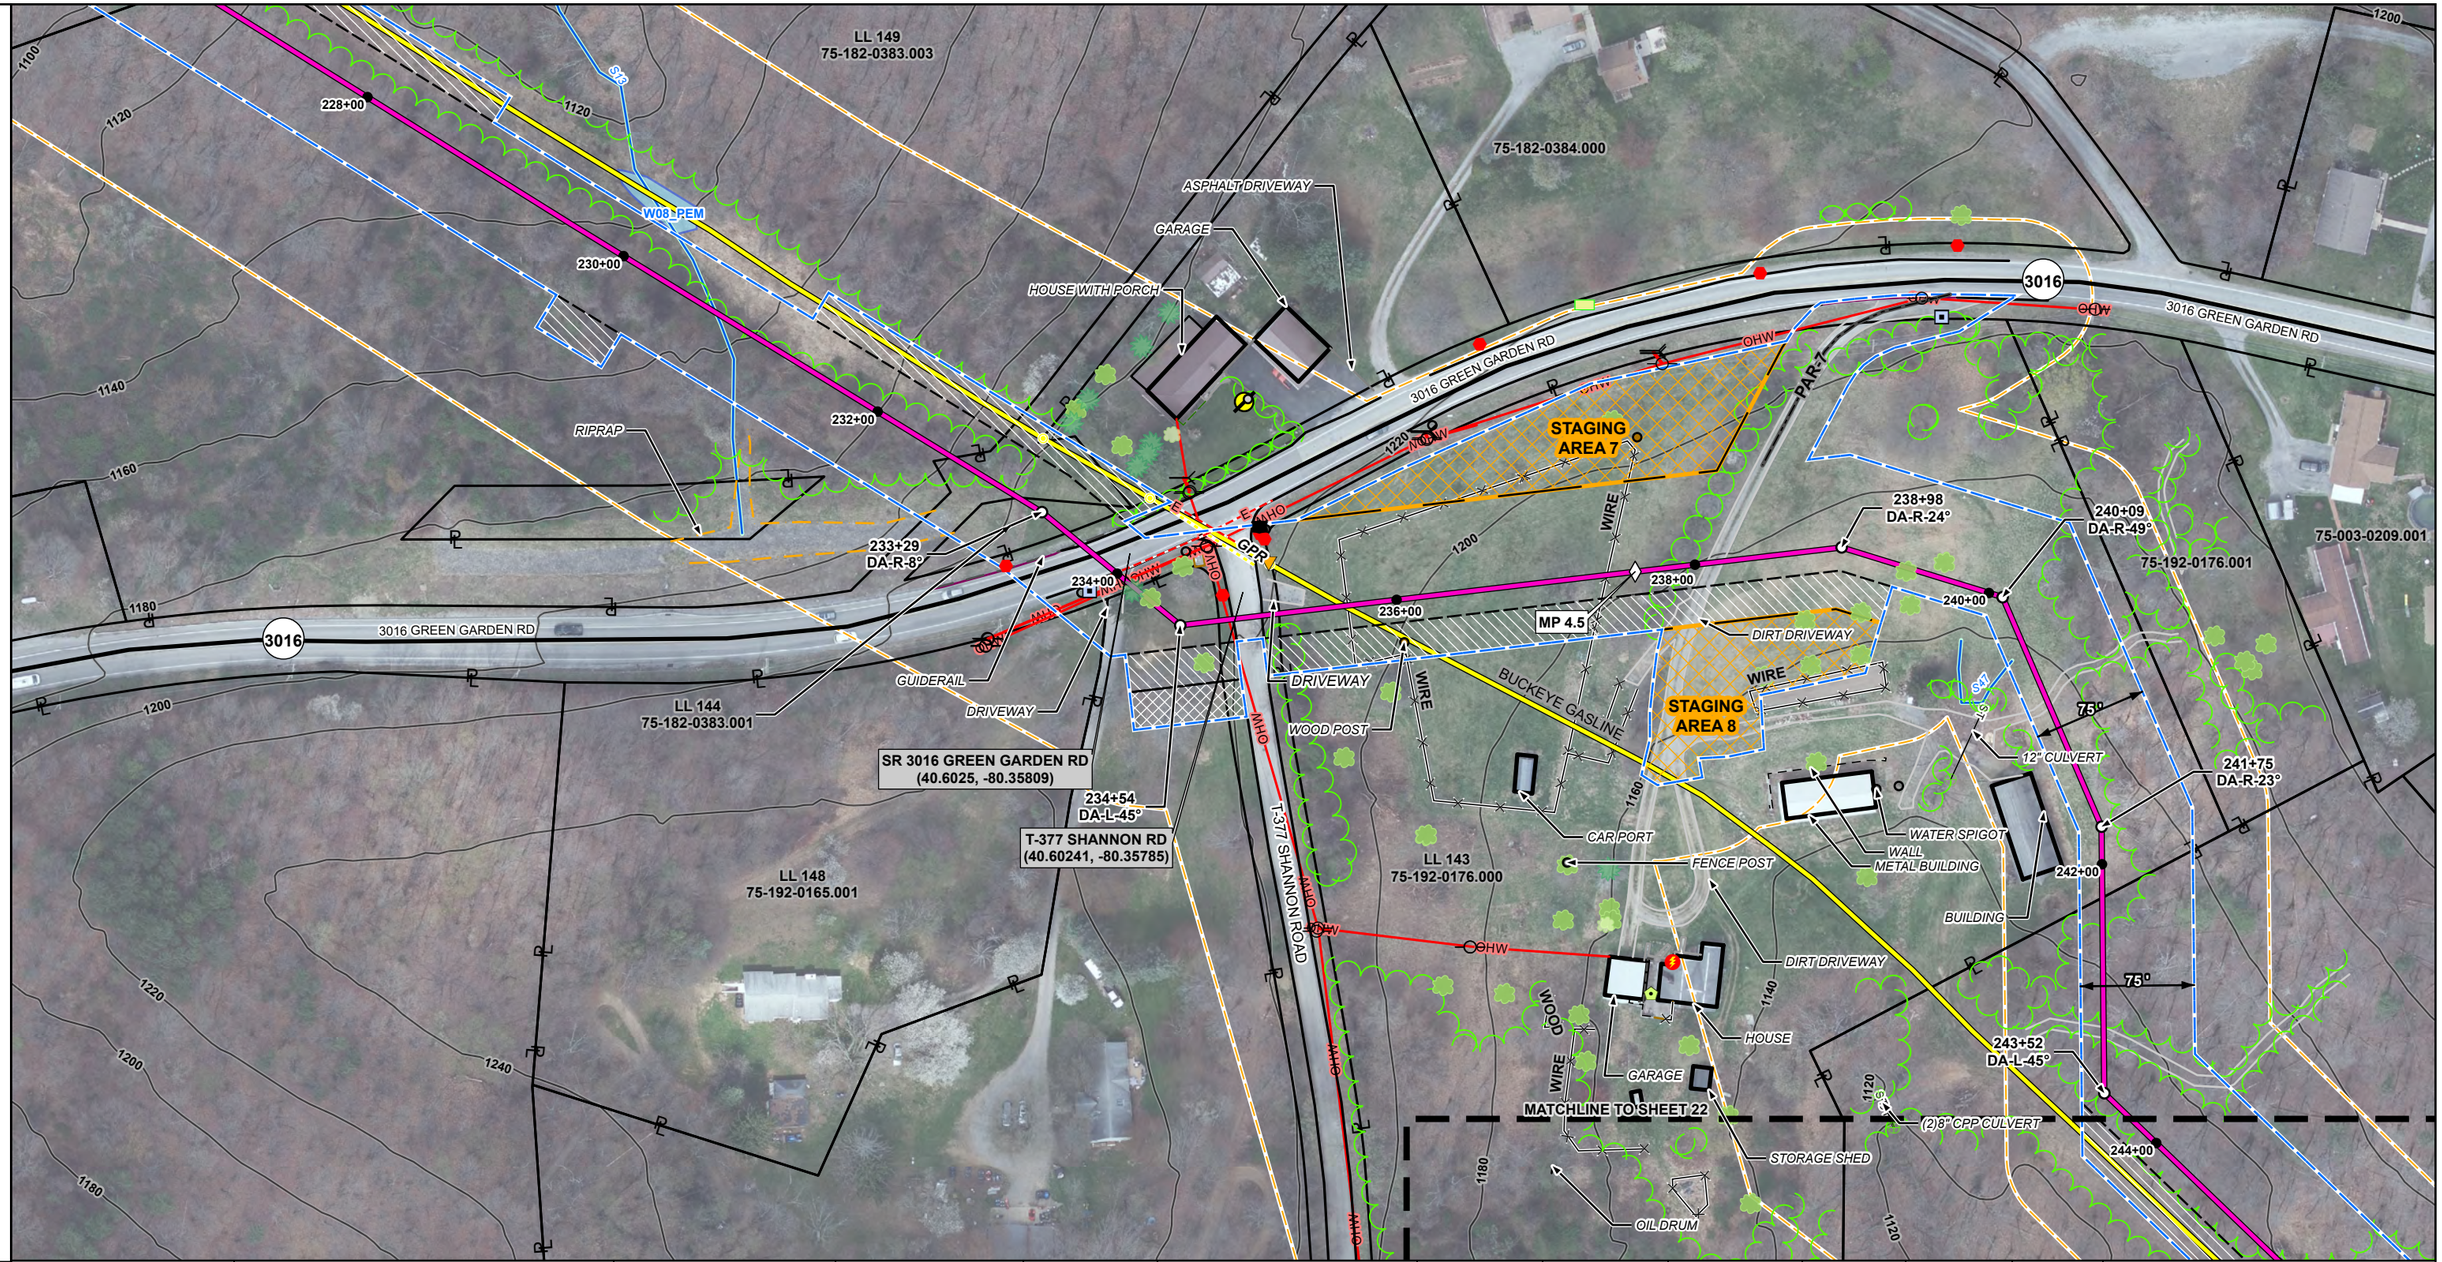

FOOTAGE		636'	130'	33'	40'	273'	40'	241'	20'	208'	20'	55'	
WALL THICKNESS	226+81 MATCHLINE	24"-0.500WT	233+17 24"-0.562WT	234+47 24"-0.500WT	234+80 24"-0.562WT	235+20 24"-0.500WT	237+93 24"-0.562WT	238+33 24"-0.500WT	240+74 24"-0.562WT	240+94 24"-0.500WT	243+02 24"-0.562WT	243+22 24"-0.500WT	243+77 MATCHLINE
GRADE		X-65	X-65	X-65	X-65	X-65	X-65	X-65	X-65	X-65	X-65	X-65	
COATING		FBE	PWR	FBE	PWR	FBE	PWR	FBE	PWR	FBE	PWR	FBE	

N W E S

ISSUED FOR FERC

National Fuel® Supply Corporation

0 100 200 Feet

National Fuel Supply Corporation
Shippingport Lateral Project

Raccoon Township
Beaver County
Pennsylvania

REV
P

DRAWN BY : KEYSTONE CONSULTANTS. LLC
CHECKED BY : D. MCINTIRE
SCALE : 1 =100 feet
DATE : 8/21/2025

21
34

PIPELINE

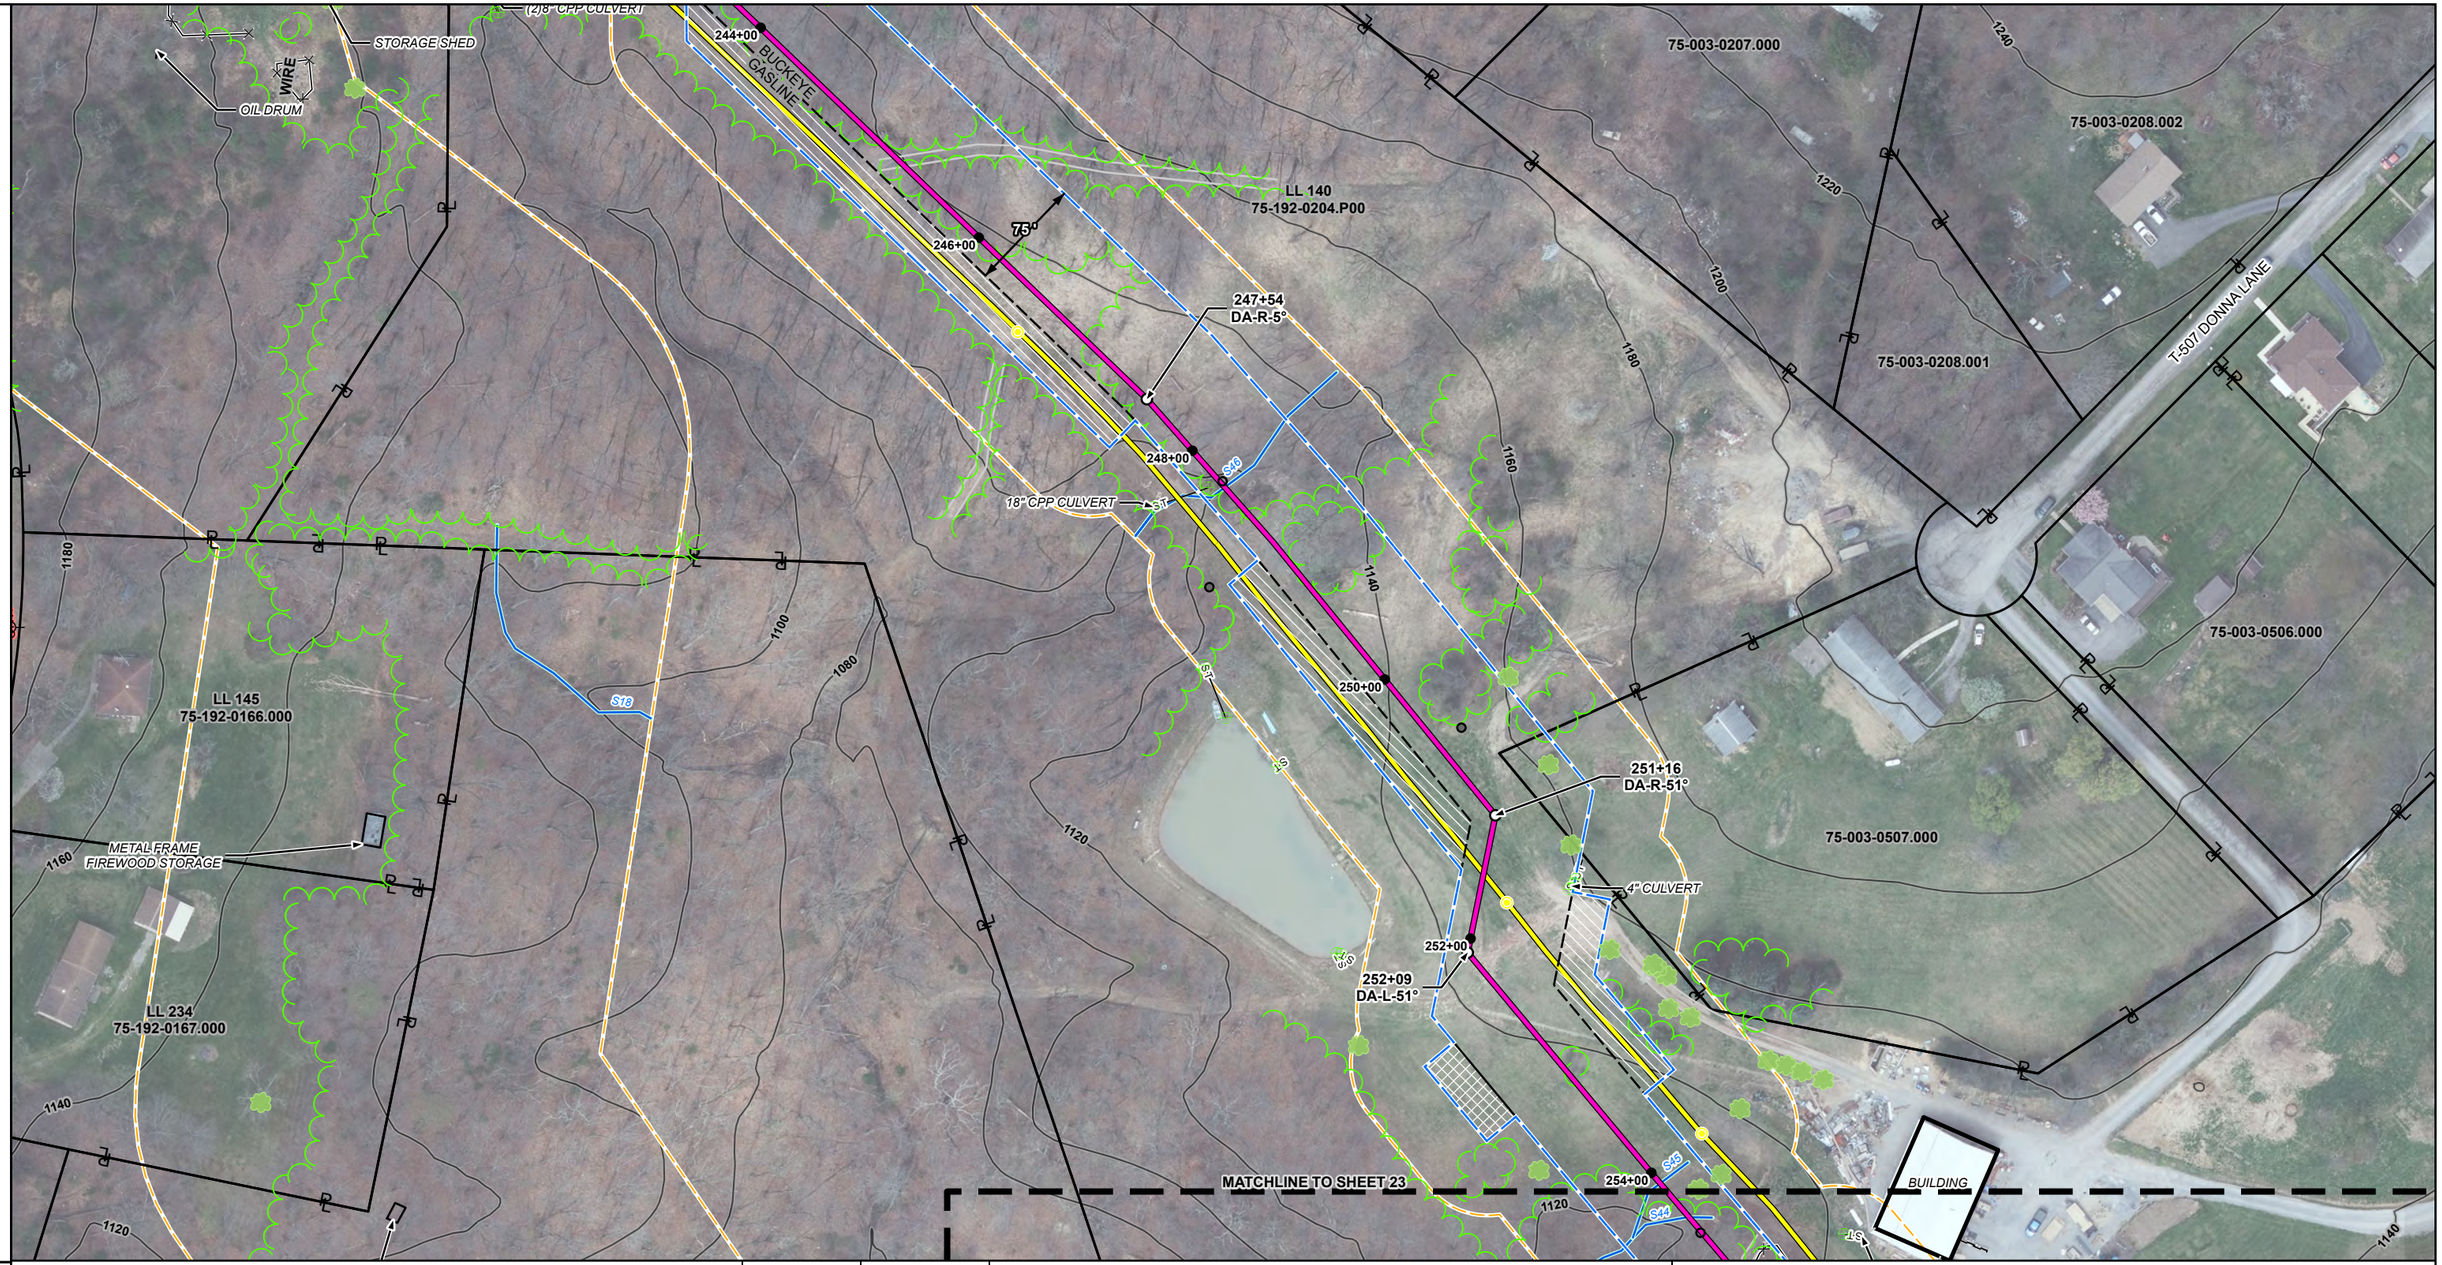

FOOTAGE		141'	20'	878'	
WALL THICKNESS		24"-0.500WT	24"-0.562WT	24"-0.500WT	
GRADE	243+77 MATCHLINE	X-65	X-65	X-65	254+16 MATCHLINE
COATING		FBE	PWR	FBE	

245+18 | 245+38

N W E S

ISSUED FOR FERC

National Fuel® Supply Corporation

0 100 200 Feet

National Fuel Supply Corporation
Shippingport Lateral Project

Raccoon Township
Beaver County
Pennsylvania

REV
P

DRAWN BY : KEYSTONE CONSULTANTS. LLC
CHECKED BY : D. MCINTIRE
SCALE : 1 =100 feet
DATE : 8/21/2025

PIPELINE

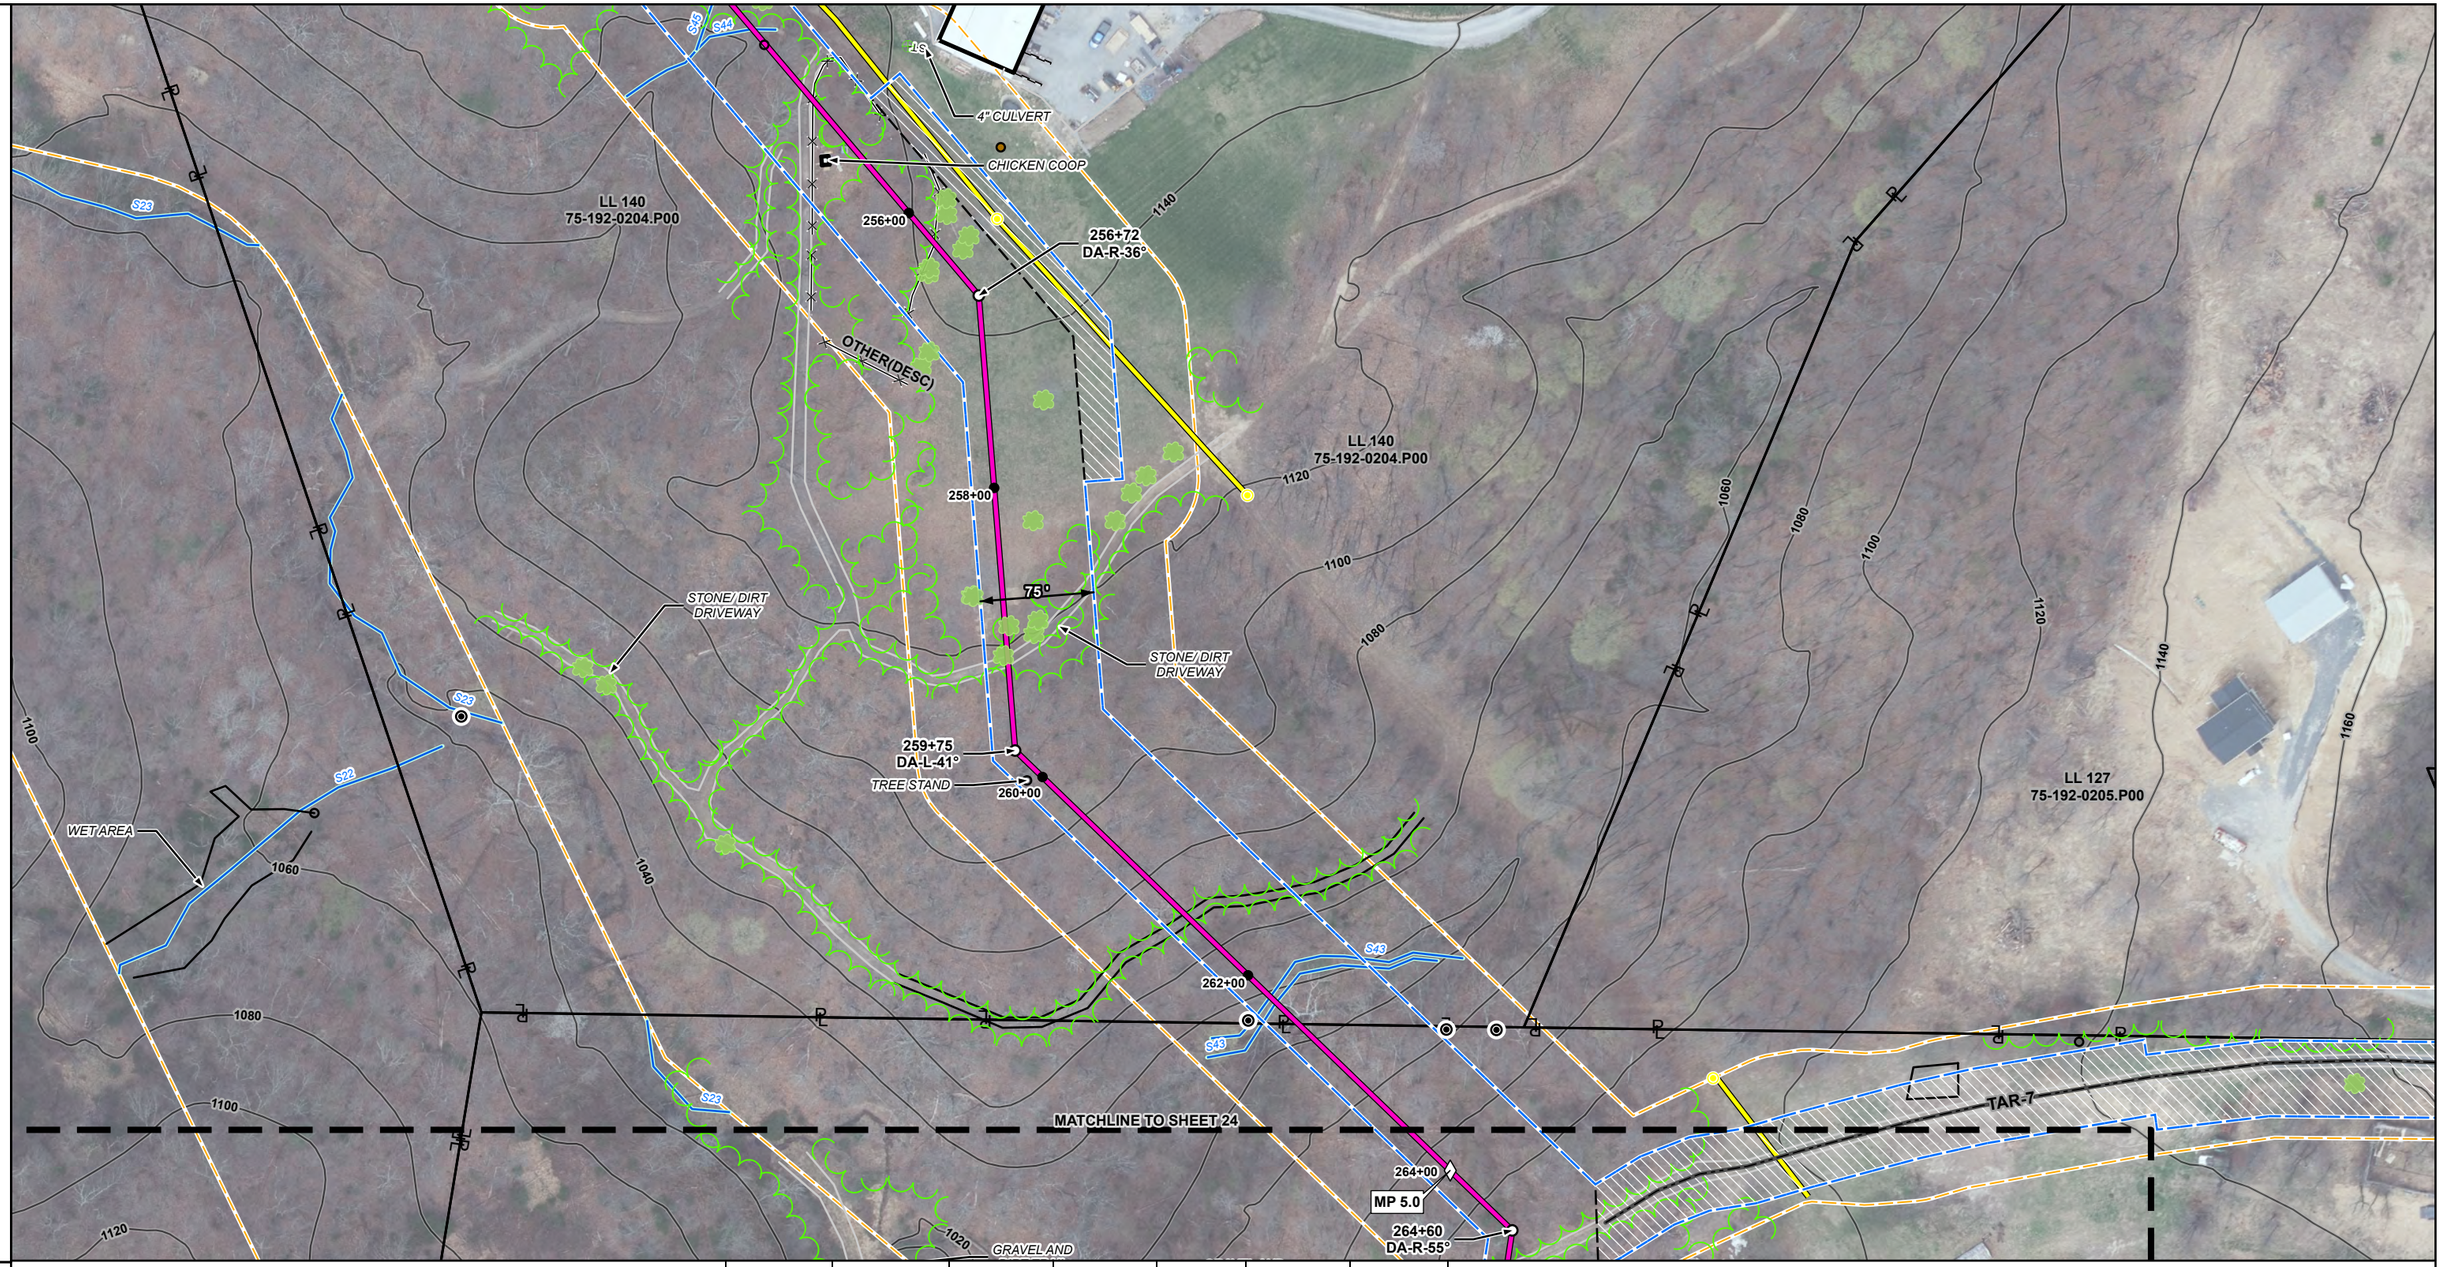

FOOTAGE		69'	20'	400'	20'	207'	20'	206'	
WALL THICKNESS		24"-0.500WT	24"-0.562WT	24"-0.500WT	24"-0.562WT	24"-0.500WT	24"-0.562WT	24"-0.500WT	
GRADE	254+16 MATCHLINE	X-65	X-65	X-65	X-65	X-65	X-65	X-65	263+58 MATCHLINE
COATING		FBE	PWR	FBE	PWR	FBE	PWR	FBE	
		254+85	255+05	259+05	259+25	261+32	261+52		

N W E S

ISSUED FOR FERC

National Fuel® Supply Corporation

0 100 200 Feet

National Fuel Supply Corporation
Shippingport Lateral Project

Raccoon Township
Beaver County
Pennsylvania

REV
P

DRAWN BY : KEYSTONE CONSULTANTS. LLC
CHECKED BY : D. MCINTIRE
SCALE : 1 =100 feet
DATE : 8/21/2025

PIPELINE

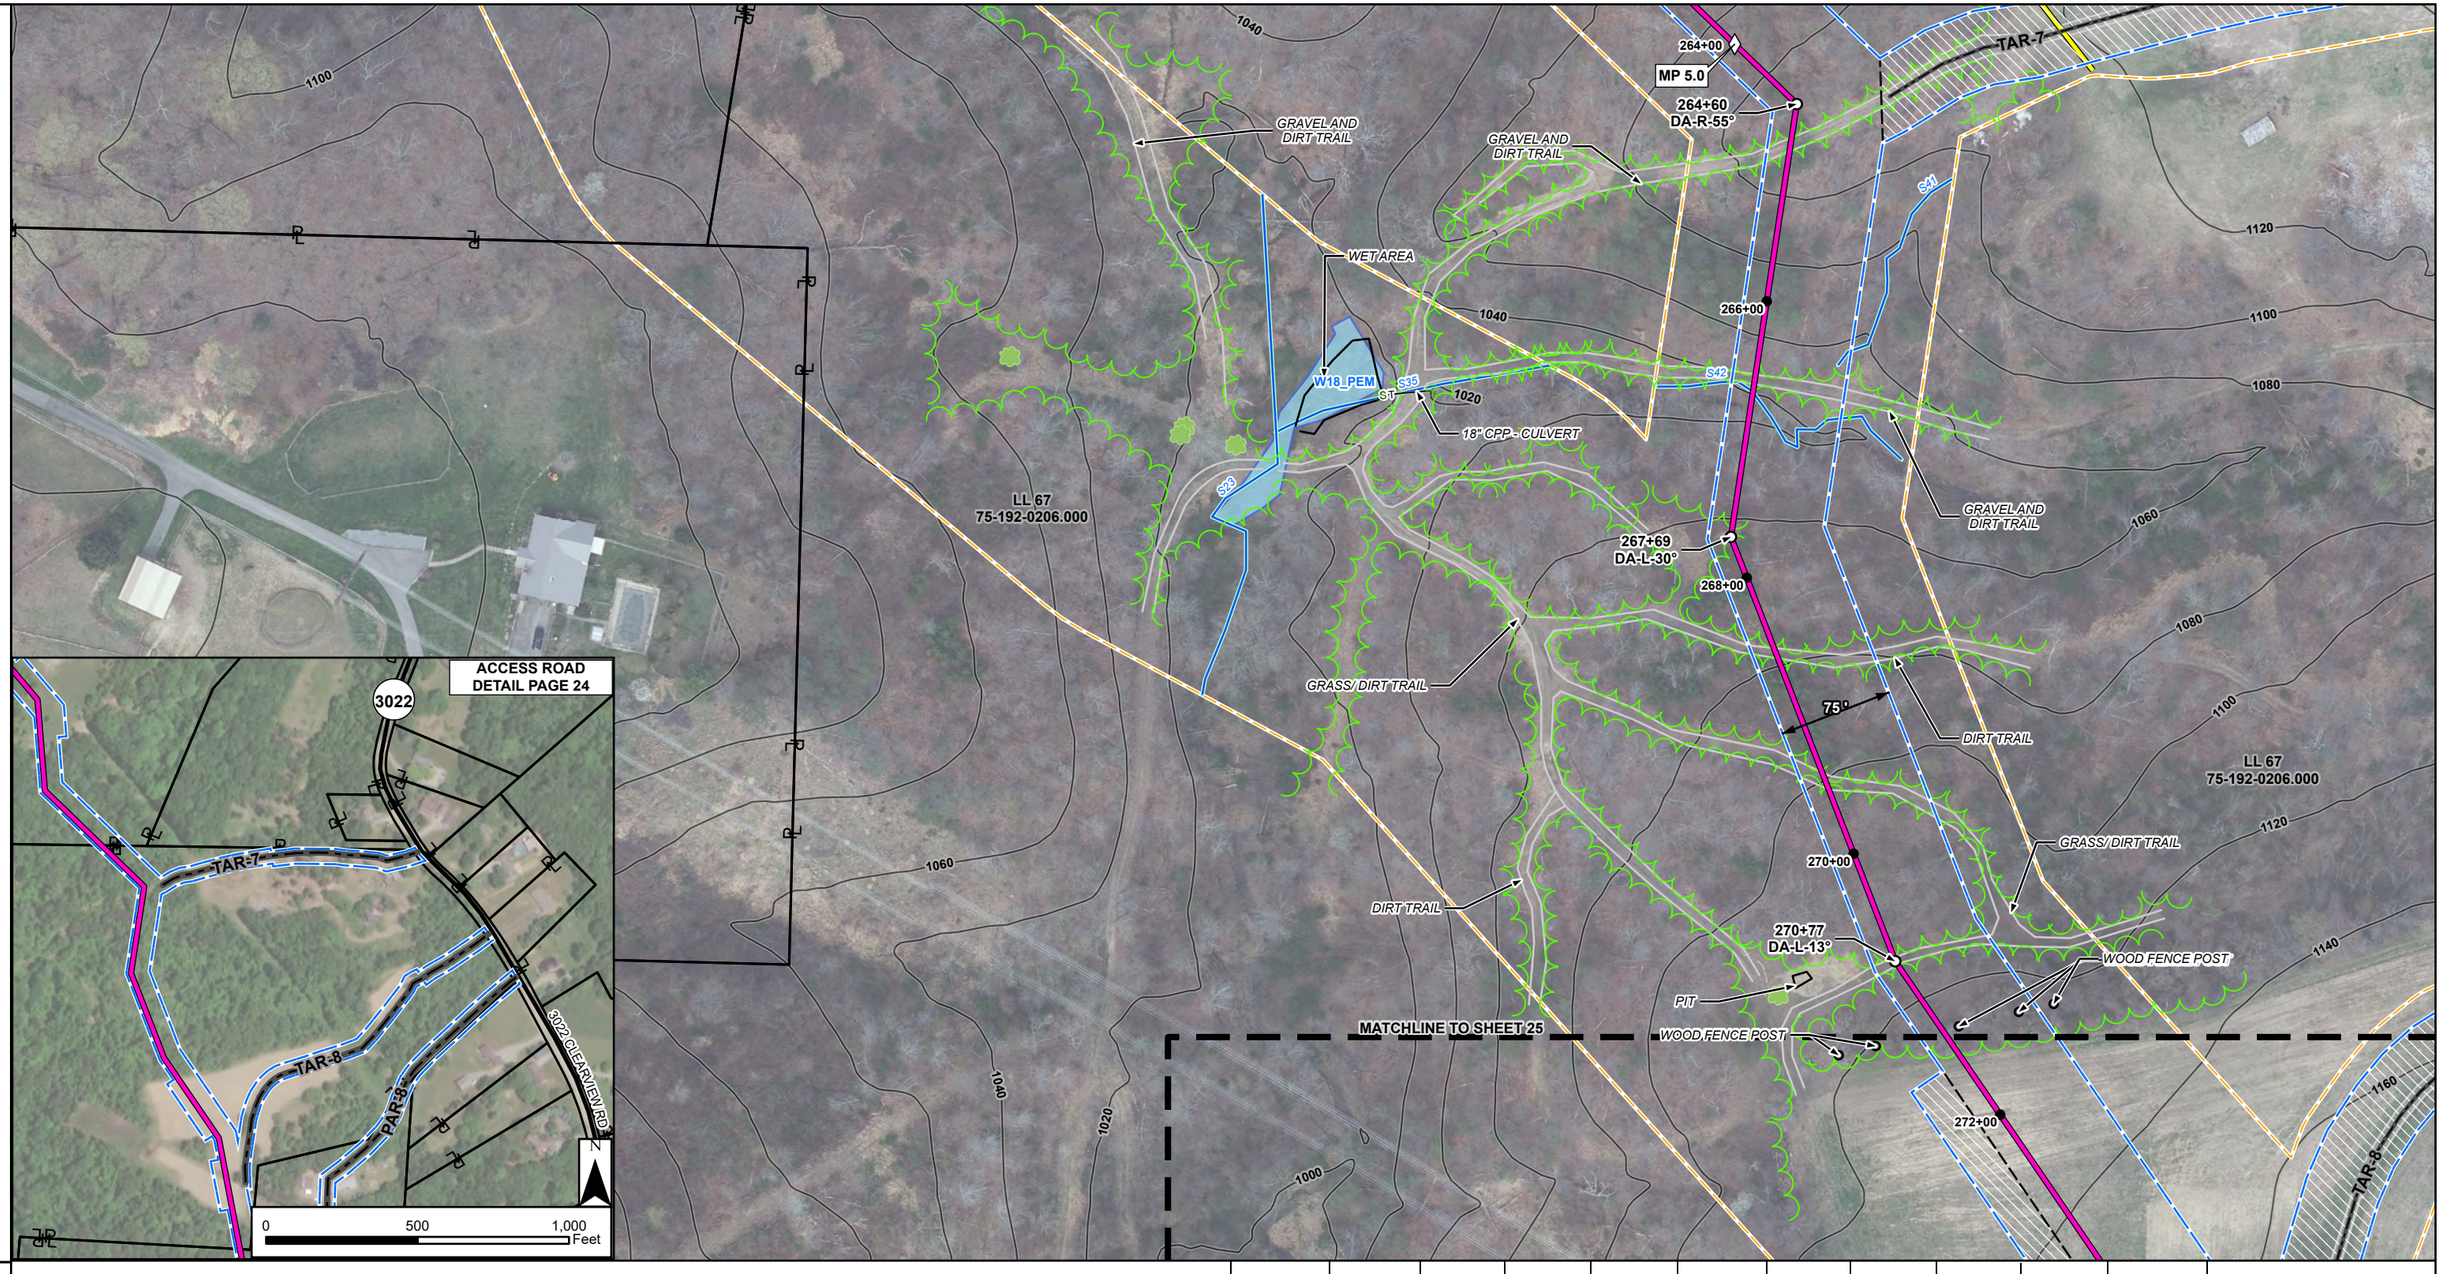

	263+58 MATCHLINE	264+79	264+99	266+45	266+65	268+45	268+65	269+38	269+58	270+67	270+87	271+38 MATCHLINE
FOOTAGE		121'	20'	146'	20'	180'	20'	73'	20'	109'	20'	51'	
WALL THICKNESS		24"-0.500WT	24"-0.562WT	24"-0.500WT	24"-0.562WT	24"-0.500WT	24"-0.562WT	24"-0.500WT	24"-0.562WT	24"-0.500WT	24"-0.562WT	24"-0.500WT	
GRADE		X-65	X-65	X-65	X-65	X-65	X-65	X-65	X-65	X-65	X-65	X-65	
COATING		FBE	PWR	FBE	PWR	FBE	PWR	FBE	PWR	FBE	PWR	FBE	

N
W E
S

ISSUED FOR FERC

National Fuel®
Supply Corporation

0 100 200 Feet

National Fuel Supply Corporation
Shippingport Lateral Project

Raccoon Township
Beaver County
Pennsylvania

REV	
P	

DRAWN BY :	KEYSTONE CONSULTANTS. LLC
CHECKED BY :	D. MCINTIRE
SCALE :	1 =100 feet
DATE :	8/21/2025

PIPELINE

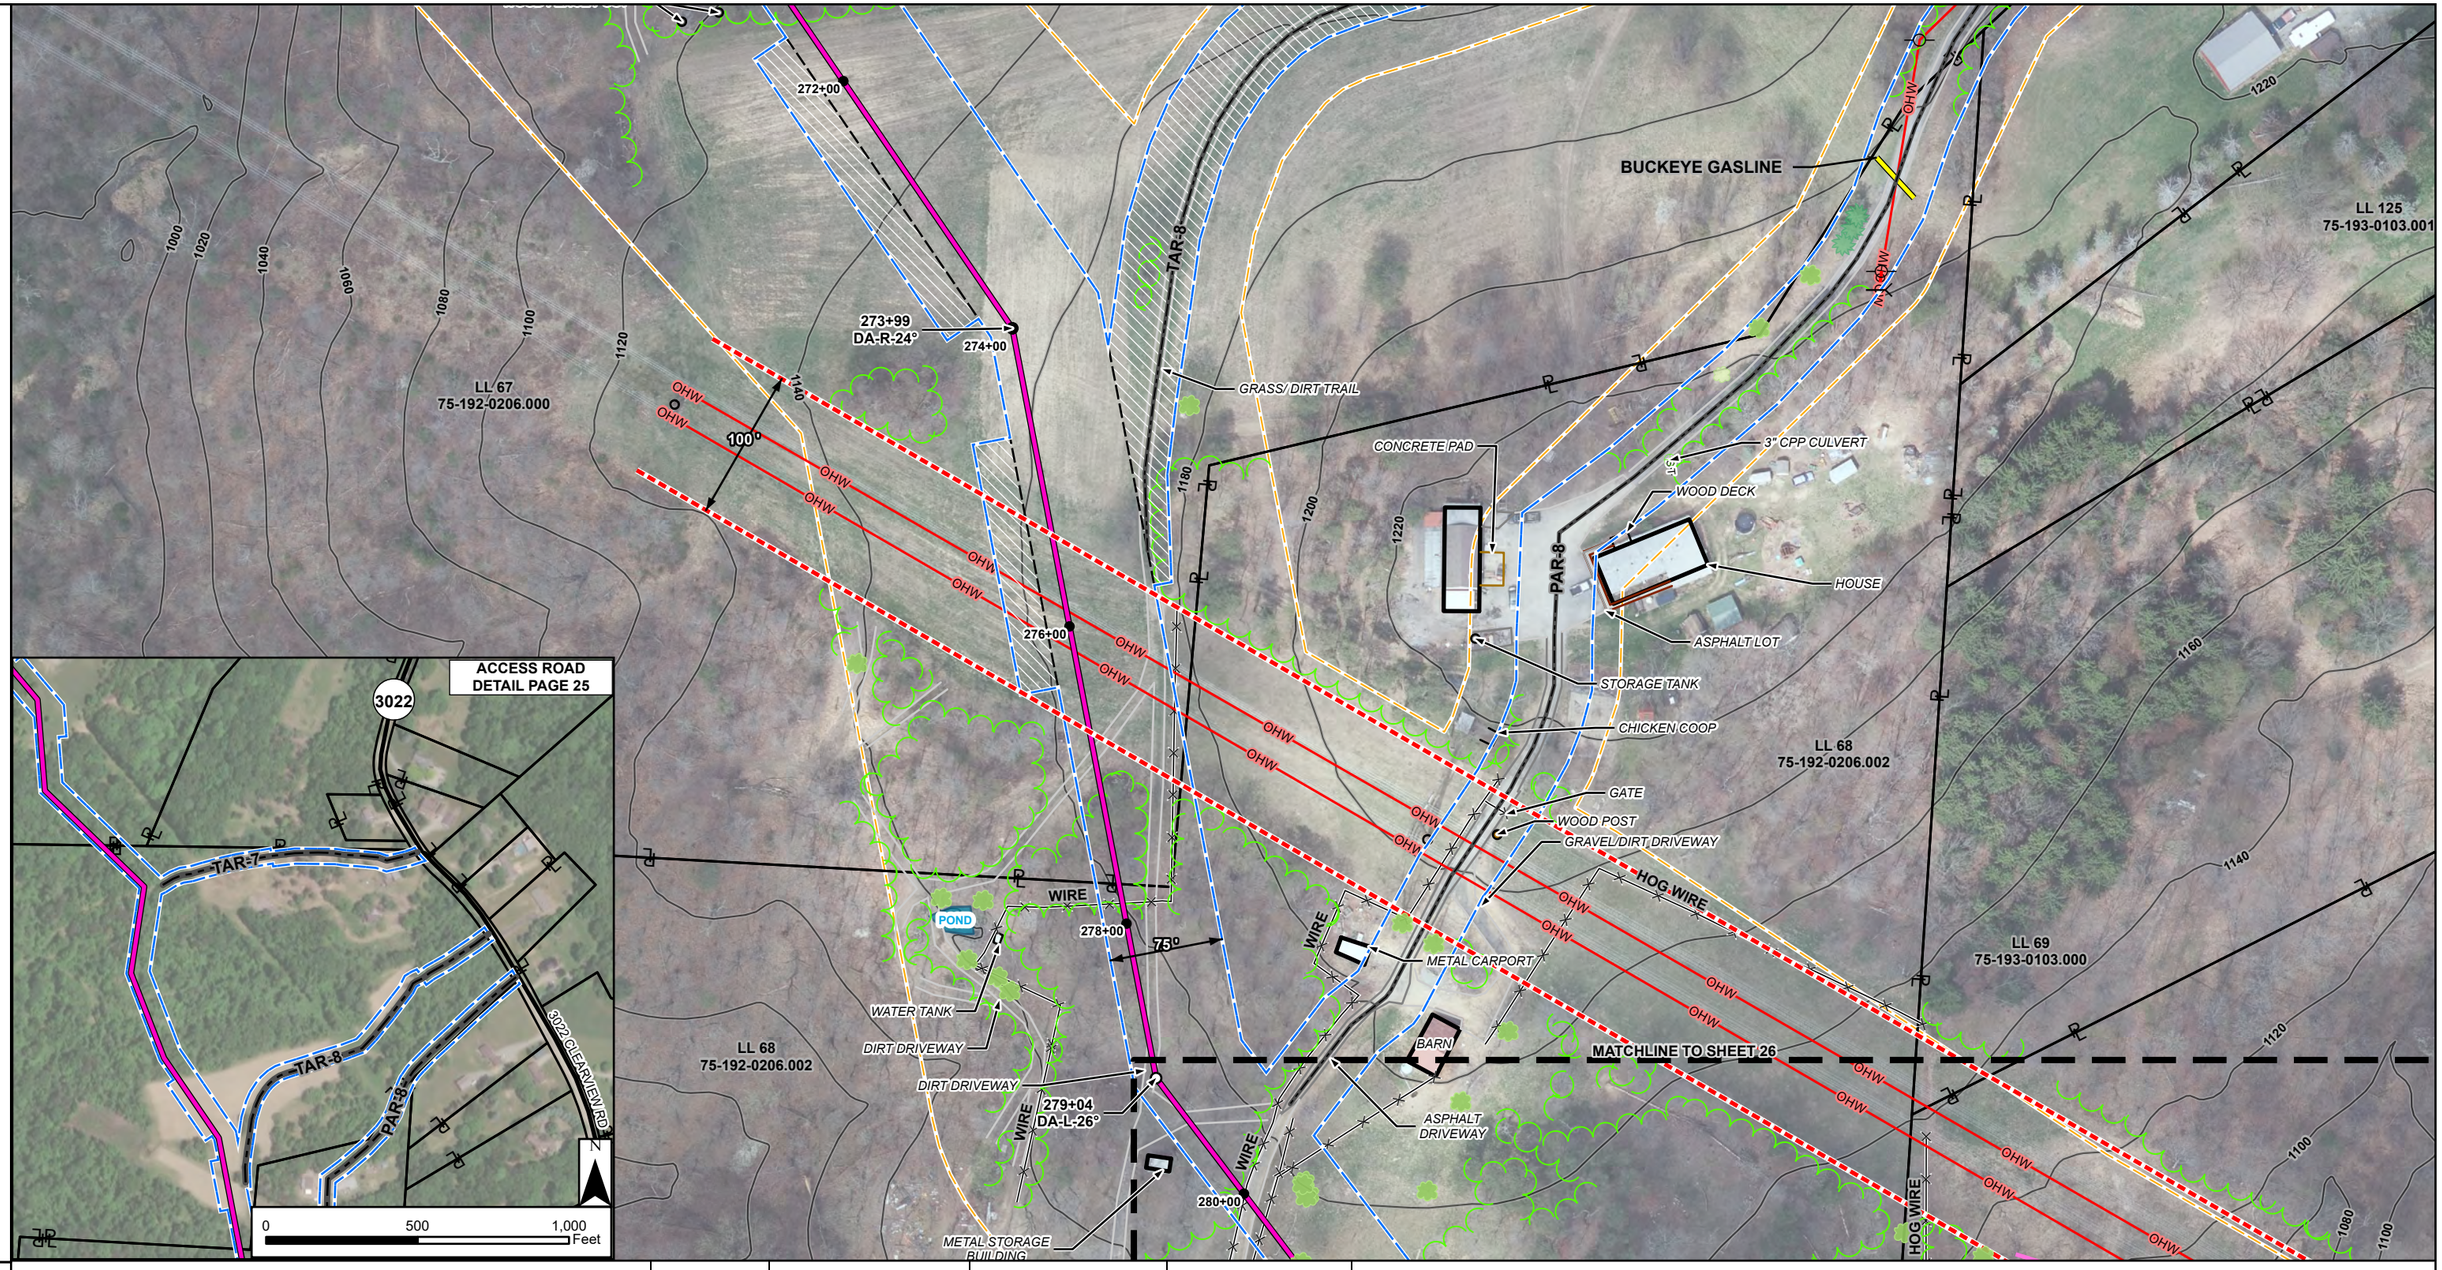

FOOTAGE		539'	20'	153'	42'	
WALL THICKNESS	271+38 MATCHLINE	24"-0.500WT	276+77	24"-0.562WT	276+97	24"-0.500WT	278+50	24"-0.562WT	278+92 MATCHLINE
GRADE		X-65		X-65		X-65		X-65	
COATING		FBE		PWR		FBE		PWR	

N W E S

ISSUED FOR FERC

National Fuel® Supply Corporation

0 100 200 Feet

National Fuel Supply Corporation
Shippingport Lateral Project

Raccoon Township
Beaver County
Pennsylvania

REV P

DRAWN BY : KEYSTONE CONSULTANTS. LLC
CHECKED BY : D. MCINTIRE
SCALE : 1 =100 feet
DATE : 8/21/2025

PIPELINE

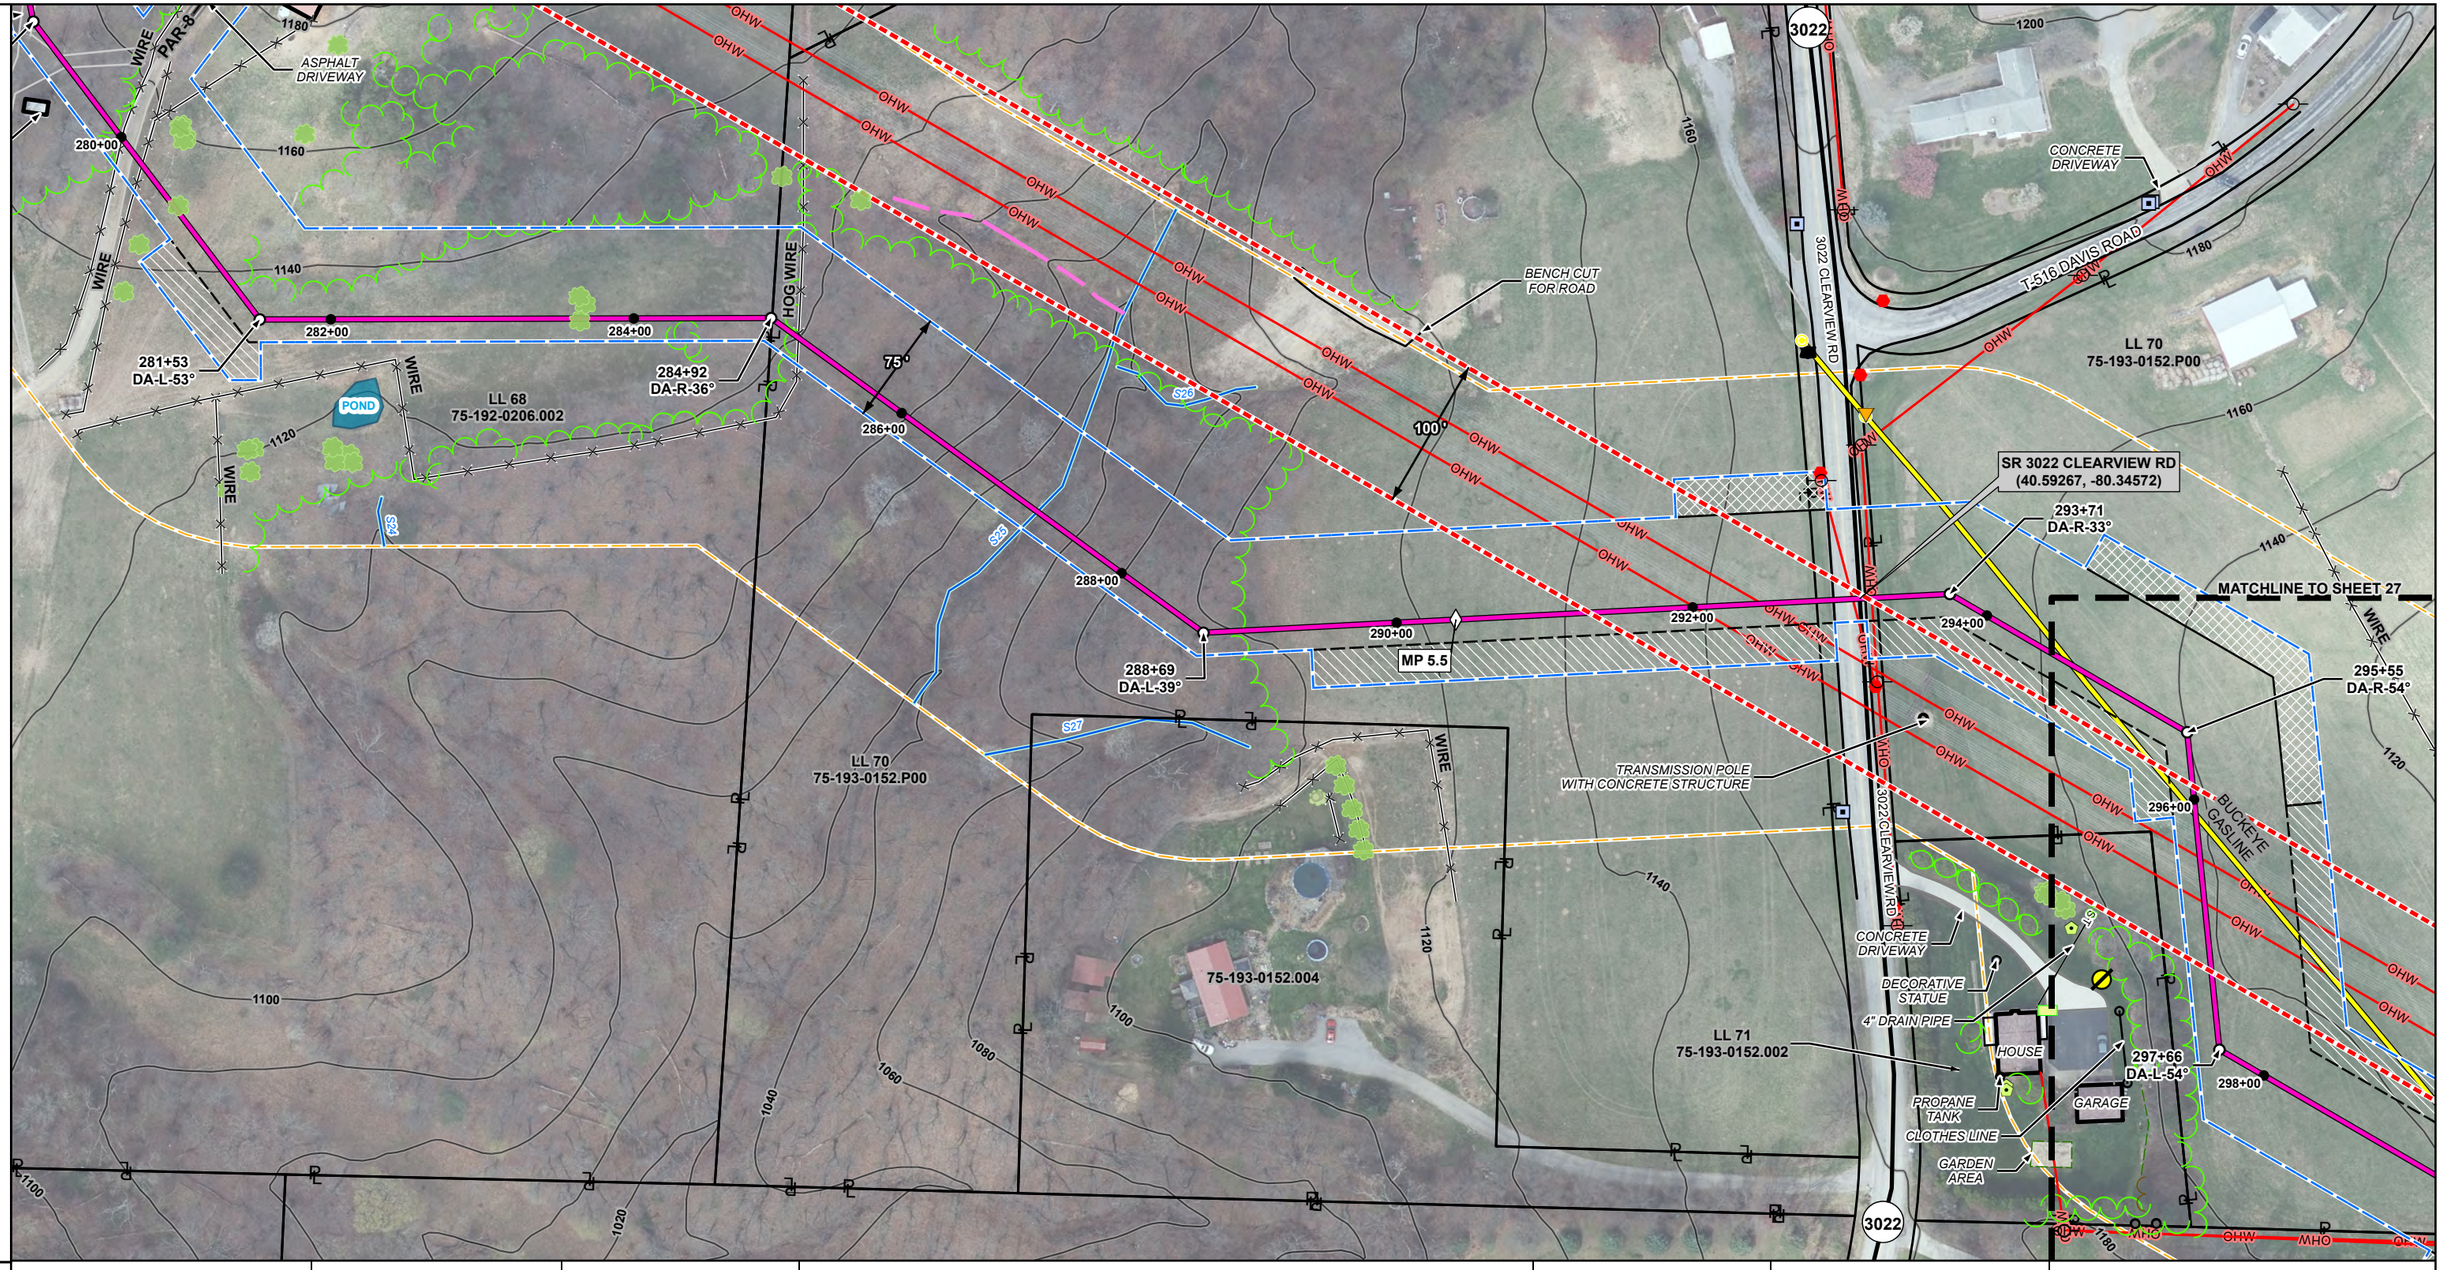

FOOTAGE	38'	68'	20'	1252'	70'	110'	
WALL THICKNESS	24"-0.562WT	24"-0.500WT	24"-0.562WT	24"-0.500WT	24"-0.562WT	24"-0.500WT	
GRADE	X-65	X-65	X-65	X-65	X-65	X-65	
COATING	PWR	FBE	PWR	FBE	PWR	FBE	
	278+92 MATCHLINE	279+30	279+98	280+18	292+70	293+40	294+50 MATCHLINE

N W E S

ISSUED FOR FERC

National Fuel® Supply Corporation

0 100 200 Feet

National Fuel Supply Corporation
Shippingport Lateral Project
Raccoon Township
Beaver County
Pennsylvania

REV P

DRAWN BY : KEYSTONE CONSULTANTS. LLC
CHECKED BY : D. MCINTIRE
SCALE : 1 =100 feet
DATE : 8/21/2025

26 / 34

PIPELINE

295+55
DA-R-54°

296+00

297+66
DA-L-54°

298+00

GARAGE

LL 70
75-193-0152.P00

TRANSMISSION POLE
WITH CONCRETE STRUCTURE

WIRE

100'

300+00

24" PLASTIC LID

WOODEN
BENCH

BRUSH PILE

302+00

75°

304+00

303+09
DA-L-50°

BUCKEYE GASLINE

LL 72
75-193-0102.006

WIRE

SAND
MOUND

TRANSMISSION POLE
WITH CONCRETE STRUCTURE

CLEANOUTS

LL 73
75-193-0102.005

LL 74
75-193-0159.P00

BARBED WIRE

305+29
DA-R-41°

306+00

308+16
DA-R-45°

308+00

100'

310+00

MATCHLINE TO SHEET 28

FOOTAGE	1567'
WALL THICKNESS	24"-0.500WT
GRADE	X-65
COATING	FBE

294+50 MATCHLINE

310+17 MATCHLINE

N
W E
S

ISSUED FOR FERC

National Fuel®
Supply Corporation

0 100 200 Feet

National Fuel Supply Corporation
Shippingport Lateral Project

Raccoon Township
Beaver County
Pennsylvania

REV
P

DRAWN BY : KEYSTONE CONSULTANTS. LLC
CHECKED BY : D. MCINTIRE
SCALE : 1 =100 feet
DATE : 8/21/2025

27
34

PIPELINE

LL 73
75-193-0102.005

WIRE

75'

100'

312+00

314+00

316+00

317+27
DA-L-35°

318+00

319+99
DA-L-43°

320+00

322+00

324+00

MP 6.0

FENCE POST

LL 74
75-193-0159.P00

BUCKEYE GASLINE

S37

S36

S19

W16_PEM

RACCOON TWP

INDEPENDENCE TWP

MATCHLINE TO SHEET 29

FOOTAGE	1433'	
WALL THICKNESS	24"-0.500WT	
GRADE	X-65	
COATING	FBE	

310+17 MATCHLINE

324+50 MATCHLINE

N W E S

ISSUED FOR FERC

National Fuel® Supply Corporation

0 100 200 Feet

National Fuel Supply Corporation
Shippingport Lateral Project
Raccoon & Independence Townships
Beaver County
Pennsylvania

REV
P

DRAWN BY : KEYSTONE CONSULTANTS. LLC
CHECKED BY : D. MCINTIRE
SCALE : 1 =100 feet
DATE : 8/21/2025

28
34

PIPELINE

RACCOON TWP
INDEPENDENCE TWP

LL 75
66-193-0164.P00

LL 121
66-193-0165.001

66-193-0165.002

LL 76
66-193-0163.001

326+90
DA-R-36°

326+00

328+00

330+00

330+97
DA-L-24°

332+00

333+98
DA-L-42°

334+00

335+59
DA-R-62°

336+00

338+00

340+00

100°

75°

DEER STAND

DEER STAND

DEER STAND

GRASS PATH

WET AREA

W17_PEM

S34

OHW

WIRE

METAL

PAR-9

TAR-9

TRANSMISSION POLE

4" PVC VERTICAL PIPE WITH CAP

T-516 DAVIS ROAD
(40.58888, -80.33308)

T-516 DAVIS ROAD

ENERGY TRANSFER

SUNOCO LOGISTICS LINE

MATCHLINE TO SHEET 30

FOOTAGE	1346'	40'	236'
WALL THICKNESS	24"-0.500WT	24"-0.562WT	24"-0.500WT
GRADE	X-65	X-65	X-65
COATING	FBE	PWR	FBE

324+50 MATCHLINE

337+96

338+36

340+72 MATCHLINE

N
W E
S

ISSUED FOR FERC

National Fuel®
Supply Corporation

0 100 200 Feet

National Fuel Supply Corporation
Shippingport Lateral Project

Independence Township
Beaver County
Pennsylvania

REV
P

DRAWN BY : KEYSTONE CONSULTANTS. LLC
CHECKED BY : D. MCINTIRE
SCALE : 1 =100 feet
DATE : 8/21/2025

29
34

PIPELINE

FOOTAGE	8'	60'	966'		30'	335'	
WALL THICKNESS	24"-0.500WT	24"-0.562WT	24"-0.500WT		24"-0.562WT	24"-0.500WT	
GRADE	X-65	X-65	X-65		X-65	X-65	
COATING	FBE	PWR	FBE		PWR	FBE	

340+72 MATCHLINE | 340+80 | 341+40 | 351+06 | 351+36 | 354+71 MATCHLINE

ISSUED FOR FERC

National Fuel® Supply Corporation

0 100 200 Feet

National Fuel Supply Corporation
Shippingport Lateral Project
Independence Township
Beaver County
Pennsylvania

REV P

DRAWN BY : KEYSTONE CONSULTANTS. LLC
CHECKED BY : D. MCINTIRE
SCALE : 1 =100 feet
DATE : 8/21/2025

30 / 34

PIPELINE

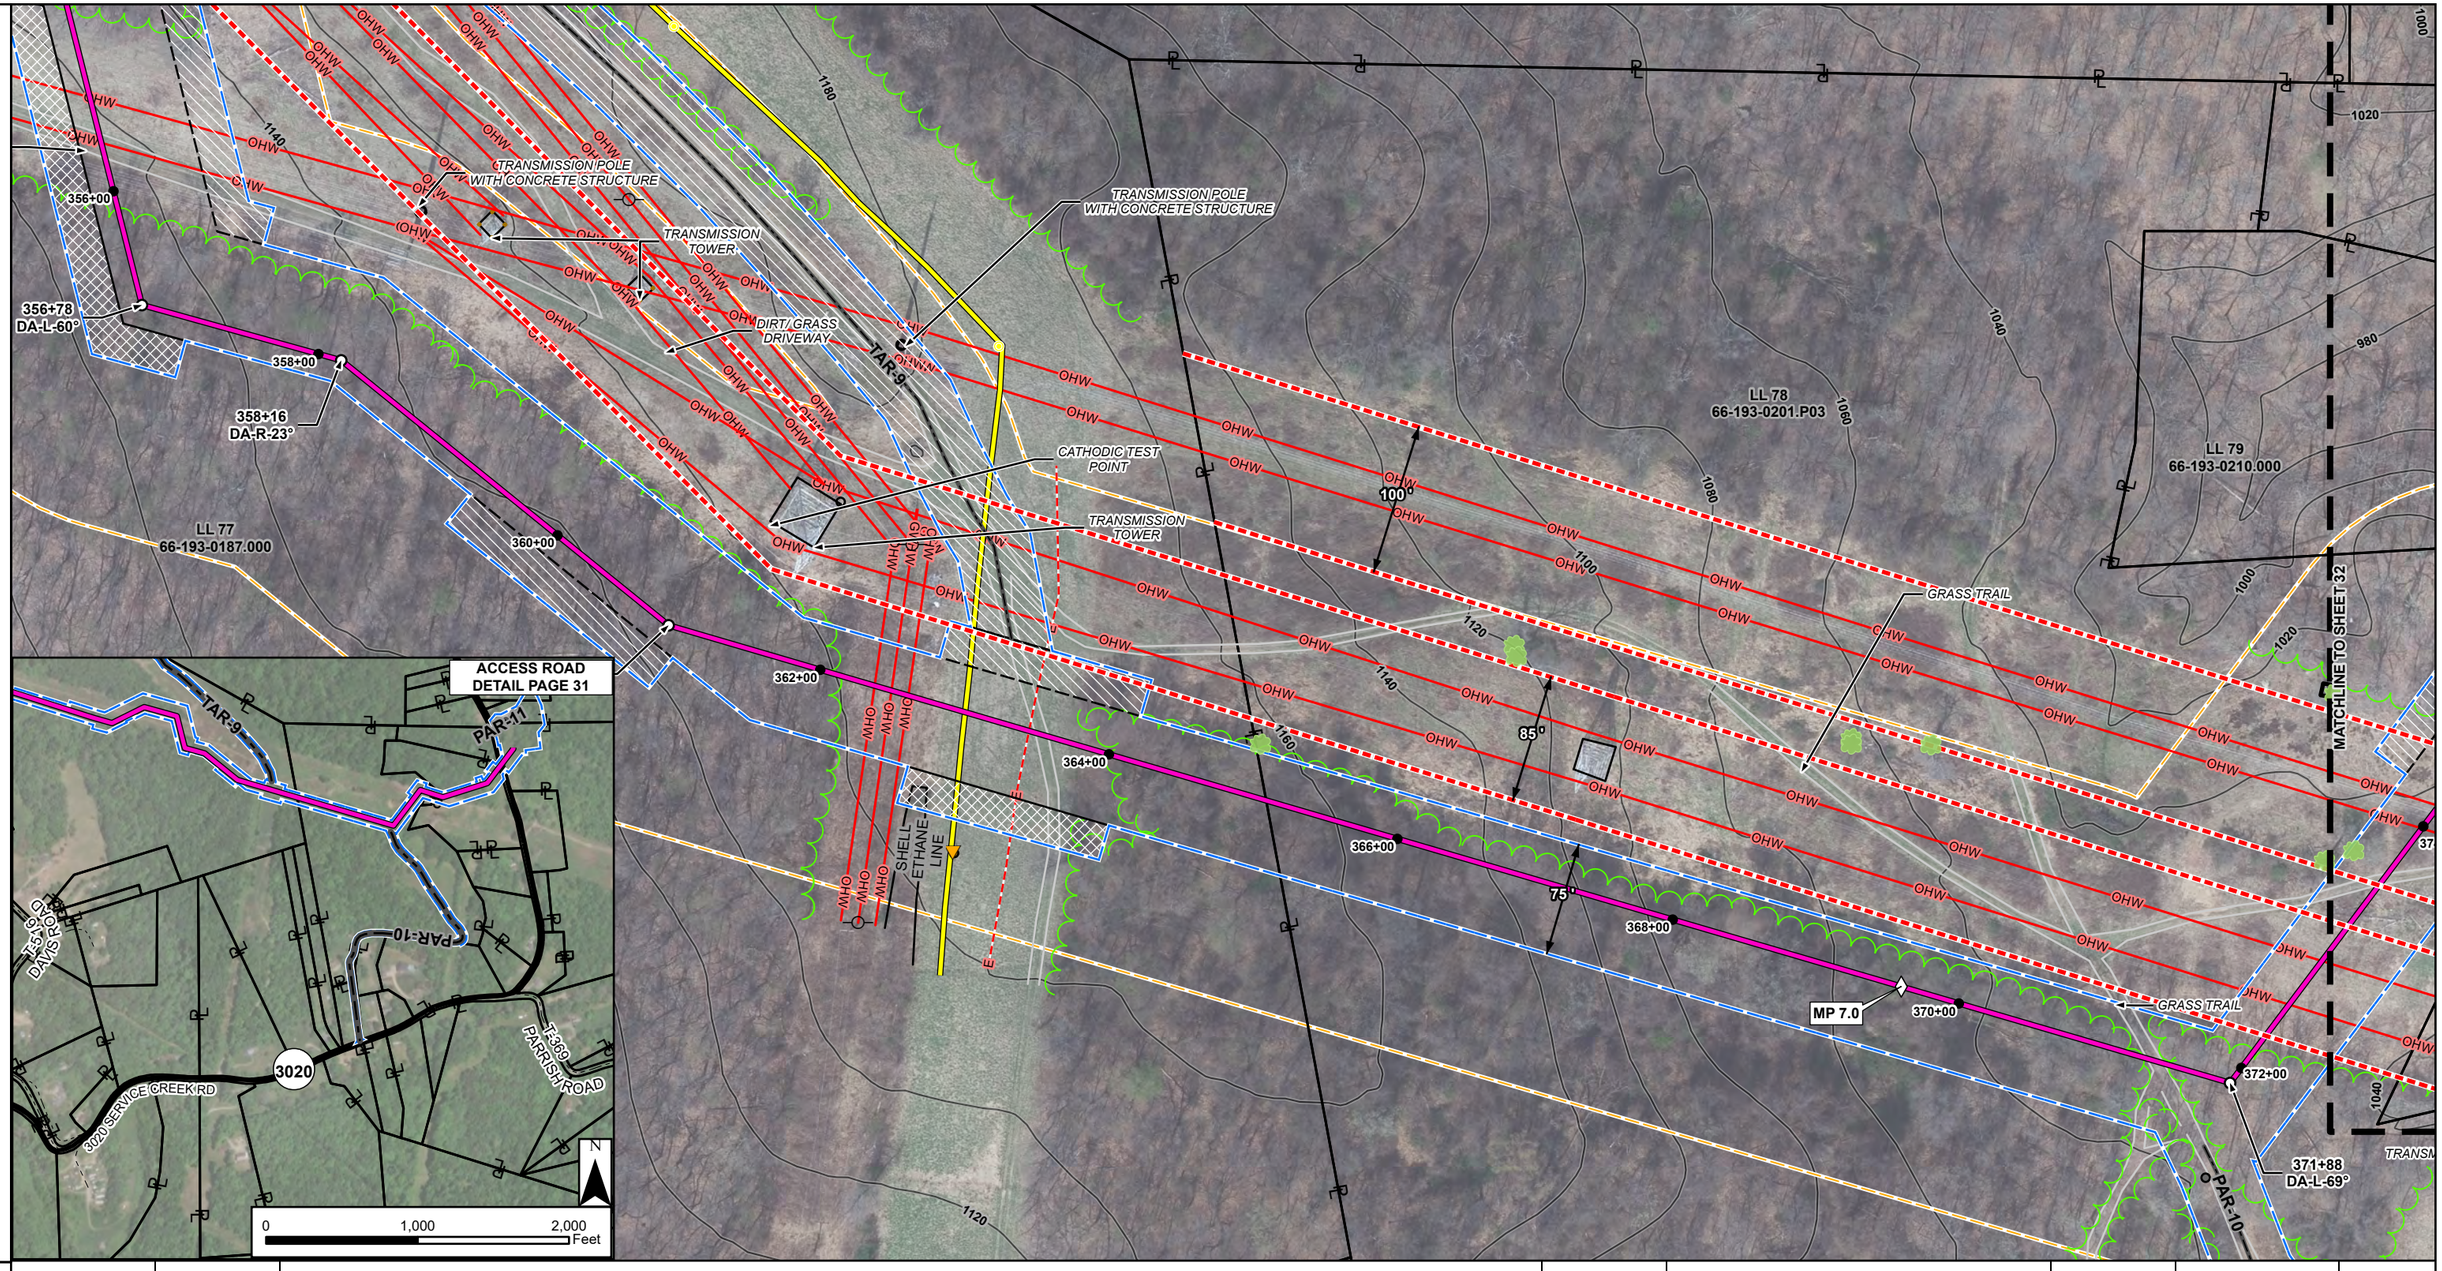

FOOTAGE	78'	40'	755'		20'	757'		30'	146'		
WALL THICKNESS	354+71 MATCHLINE	24"-0.500WT	355+49	24"-0.562WT	355+89	24"-0.500WT	363+44	24"-0.562WT	363+64	24"-0.500WT	371+21	24"-0.562WT	371+51	24"-0.500WT	372+97 MATCHLINE
GRADE	X-65		X-65		X-65		X-65		X-65		X-65		X-65		
COATING	FBE		PWR		FBE		PWR		FBE		PWR		FBE		

N
W E
S

ISSUED FOR FERC

National Fuel®
Supply Corporation

0 100 200 Feet

National Fuel Supply Corporation
Shippingport Lateral Project
Independence Township
Beaver County
Pennsylvania

REV	P
DRAWN BY :	KEYSTONE CONSULTANTS. LLC
CHECKED BY :	D. MCINTIRE
SCALE :	1 =100 feet
DATE :	8/21/2025

PIPELINE

LL 81
66-193-0184.000

LL 80
66-193-0210.001

LL 79
66-193-0210.000

LL 84
66-193-0210.003

LL 85
66-193-0210.002

CULVERT 18" CMP

EXISTING VALVE SET

CHAIN LINK

WIRE

PANEL BOX

METAL POST

GUIDERAIL

PAR-11

SR 3020 SERVICE CREEK RD
(40.58753, -80.31983)

3020 SERVICE CREEK RD

382+88
MP 7.25

382+81
DA-L-45°

382+00

380+00

379+87
DA-L-35°

376+43
DA-L-35°

374+82
DA-R-70°

376+00

374+00

378+00

75°

100°

85°

OLD EROSION CONTROL BLANKET

SHED

W01_PSS_02

W01_PEM_02

S31

S25

NFG

OHW

MLOHW

FOOTAGE	50'	20'	723'	130'	68'	
WALL THICKNESS	24"-0.500WT	24"-0.562WT	24"-0.500WT	24"-0.562WT	24"-0.500WT	
GRADE	X-65	X-65	X-65	X-65	X-65	
COATING	FBE	PWR	FBE	PWR	FBE	

372+97 MATCHLINE | 373+47 | 373+67 | 380+90 | 382+20 | 382+88 END PROPOSED PIPELINE

N W E S

ISSUED FOR FERC

National Fuel® Supply Corporation

0 100 200 Feet

National Fuel Supply Corporation
Shippingport Lateral Project
Independence Township
Beaver County
Pennsylvania

REV
P

DRAWN BY : KEYSTONE CONSULTANTS. LLC
CHECKED BY : D. MCINTIRE
SCALE : 1 =100 feet
DATE : 8/21/2025

32
34

PIPELINE

FOOTAGE	
WALL THICKNESS	
GRADE	
COATING	

N W E S

ISSUED FOR FERC

National Fuel® Supply Corporation

0 100 200 Feet

National Fuel Supply Corporation
Shippingport Lateral Project

Raccoon Township
Beaver County
Pennsylvania

REV	DRAWN BY :	KEYSTONE CONSULTANTS. LLC
	CHECKED BY :	D. MCINTIRE
P	SCALE :	1 =100 feet
	DATE :	8/21/2025

33
34

PIPELINE

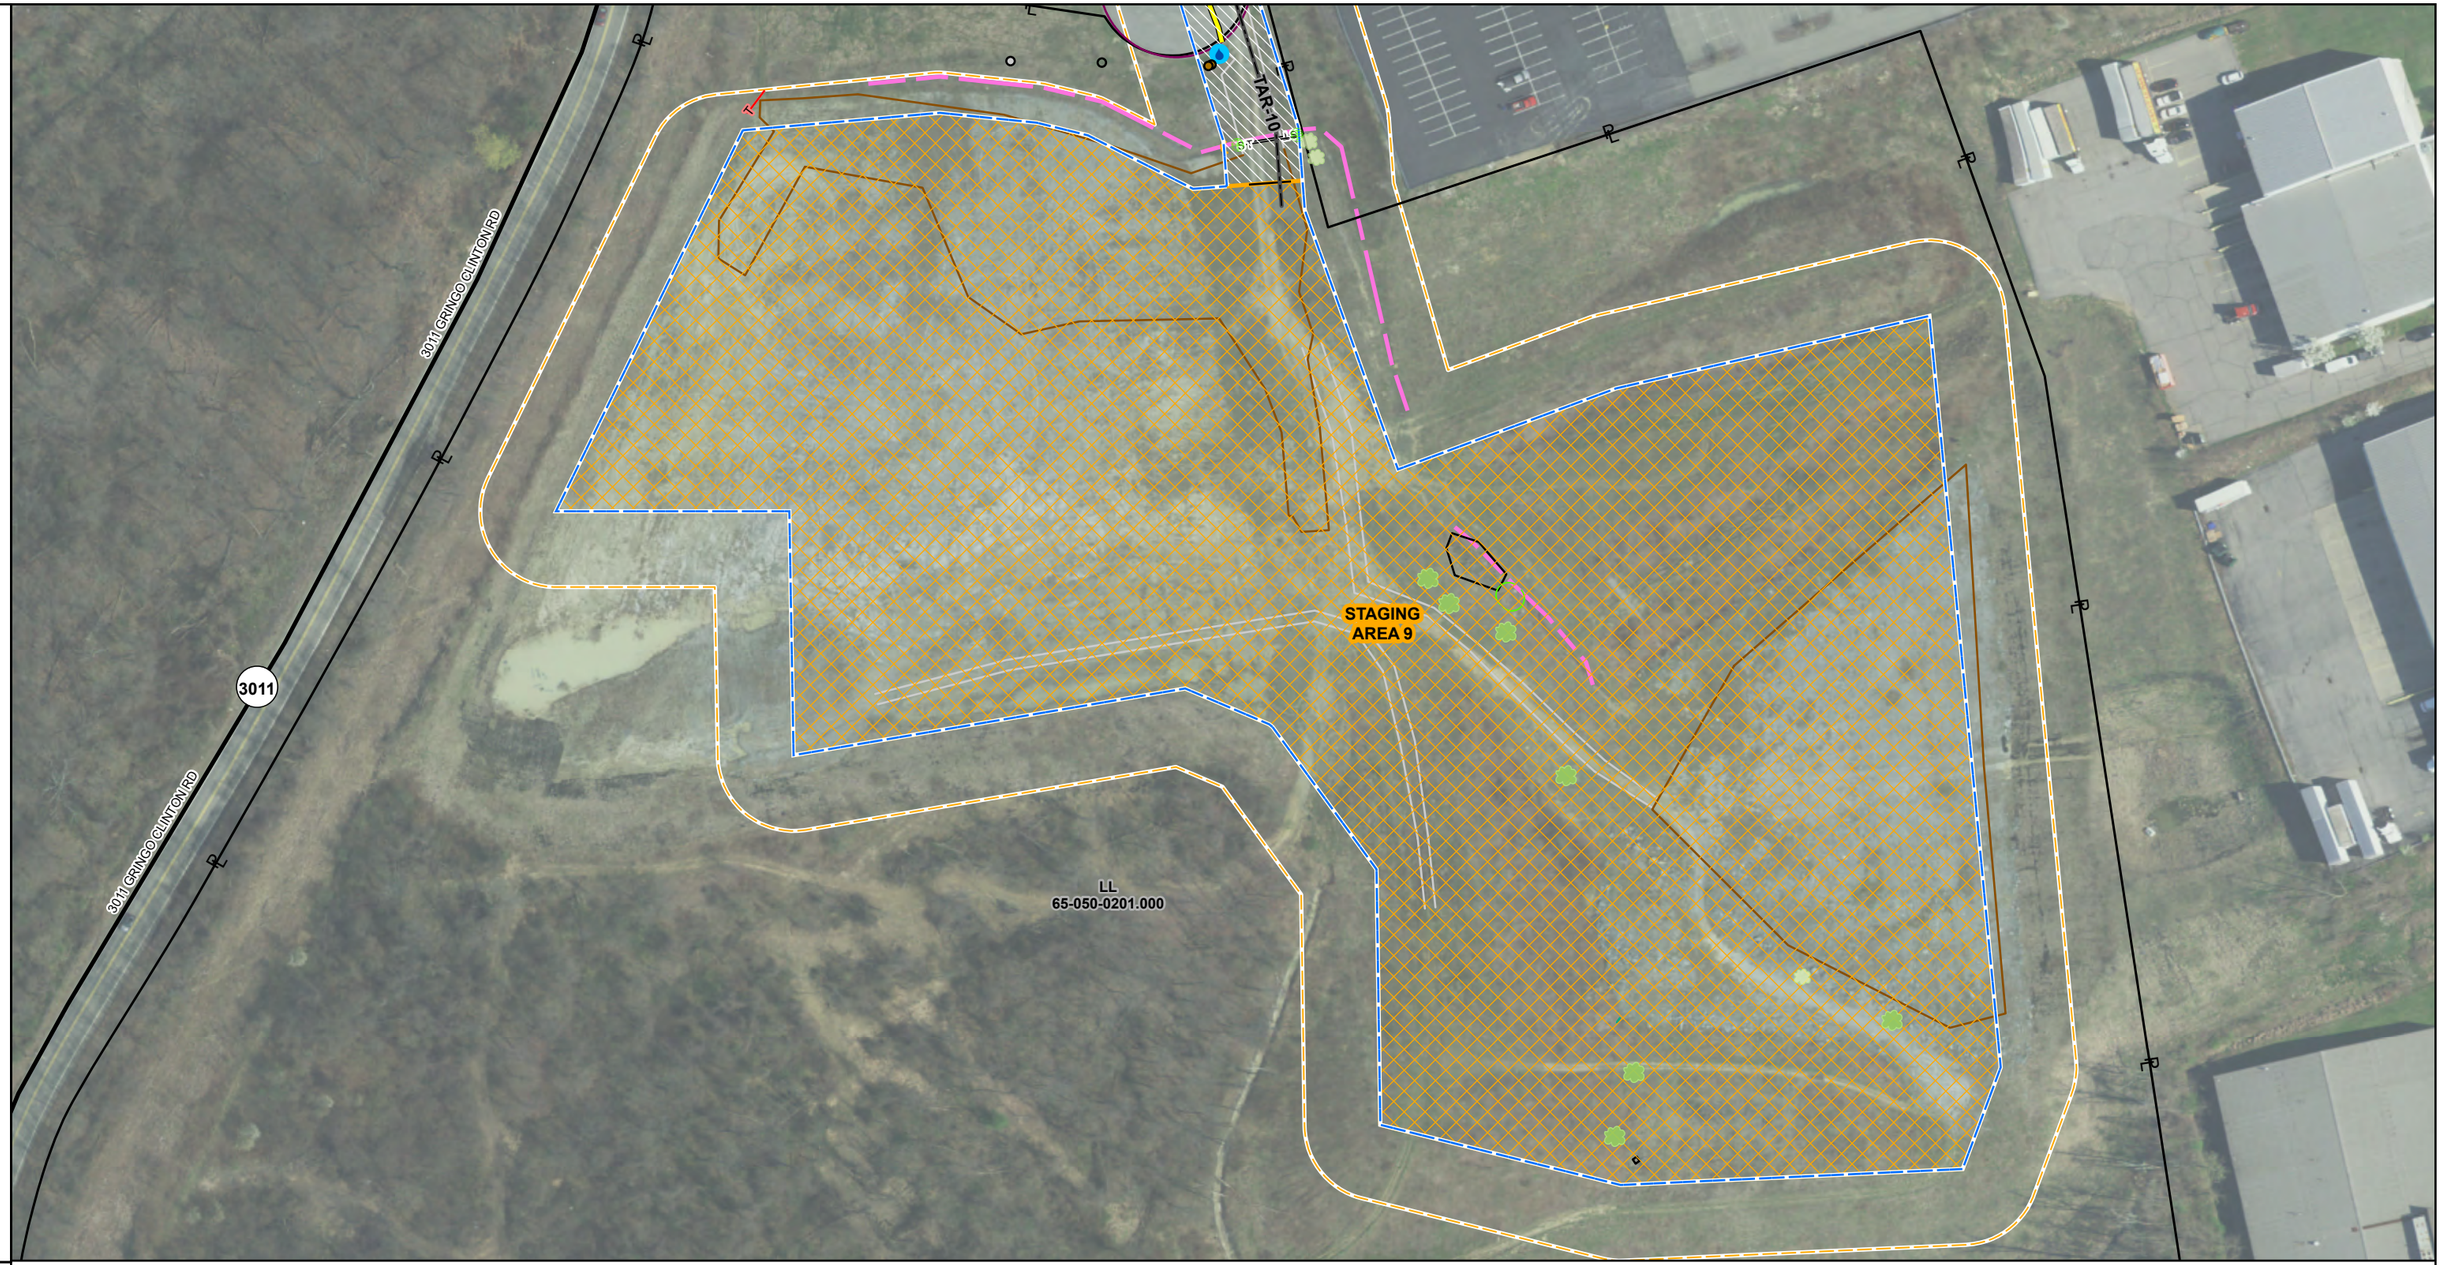

FOOTAGE	
WALL THICKNESS	
GRADE	
COATING	

N
W E
S

ISSUED FOR FERC

National Fuel®
Supply Corporation

0 100 200 Feet

National Fuel Supply Corporation
Shippingport Lateral Project

Hopewell Township
Beaver County
Pennsylvania

REV
P

DRAWN BY : KEYSTONE CONSULTANTS. LLC
CHECKED BY : D. MCINTIRE
SCALE : 1 =100 feet
DATE : 8/21/2025

34
34

Appendix A-4 – Mercer Compressor Station Plan Drawing

Study Area

Limit of Disturbance

0 20 40 Meters

0 80 160 Feet

Scale: 1:2,000

Spatial Reference: NAD 1983 2011 StatePlane Pennsylvania South FIPS 3702 Ft US

Basemap: ESRI World Imagery (5/2/2021)

Shippingport Lateral Project, Mercer Compressor Station

Mercer County, Pennsylvania

Prepared For: National Fuel Supply Corporation

Prepared By: TETRA TECH

Cartographer: JULIE.GIBSON

NOT FOR CONSTRUCTION

Date: 8/27/2025

Path: C:\Users\julie.gibson\Tetra Tech, Inc\My Data Sciences - My PCP\212C-BF-00598 NFG Line N13 Client Deliverables\ARR_Client_Delivery.aprx

Appendix A-5 – Construction ROW Workspace Configuration Figures

ROW Construction Configuration Drawings
Shippingport Lateral Pipeline

Station	Figure #
0+00 to 5+00	1
5+00 to 6+50	2
6+50 to 23+75	1
23+75 to 32+50	2
32+50 to 34+00	3
34+00 to 54+50	1
54+50 to 61+50	4
61+50 to 71+50	2
71+50 to 73+00	1
73+00 to 73+50	2
73+50 to 75+50	4
75+50 to 76+00	2
76+00 to 81+75	1
81+75 to 93+00	2
93+00 to 96+50	1
96+50 to 99+80	4
99+80 to 100+25	1
100+25 to 103+20	2
103+20 to 104+00	1
104+00 to 109+00	5
109+00 to 110+50	6
110+50 to 113+00	2
113+00 to 114+00	1
114+00 to 117+50	2
117+50 to 119+75	1
119+75 to 126+50	2
126+50 to 128+50	1
128+50 to 138+50	2
138+50 to 149+75	1
149+75 to 151+25	2
151+25 to 152+50	5
152+50 to 153+00	6
153+00 to 157+00	1
157+00 to 160+30	7
160+30 to 160+75	1
160+75 to 163+75	2
163+75 to 167+75	1
167+75 to 181+00	2
181+00 to 185+25	1
185+25 to 192+00	6
192+00 to 196+25	1

Station	Figure #
196+25 to 202+50	5
202+50 to 203+50	1
203+50 to 205+00	6
205+00 to 212+00	5
212+00 to 213+00	5
213+00 to 216+00	1
216+00 to 217+50	6
217+50 to 218+75	5
218+75 to 219+50	6
219+50 to 220+25	5
220+25 to 221+75	1
221+75 to 223+00	5
223+00 to 224+00	6
224+00 to 228+80	2
228+80 to 229+75	1
229+75 to 230+25	5
230+25 to 231+40	1
231+40 to 233+75	2
233+75 to 234+00	1
234+00 to 235+00	5
235+00 to 235+20	1
235+20 to 239+50	5
239+50 to 243+75	1
243+75 to 247+75	5
247+75 to 248+75	1
248+75 to 251+50	5
251+50 to 252+40	2
252+40 to 253+00	4
253+00 to 253+60	2
253+60 to 255+30	1
255+30 to 258+00	2
258+00 to 271+50	1
271+50 to 274+00	5
274+00 to 274+50	1
274+50 to 276+25	5
276+25 to 280+75	1
280+75 to 281+50	5
281+50 to 289+50	1
289+50 to 292+00	5
292+00 to 293+00	6
293+00 to 293+20	1

ROW Construction Configuration Drawings
Shippingport Lateral Pipeline

Station	Figure #
293+20 to 294+50	5
294+50 to 296+00	6
296+00 to 299+50	2
299+50 to 300+00	4
300+00 to 304+50	2
304+50 to 307+25	1
307+25 to 308+50	2
308+50 to 313+50	5
313+50 to 314+80	1
314+80 to 316+75	6
316+75 to 317+25	5
317+25 to 319+00	6
319+00 to 325+75	1
325+75 to 326+50	5
326+50 to 327+25	1
327+25 to 329+00	2
329+00 to 331+00	4
331+00 to 334+50	2
334+50 to 335+75	1
335+75 to 336+75	2
336+75 to 337+75	4
337+75 to 338+00	5
338+00 to 338+30	1
338+30 to 340+25	5
340+25 to 342+00	6
342+00 to 347+00	1
347+00 to 349+00	2
349+00 to 351+00	4
351+00 to 351+50	7
351+50 to 357+50	2
357+50 to 359+40	1
359+40 to 361+00	5
361+00 to 362+80	1
362+80 to 364+00	4
364+00 to 374+25	1
374+25 to 375+25	2
375+25 to 376+50	1
376+50 to 379+00	5
379+00 to 379+50	6

Station	Figure #
379+50 to 380+50	5
380+50 to 381+00	6
381+00 to 381+25	2
381+25 to 381+40	1
381+40 to 382+88	5

SHIPPINGPORT LATERAL TYPICAL FIGURE #1

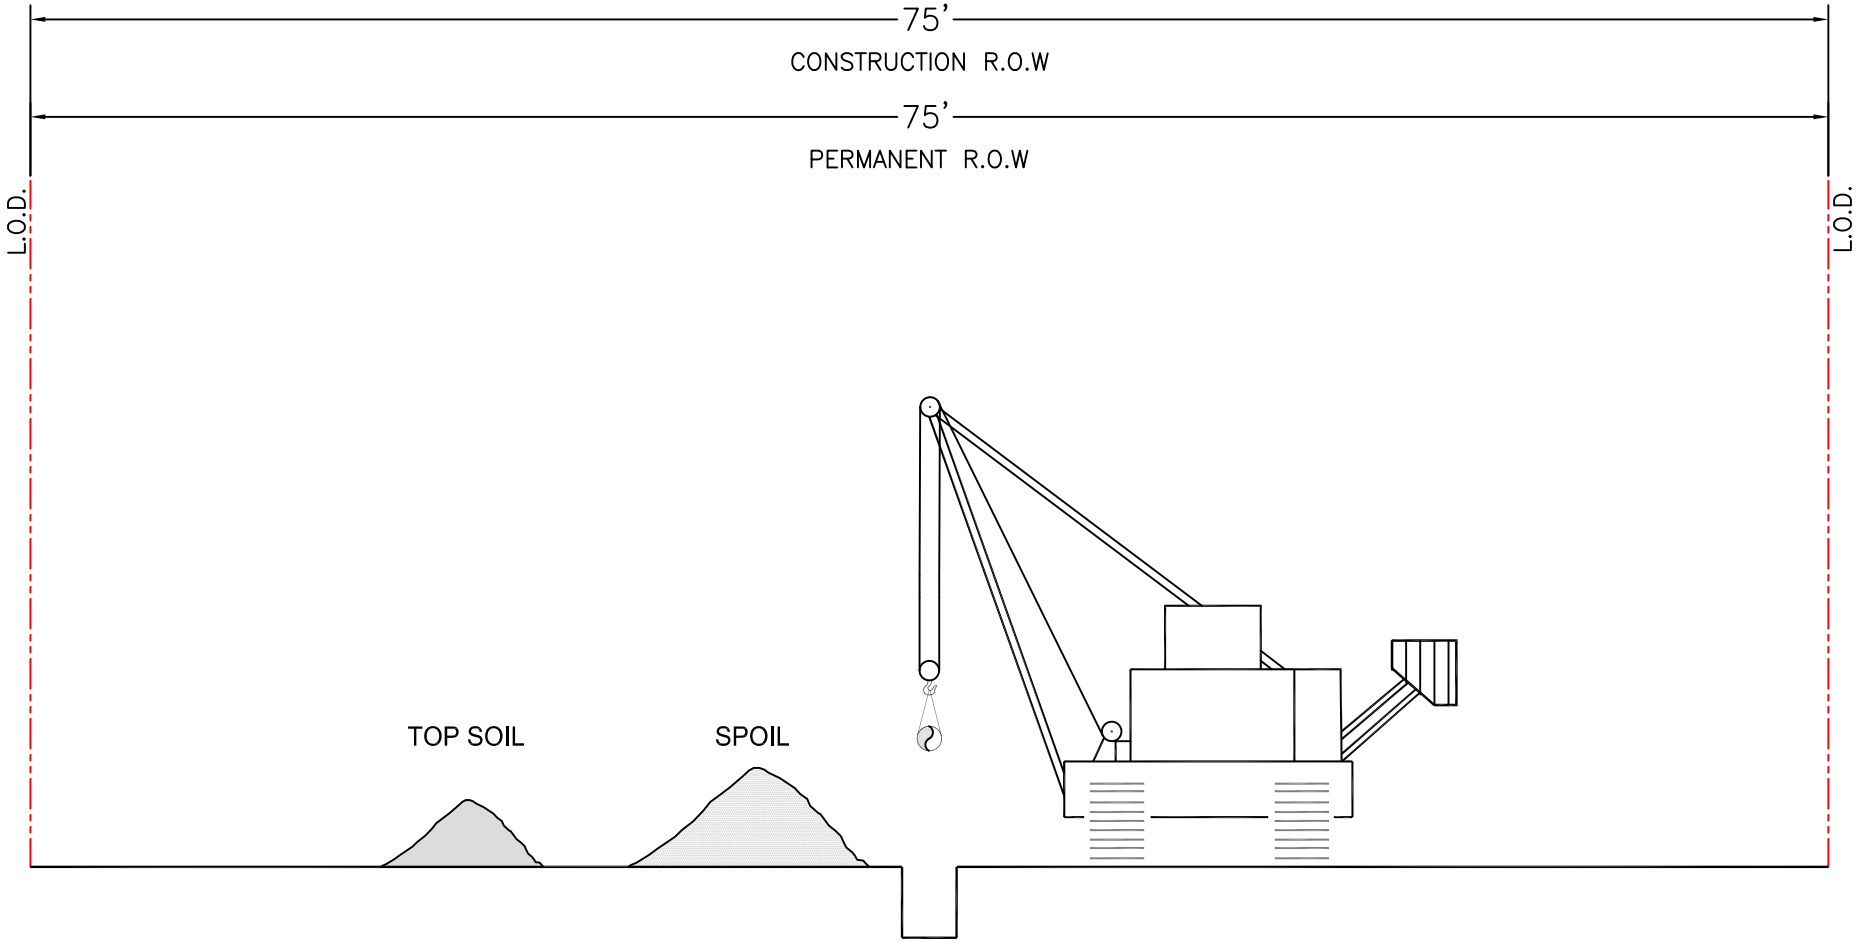

National Fuel® Supply Corporation

NATIONAL FUEL GAS SUPPLY CORPORATION
SHIPPINGPORT LATERAL CONSTRUCTION
RIGHT-OF-WAY TYPICAL DRAWING
FIGURE 1

F:\Eng-PA\Common\1 Expansion Projects - JJK\A - Line N Lateral Project\ROW Figures

SHIPPINGPORT LATERAL TYPICAL FIGURE #2

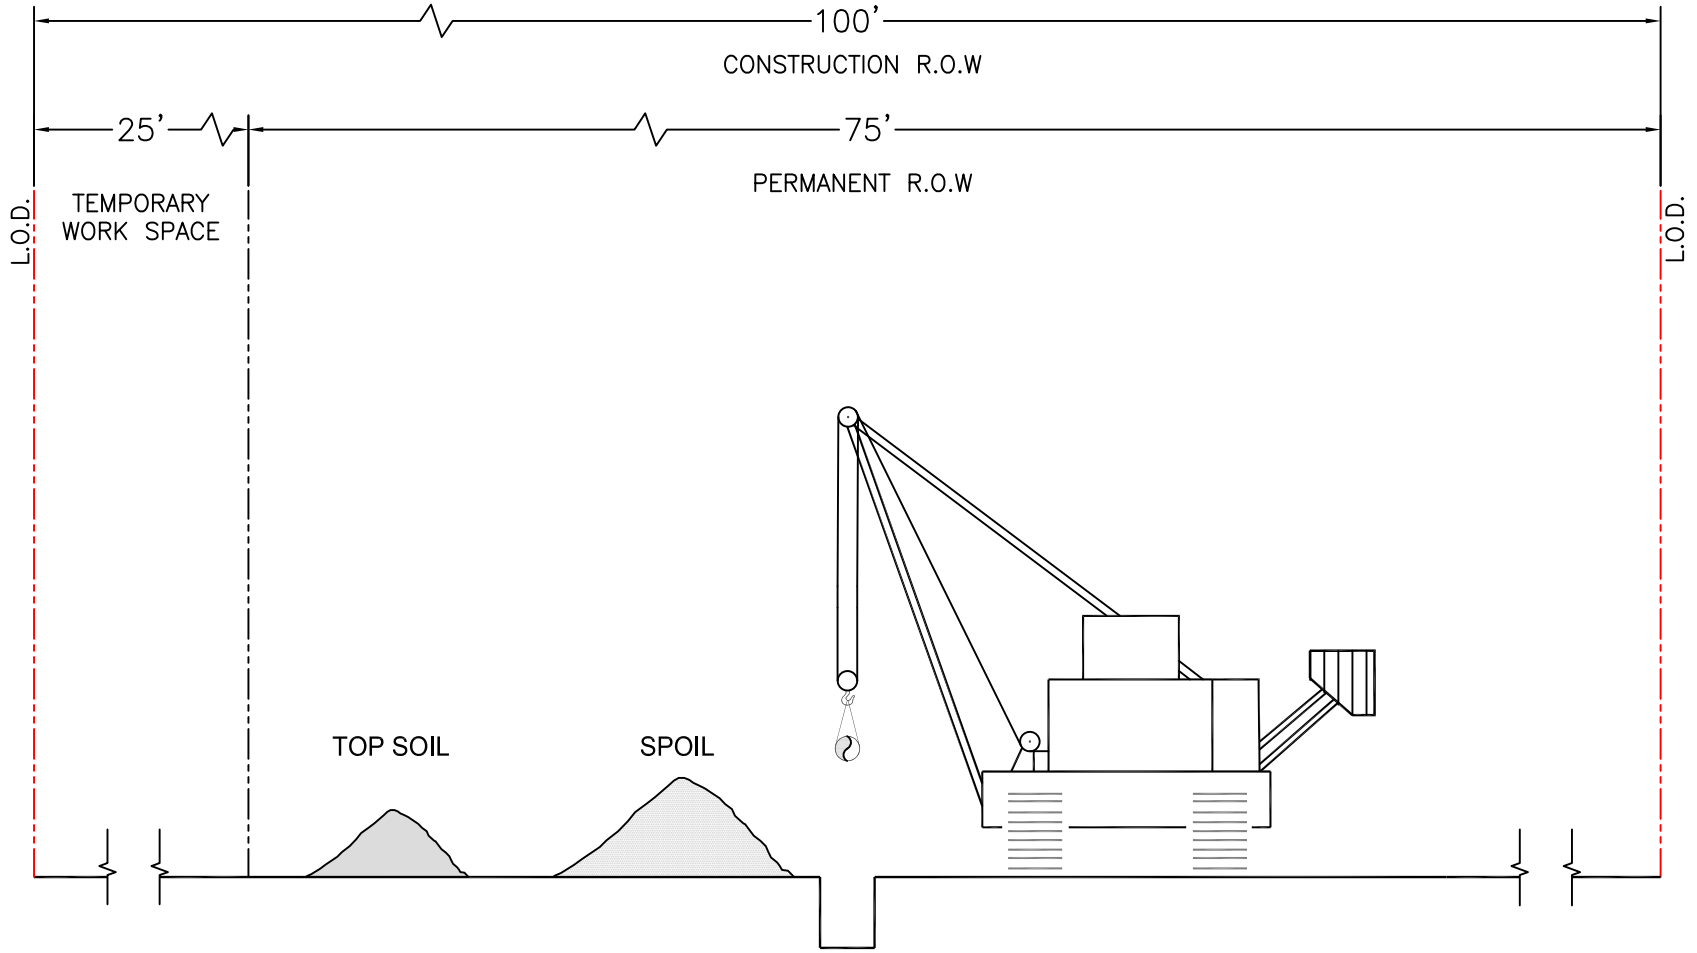

National Fuel®
Supply Corporation

NATIONAL FUEL GAS SUPPLY CORPORATION
SHIPPINGPORT LATERAL CONSTRUCTION
RIGHT-OF-WAY TYPICAL DRAWING
FIGURE 2

F:\Eng-PA\Common\1 Expansion Projects - JJK\A - Line N Lateral Project\ROW Figures

SHIPPINGPORT LATERAL TYPICAL FIGURE #3

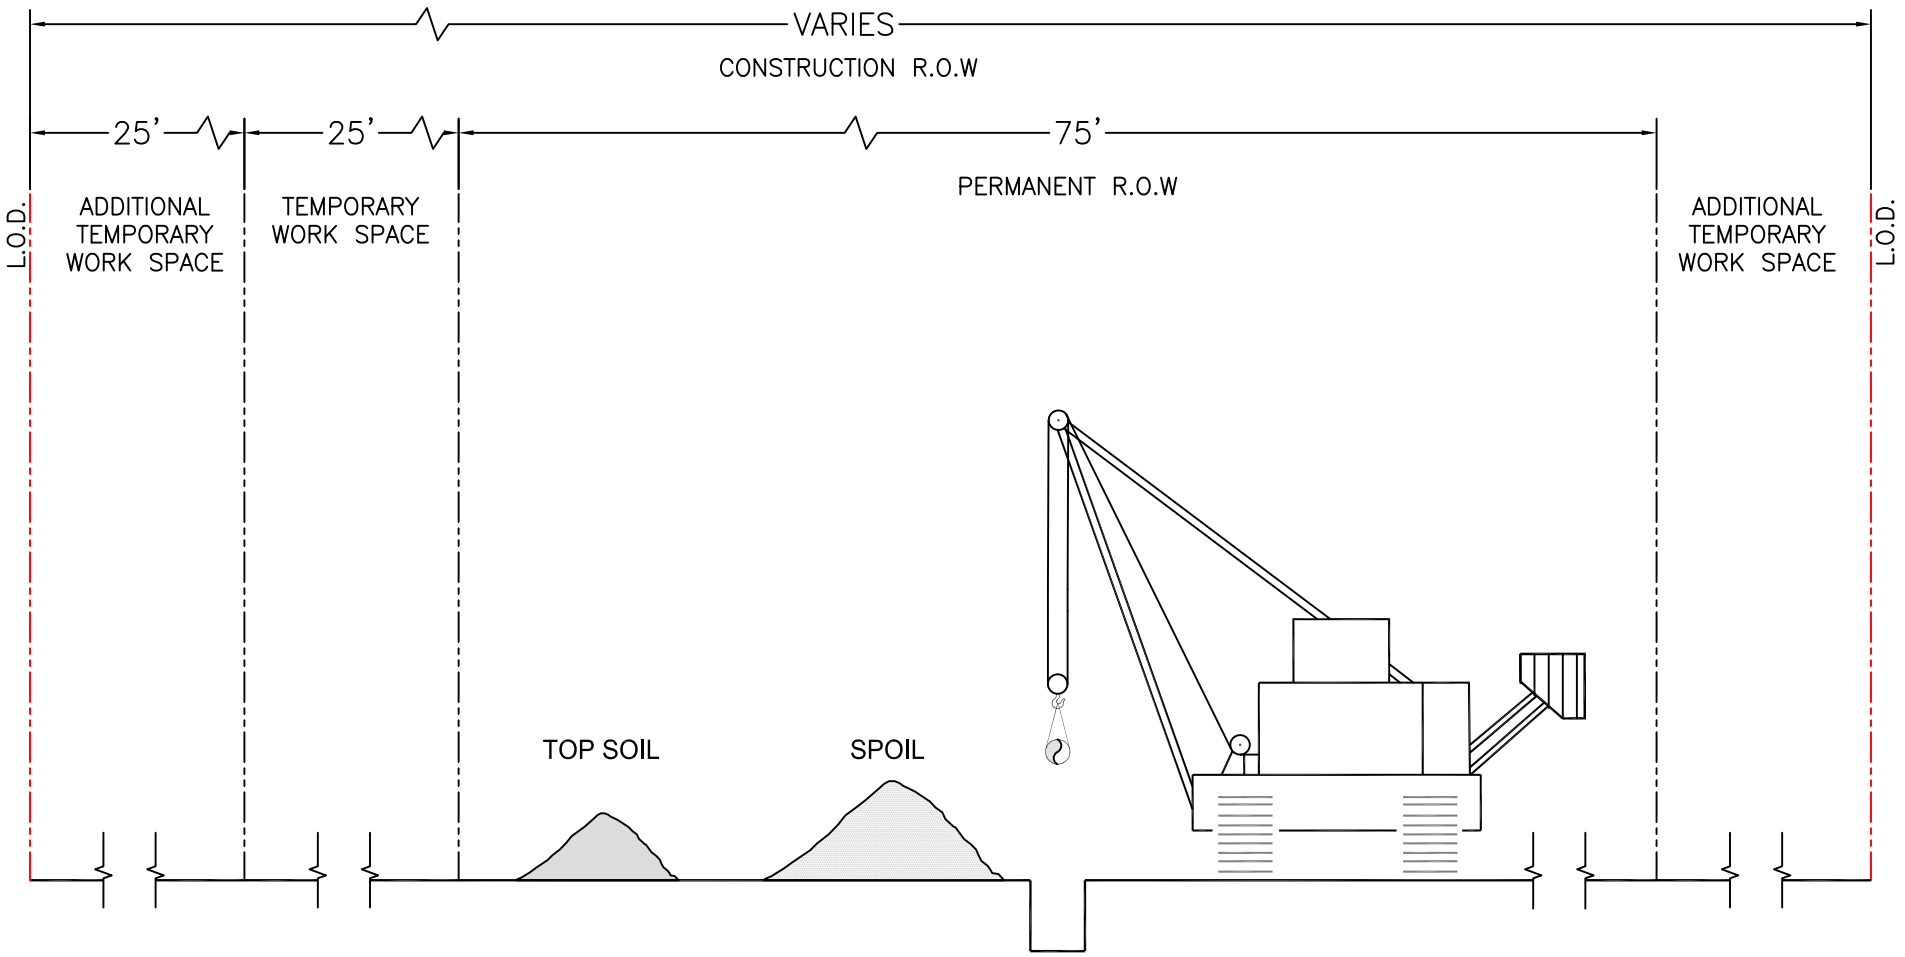

National Fuel® Supply Corporation

NATIONAL FUEL GAS SUPPLY CORPORATION
SHIPPINGPORT LATERAL CONSTRUCTION
RIGHT-OF-WAY TYPICAL DRAWING
FIGURE 3

F:\Eng-PA\Common\1 Expansion Projects - JJK\A - Line N Lateral Project\ROW Figures

SHIPPINGPORT LATERAL TYPICAL FIGURE #4

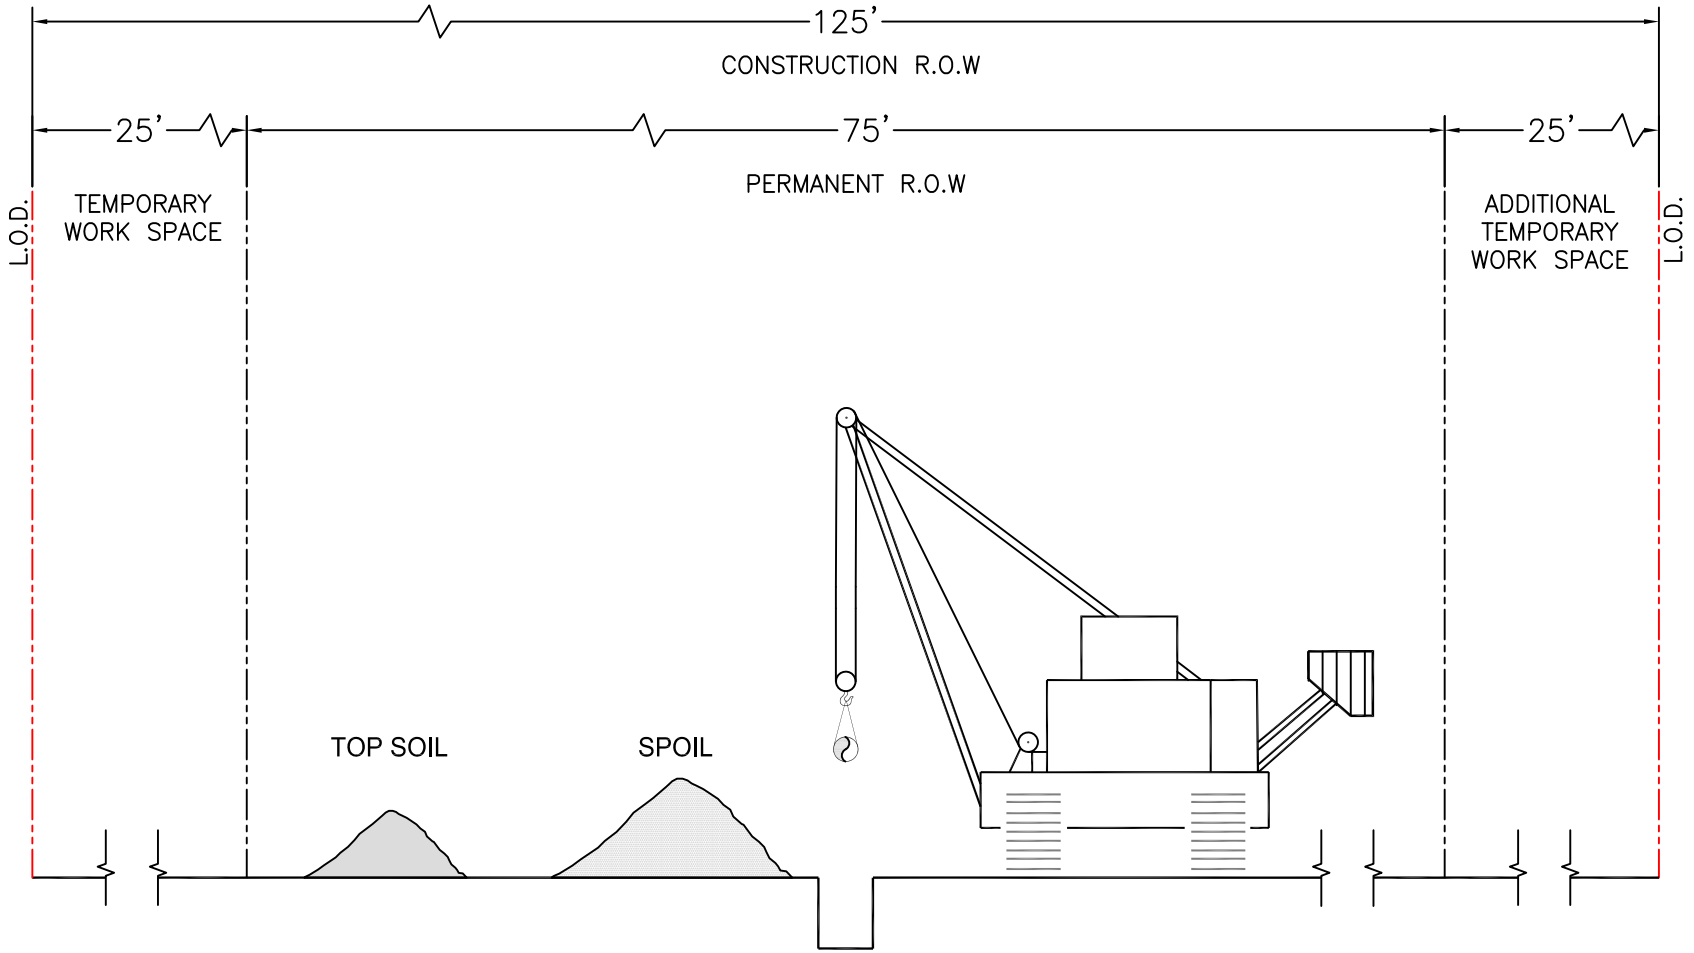

National Fuel® Supply Corporation

NATIONAL FUEL GAS SUPPLY CORPORATION
SHIPPINGPORT LATERAL CONSTRUCTION
RIGHT-OF-WAY TYPICAL DRAWING
FIGURE 4

F:\Eng-PA\Common\1 Expansion Projects - JJK\A - Line N Lateral Project\ROW Figures

SHIPPINGPORT LATERAL TYPICAL FIGURE #5

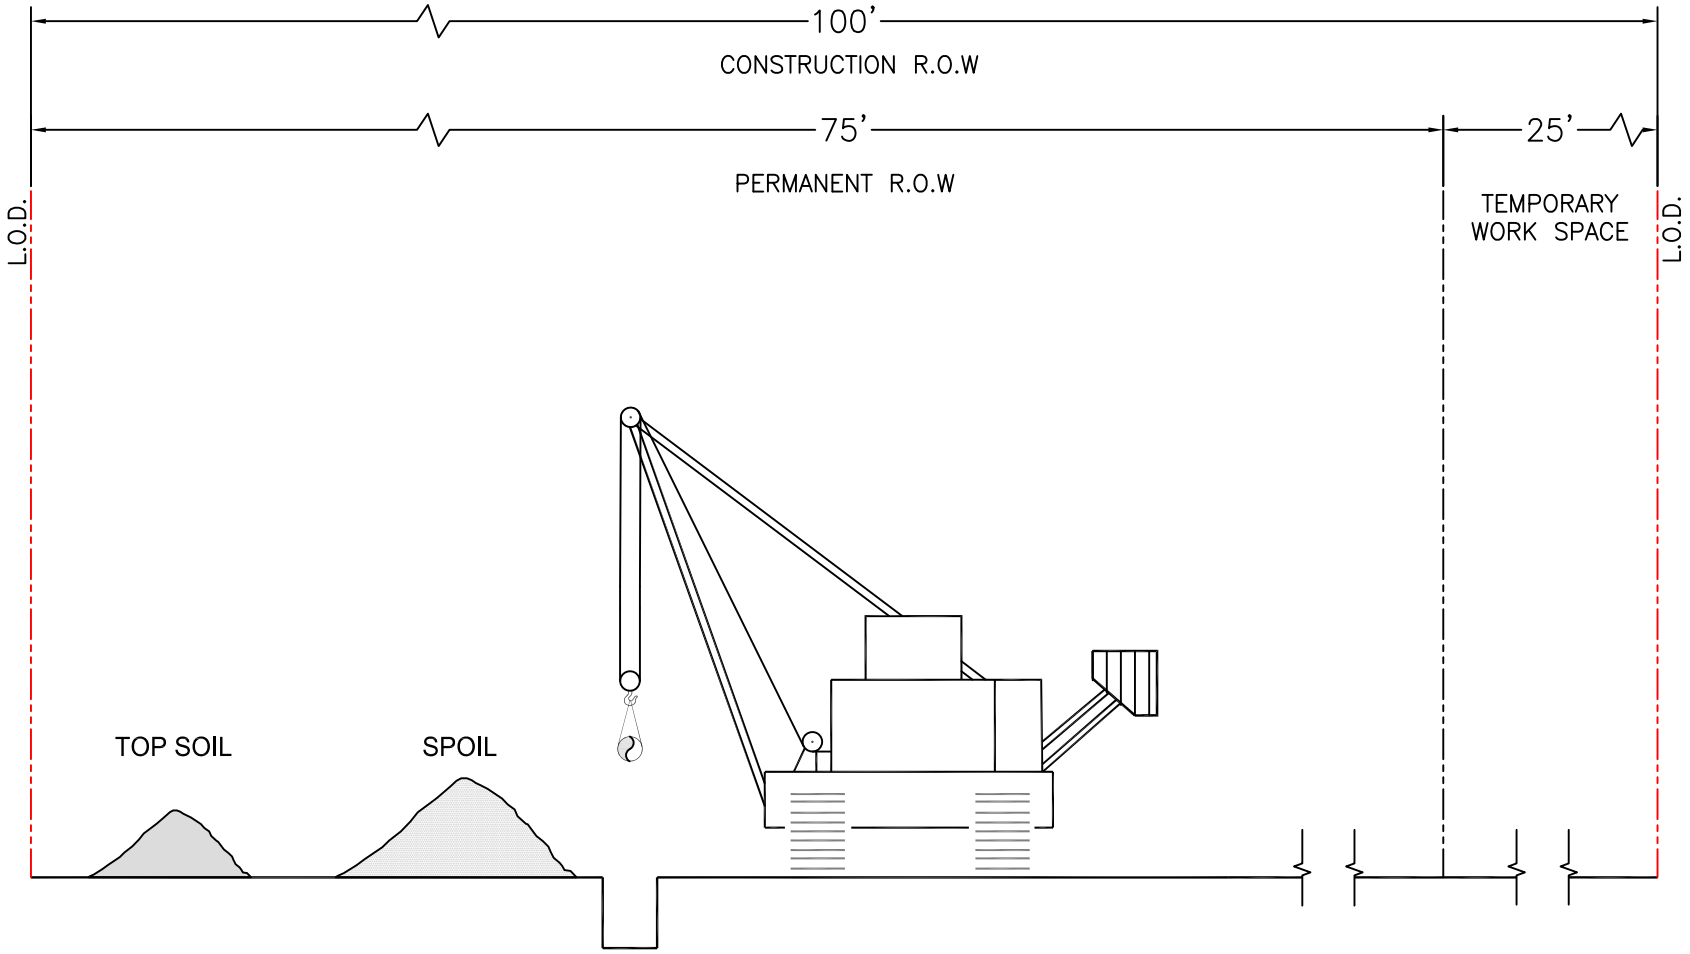

National Fuel®
Supply Corporation

NATIONAL FUEL GAS SUPPLY CORPORATION
SHIPPINGPORT LATERAL CONSTRUCTION
RIGHT-OF-WAY TYPICAL DRAWING
FIGURE 5

F:\Eng-PA\Common\1 Expansion Projects - JJK\A - Line N Lateral Project\ROW Figures

SHIPPINGPORT LATERAL TYPICAL FIGURE #6

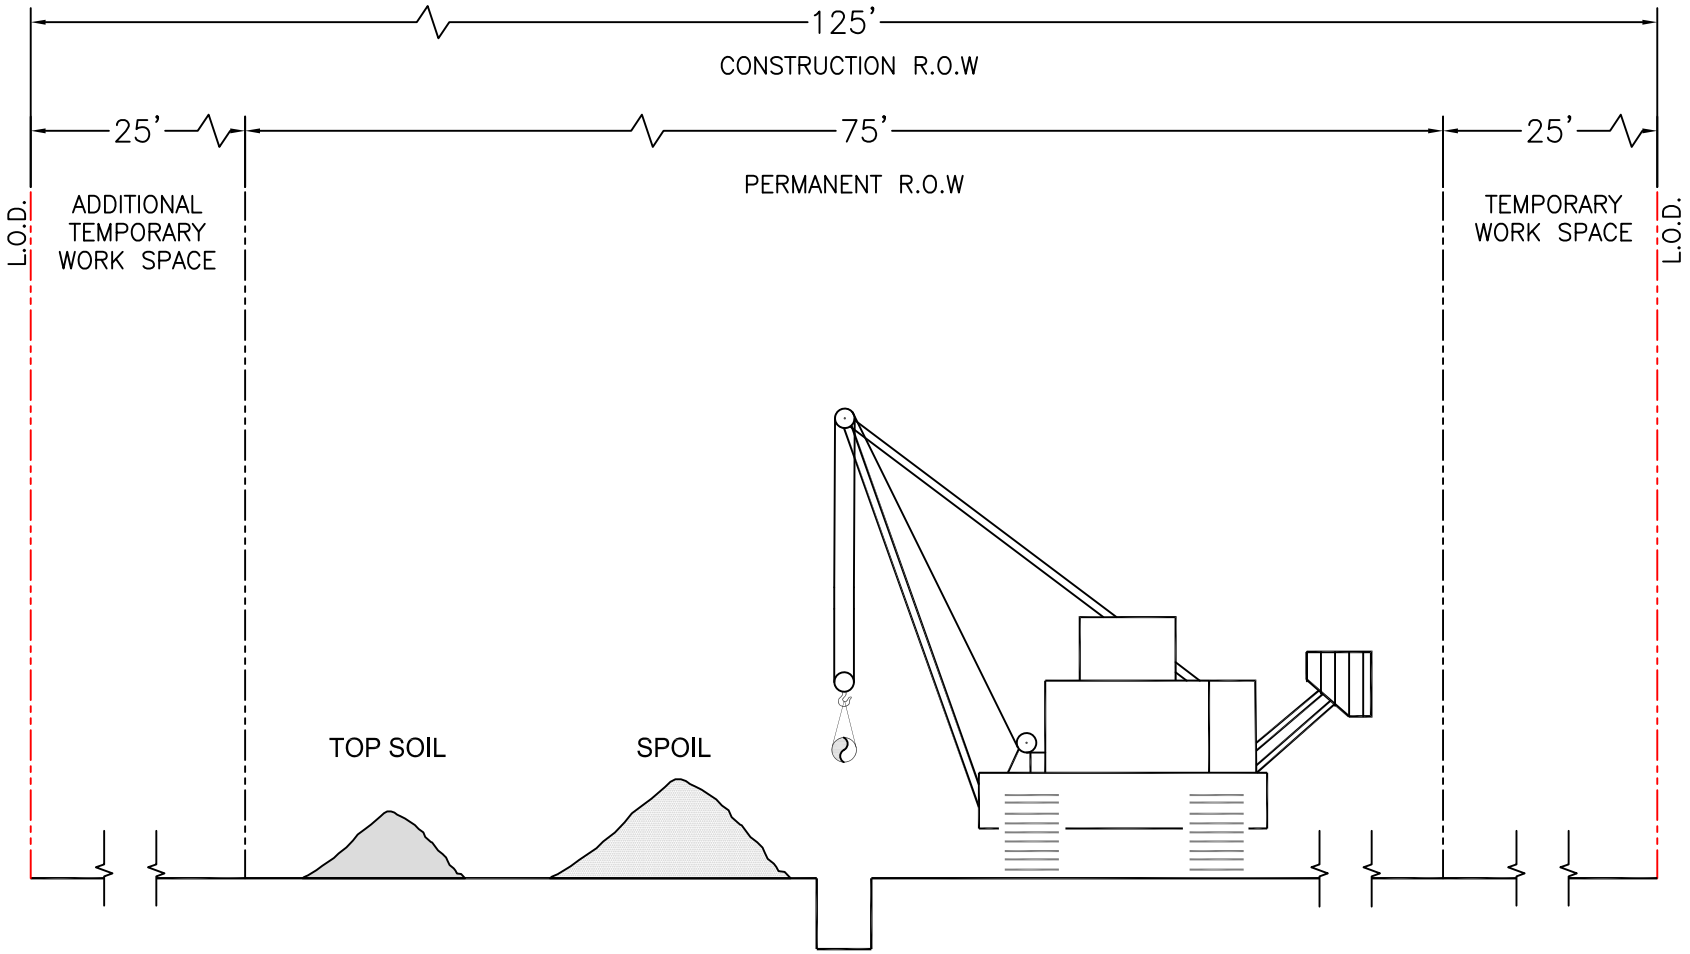

National Fuel® Supply Corporation

NATIONAL FUEL GAS SUPPLY CORPORATION
SHIPPINGPORT LATERAL CONSTRUCTION
RIGHT-OF-WAY TYPICAL DRAWING
FIGURE 6

F:\Eng-PA\Common\1 Expansion Projects - JJK\A - Line N Lateral Project\ROW Figures

SHIPPINGPORT LATERAL TYPICAL FIGURE #7

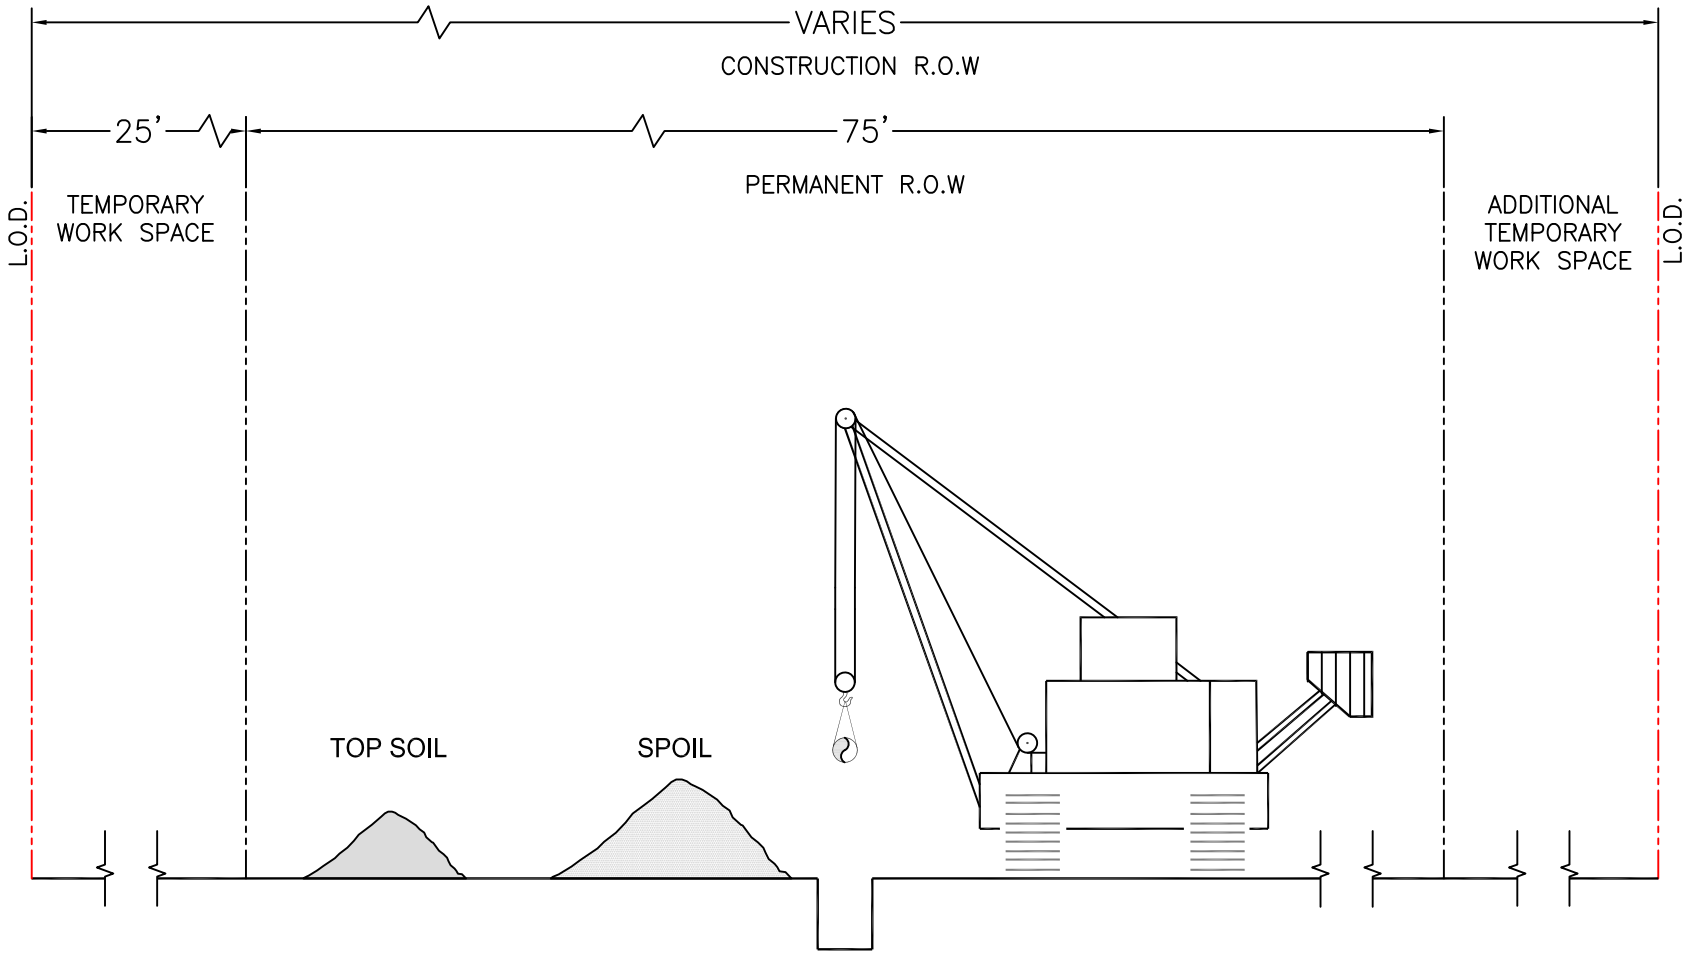

National Fuel® Supply Corporation

NATIONAL FUEL GAS SUPPLY CORPORATION
SHIPPINGPORT LATERAL CONSTRUCTION
RIGHT-OF-WAY TYPICAL DRAWING
FIGURE 7

F:\Eng-PA\Common\1 Expansion Projects - JJK\A - Line N Lateral Project\ROW Figures